


JOB NO.	0721B
---------	-------

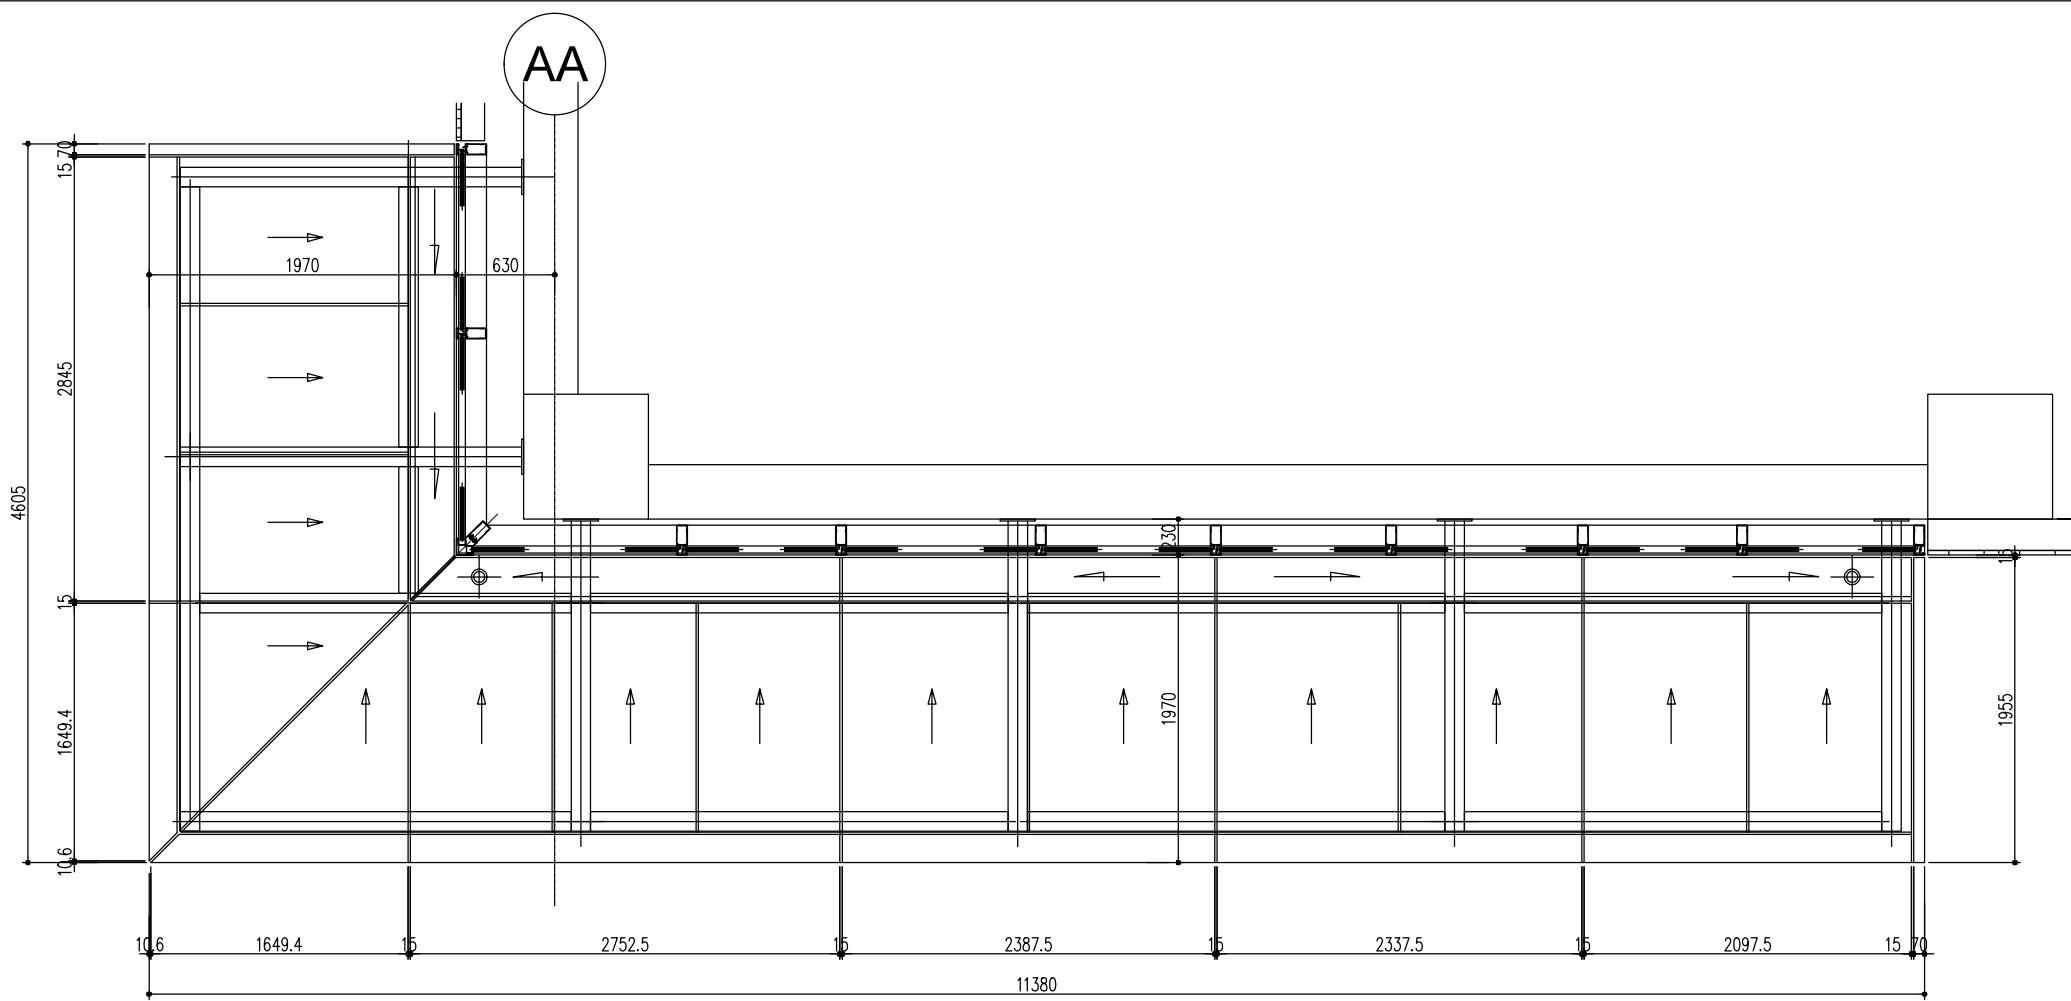


入口雨遮平面詳圖

N.T.S.

UNIT =mm

1
-

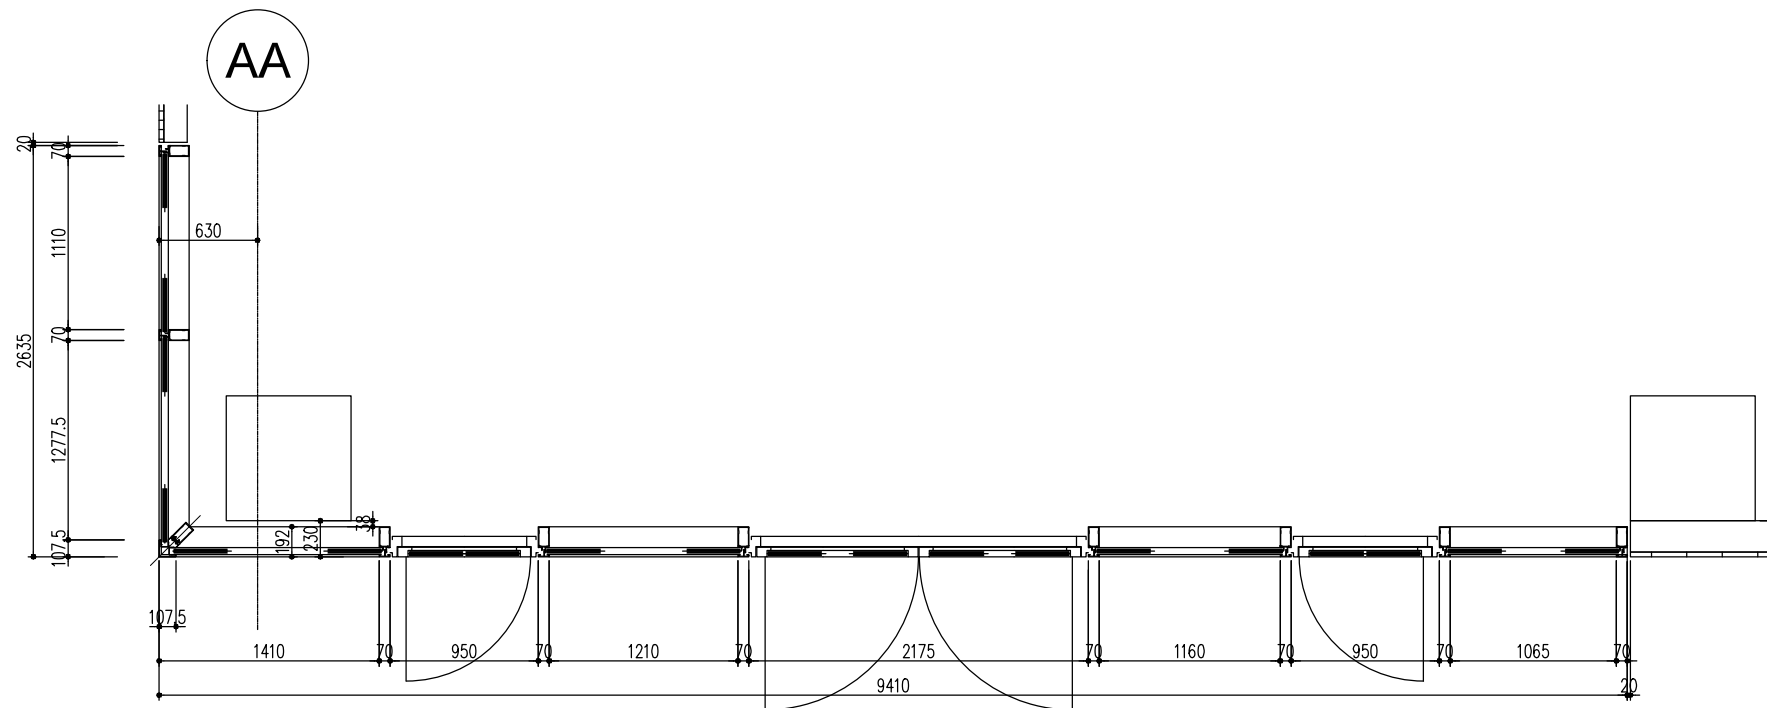


帷幕牆平面詳圖

N.T.S.

UNIT =mm

2
-

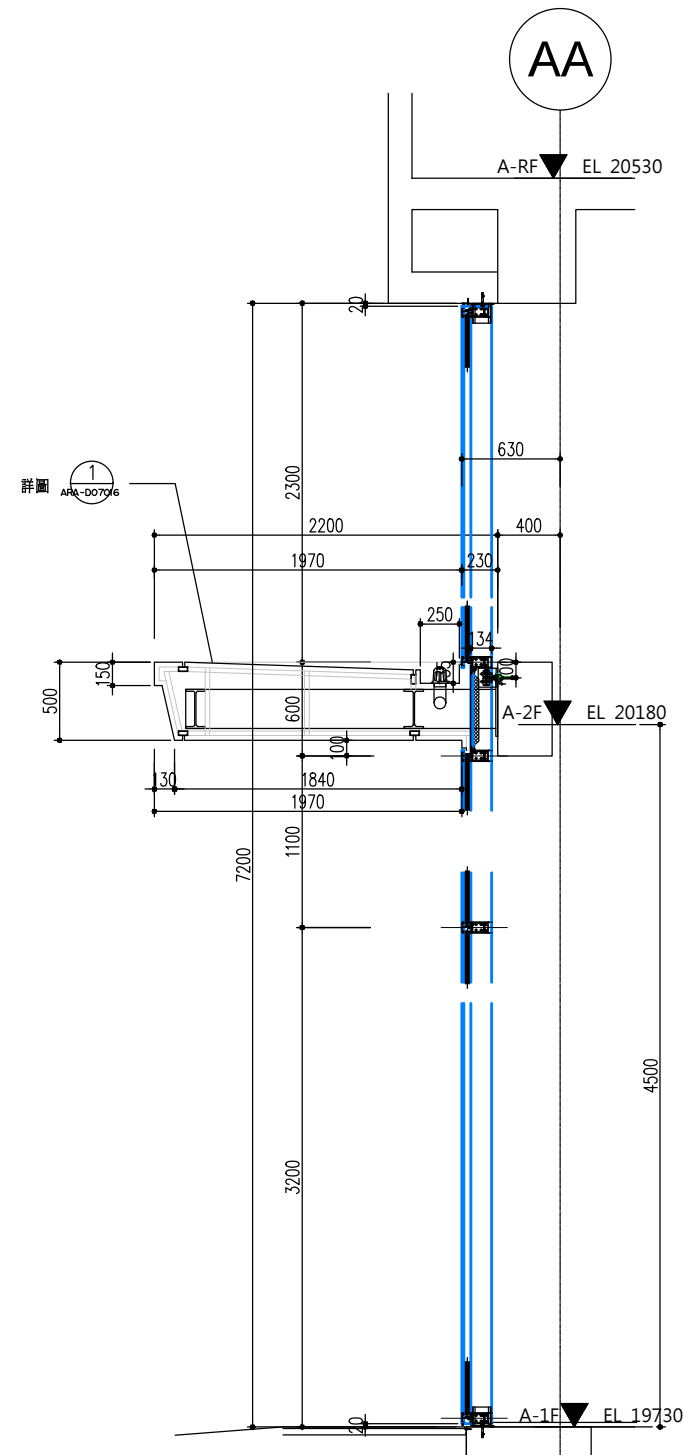

帷幕牆及入口雨遮剖面圖

N.T.S.

UNIT =mm

3
-

統一企業集團桃園U-PARK智匯產業園區
建築新建工程
U-PARK PROJECT
統流開發股份有限公司
UNI-PRESIDENT EXPRESS CORP. TAIPEI, TAIWAN, R.O.C.


玻璃帷幕平剖面圖

華興聯合建築師事務所
HWA SHIN ARCHITECTS

DWG. NO.
0721B-ARA-D07015

JOB NO.
0721B

ISSUE NO.

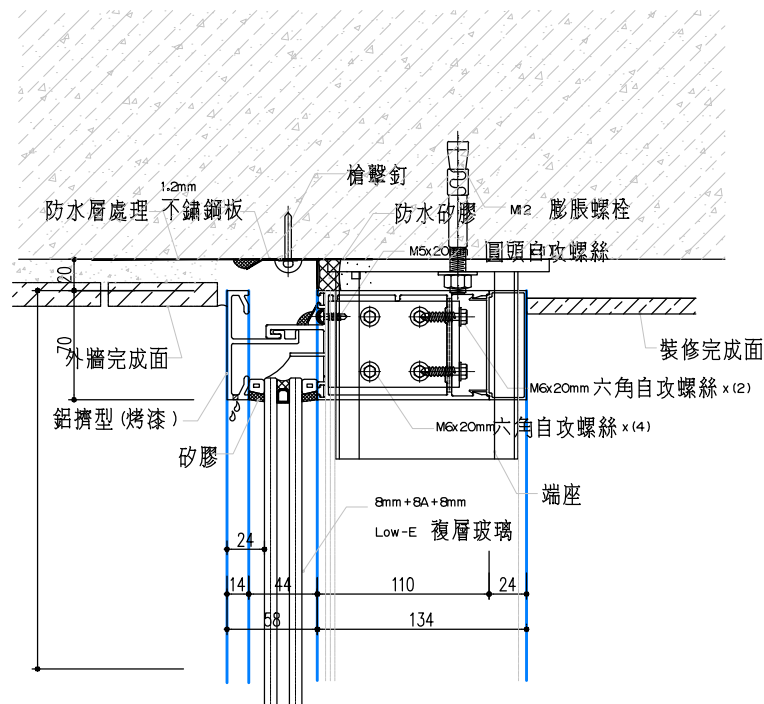


帷幕牆斷面詳圖

N.T.S.

UNIT=mm

1

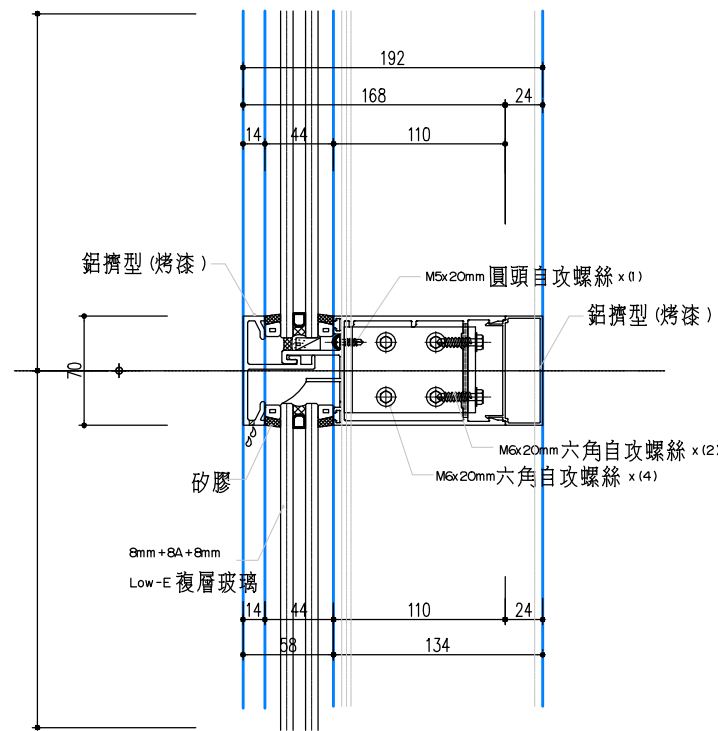


帷幕牆斷面詳圖

N.T.S.

UNIT=mm

2

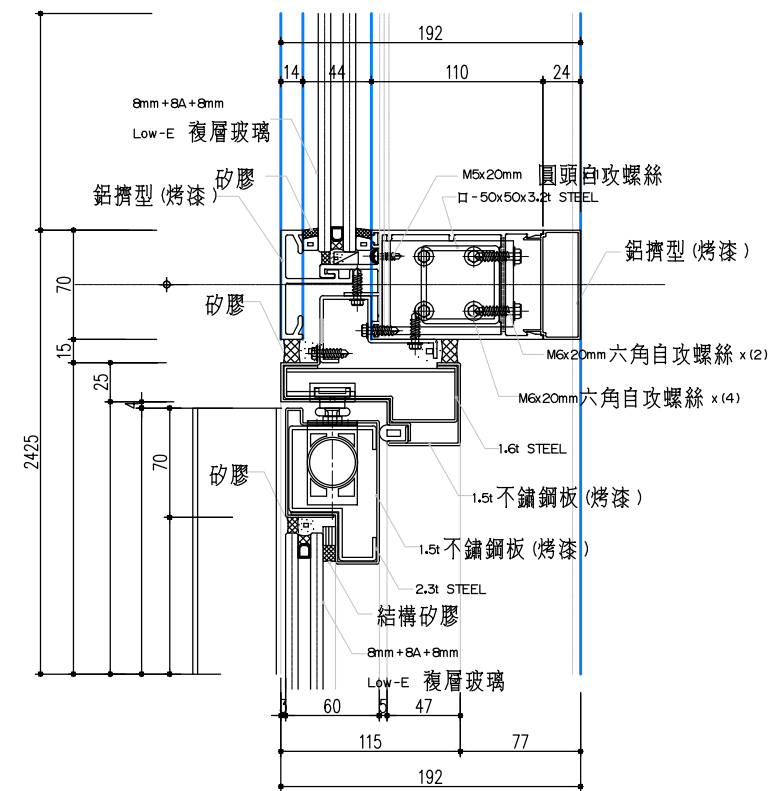


帷幕牆斷面詳圖

N.T.S.

UNIT=mm

3

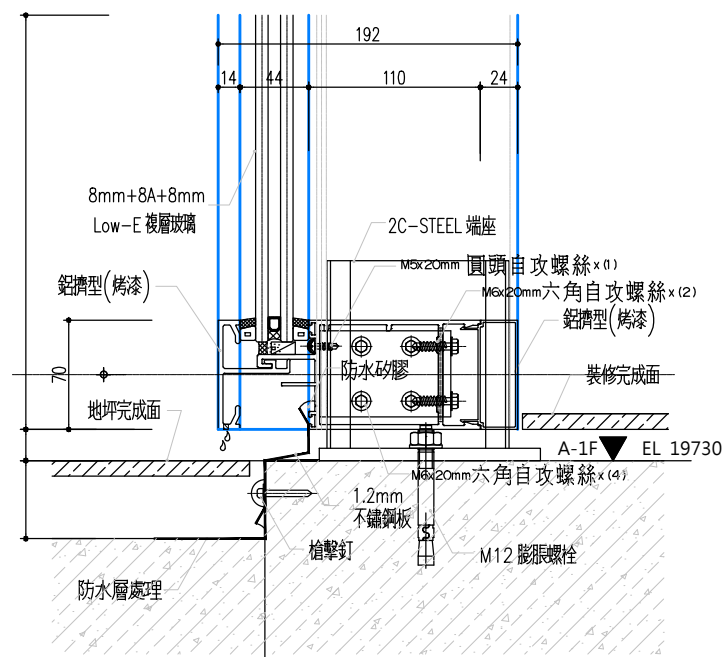


帷幕牆斷面詳圖

N.T.S.

UNIT=mm

4

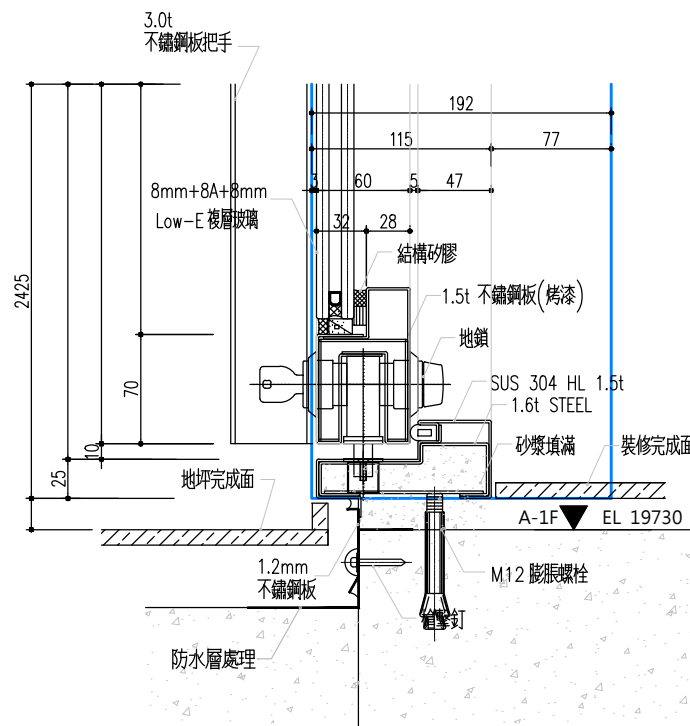

帷幕牆斷面詳圖

N.T.S.

UNIT=mm

5

統一企業集團桃園U-PARK智匯產業園區
建築新建工程
U-PARK PROJECT
統流開發股份有限公司
UNI-PRESIDENT EXPRESS CORP. TAIPEI, TAIWAN, R.O.C.


玻璃帷幕詳圖(二)

華興聯合建築師事務所
HWA SHIN ARCHITECTS

DWG. NO.
0721B-ARA-D07017

JOB NO.
0721B

ISSUE NO.

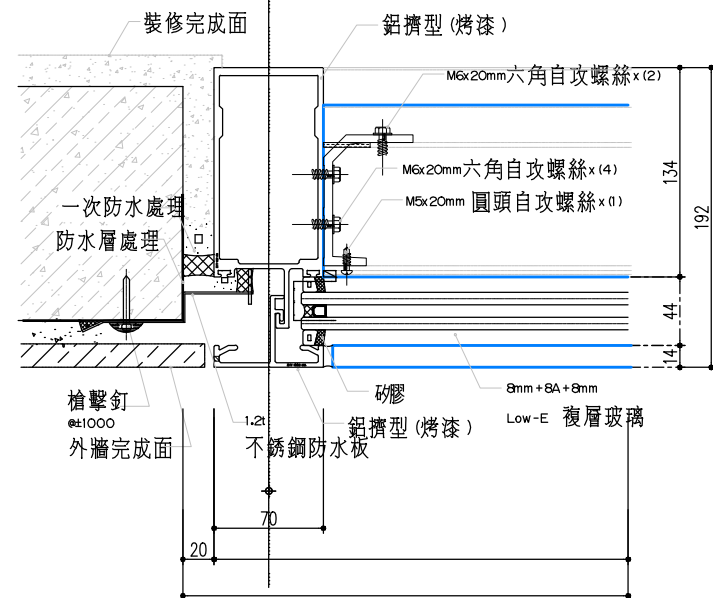


帷幕牆斷面詳圖

N.T.S.

UNIT=mm

1

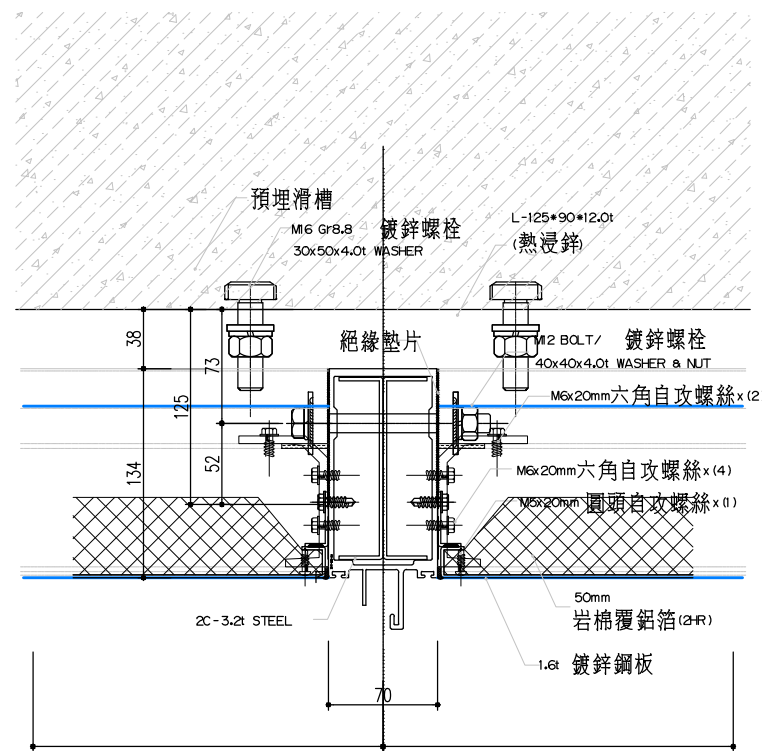


帷幕牆斷面詳圖

N.T.S.

UNIT=mm

2

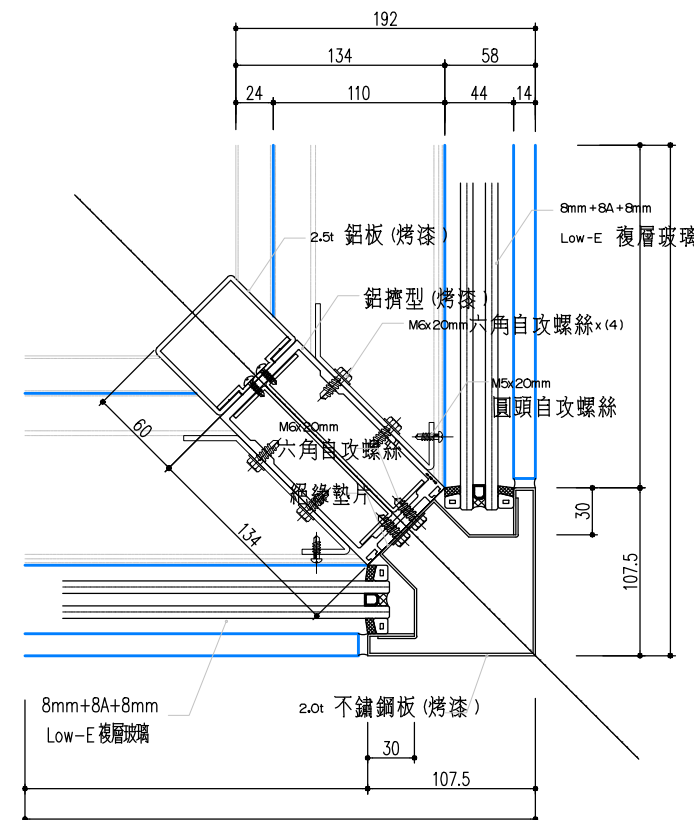


帷幕牆斷面詳圖

N.T.S.

UNIT=mm

3

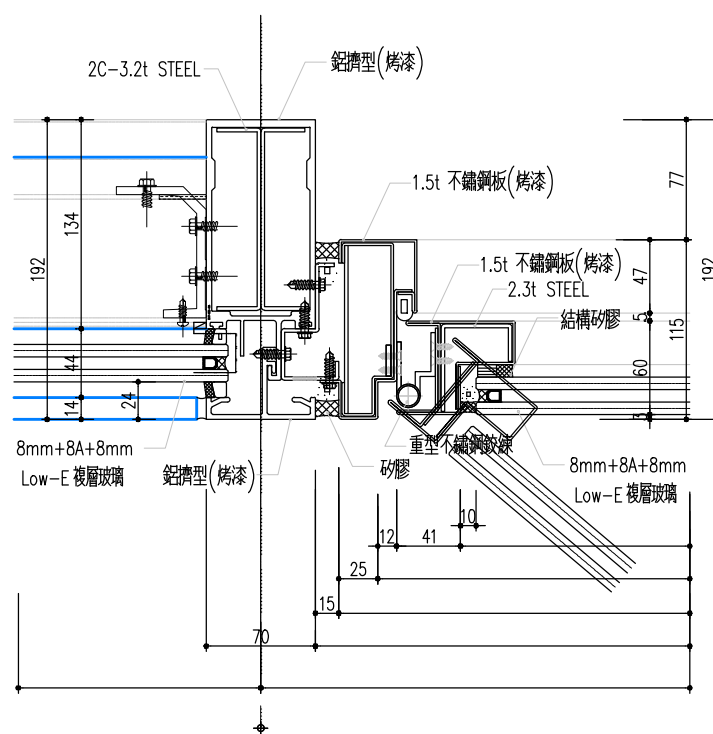


帷幕牆斷面詳圖

N.T.S.

UNIT=mm

4

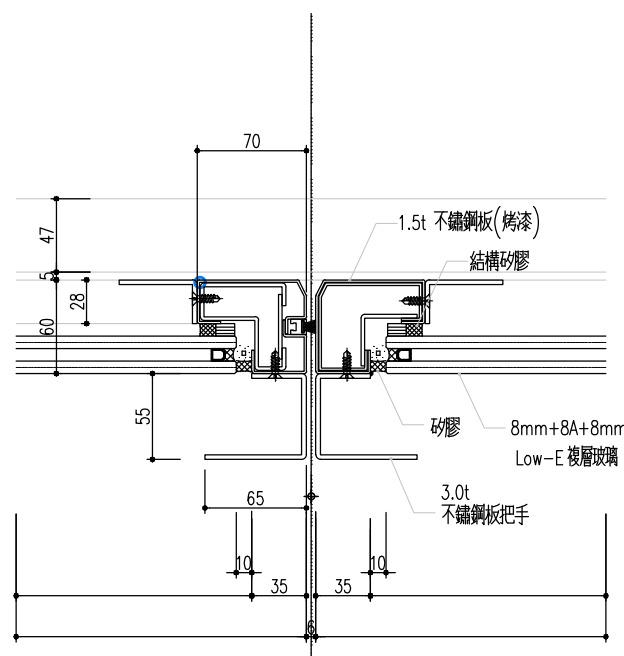


帷幕牆斷面詳圖

N.T.S.

UNIT=mm

5

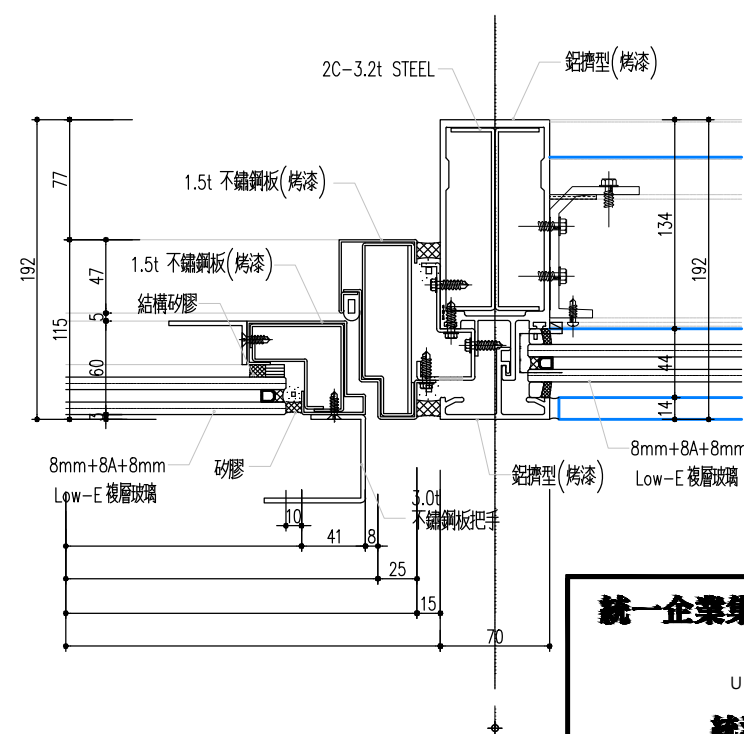

帷幕牆斷面詳圖

N.T.S.

UNIT=mm

6

統一企業集團桃園U-PARK智匯產業園區
建築新建工程
U-PARK PROJECT
統流開發股份有限公司
UNI-PRESIDENT EXPRESS CORP. TAIPEI, TAIWAN, R.O.C.


玻璃帷幕詳圖(三)

華興聯合建築師事務所
HWA SHIN ARCHITECTS


JOB NO. 0721B

DWG. NO. 0721B-ARA-D07018


ISSUE NO.

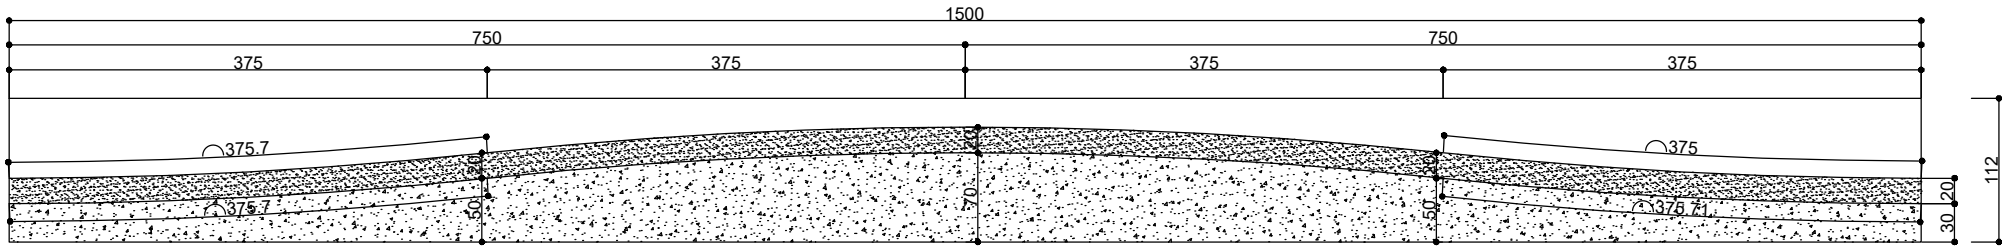


碼頭區RC護欄圖騰單元立面圖
1:60 UNIT=mm

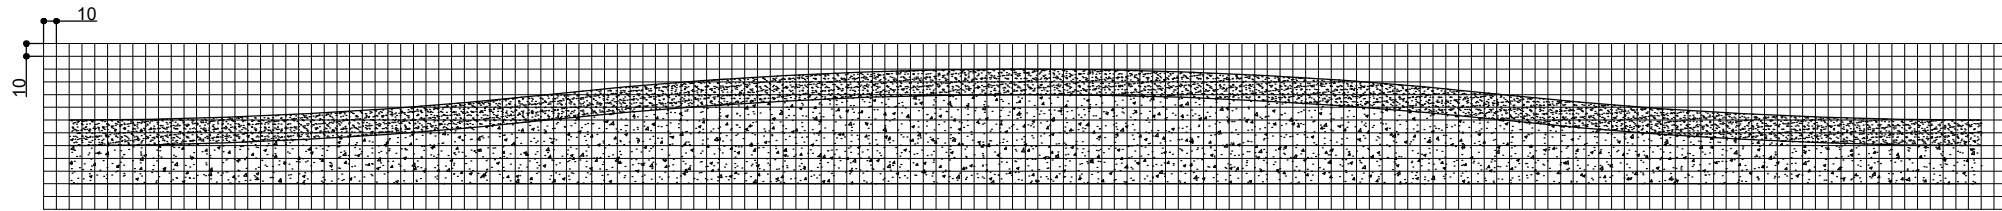


碼頭區RC護欄圖騰立面放樣圖
1:60 UNIT=mm

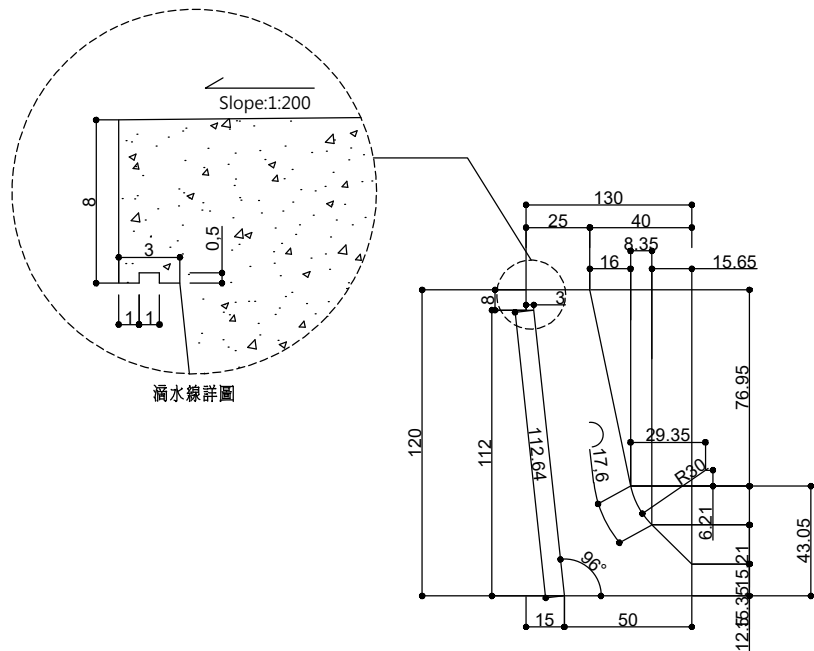

護欄粉刷剖面圖
1:30 UNIT=cm

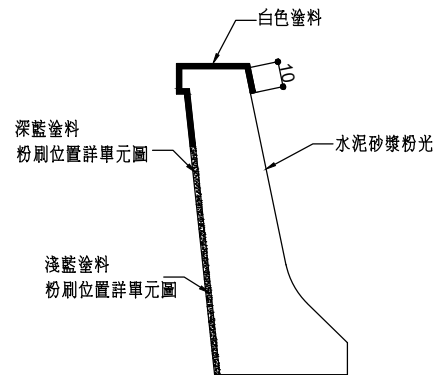

統一企業集團桃園U-PARK智匯產業園區 建築新建工程 U-PARK PROJECT 統流開發股份有限公司 UNI-PRESIDENT EXPRESS CORP. TAIPEI, TAIWAN, R.O.C.	
護欄詳圖	
 華興聯合建築師事務所 HWA SHIN ARCHITECTS	DWG. NO. 0721B-ARB-D03022
JOB NO. 0721B	ISSUE NO.

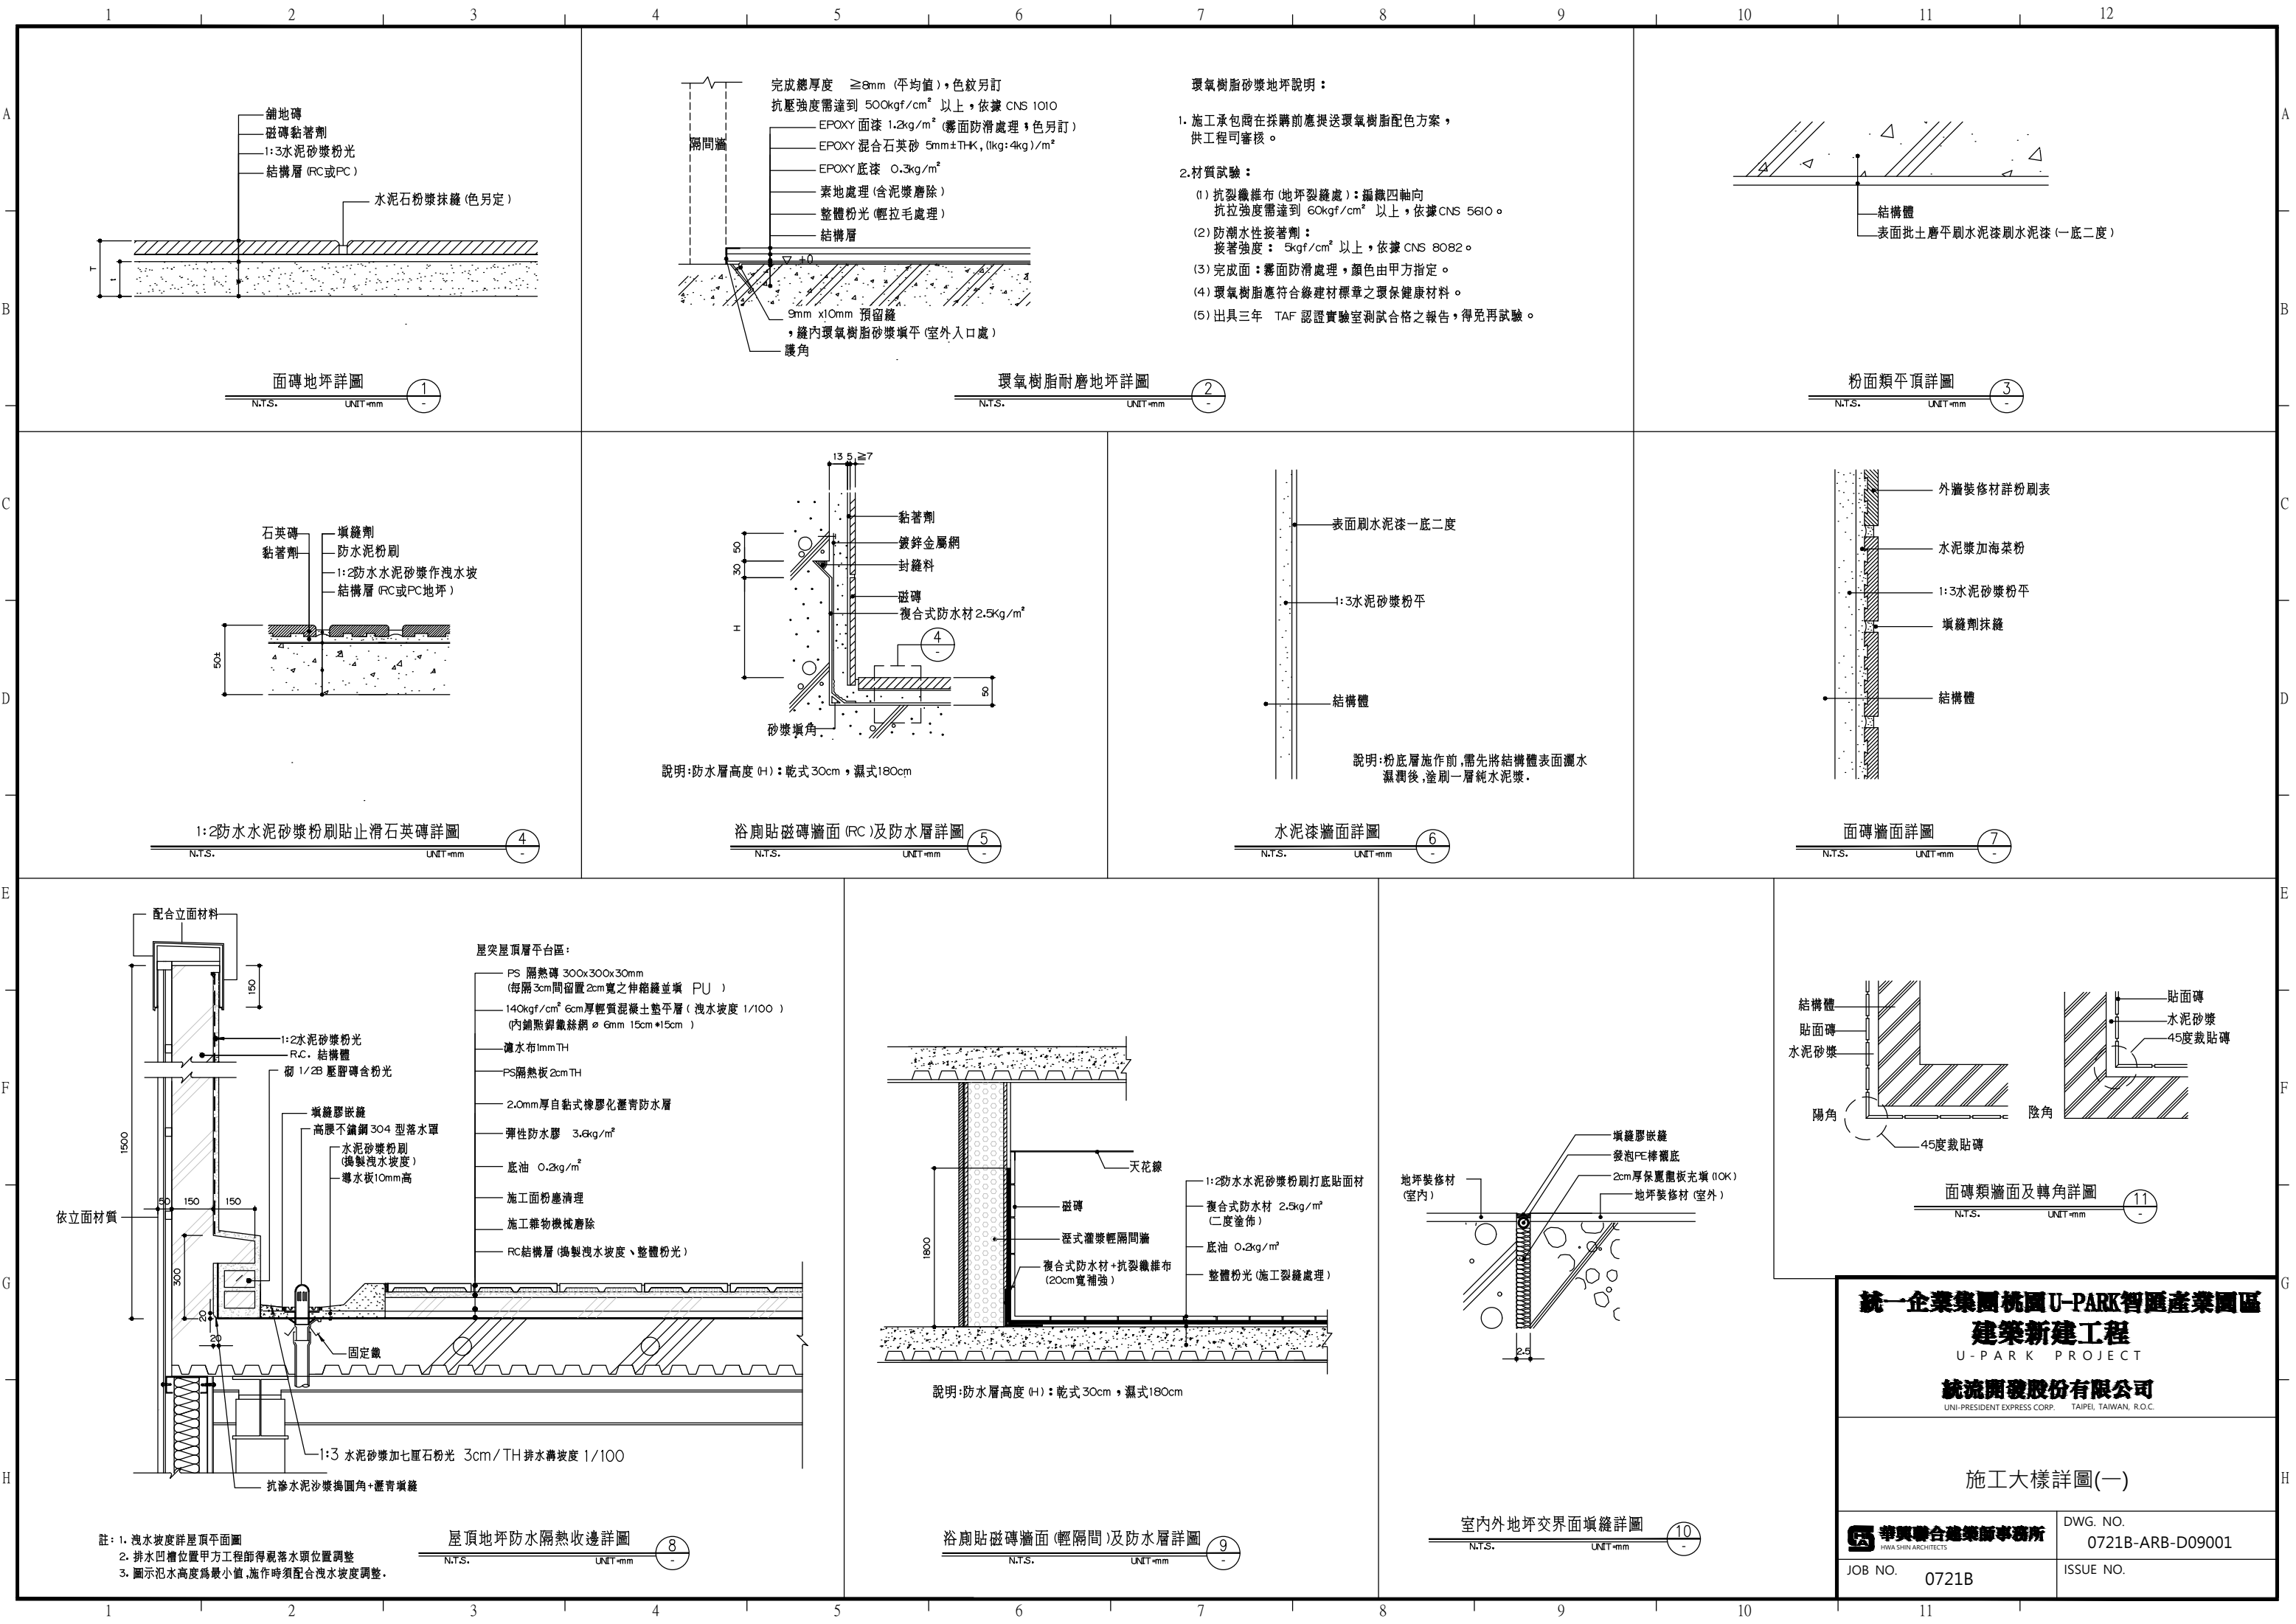

A

B

C

D

E

F

G

H

A

B

C

D

E

F

G

H

面磚地坪詳圖
N.T.S. UNIT:mm 1

環氧樹脂耐磨地坪詳圖
N.T.S. UNIT:mm 2

粉面類平頂詳圖
N.T.S. UNIT:mm 3

1:2防水水泥砂漿粉刷貼止滑石英磚詳圖
N.T.S. UNIT:mm 4

浴廁貼磁磚牆面(RC)及防水層詳圖
N.T.S. UNIT:mm 5

水泥漆牆面詳圖
N.T.S. UNIT:mm 6

面磚牆面詳圖
N.T.S. UNIT:mm 7

屋頂地坪防水隔熱收邊詳圖
N.T.S. UNIT:mm 8

浴廁貼磁磚牆面(輕隔間)及防水層詳圖
N.T.S. UNIT:mm 9

室內外地坪交界面填縫詳圖
N.T.S. UNIT:mm 10

面磚類牆面及轉角詳圖
N.T.S. UNIT:mm 11

施工大樣詳圖(一)

註：1. 洩水坡度詳屋頂平面圖
2. 排水凹槽位置甲方工程師得視落水頭位置調整
3. 圖示汎水高度為最小值,施作時須配合洩水坡度調整。

統一企業集團桃園U-PARK智匯產業園區

建築新建工程

U-PARK PROJECT

統流開發股份有限公司

UNI-PRESIDENT EXPRESS CORP. TAIPEI, TAIWAN, R.O.C.

DWG. NO.

0721B-ARB-D09001



JOB NO.

0721B

ISSUE NO.

華寅聯合建築師事務所

HWA SHIN ARCHITECTS

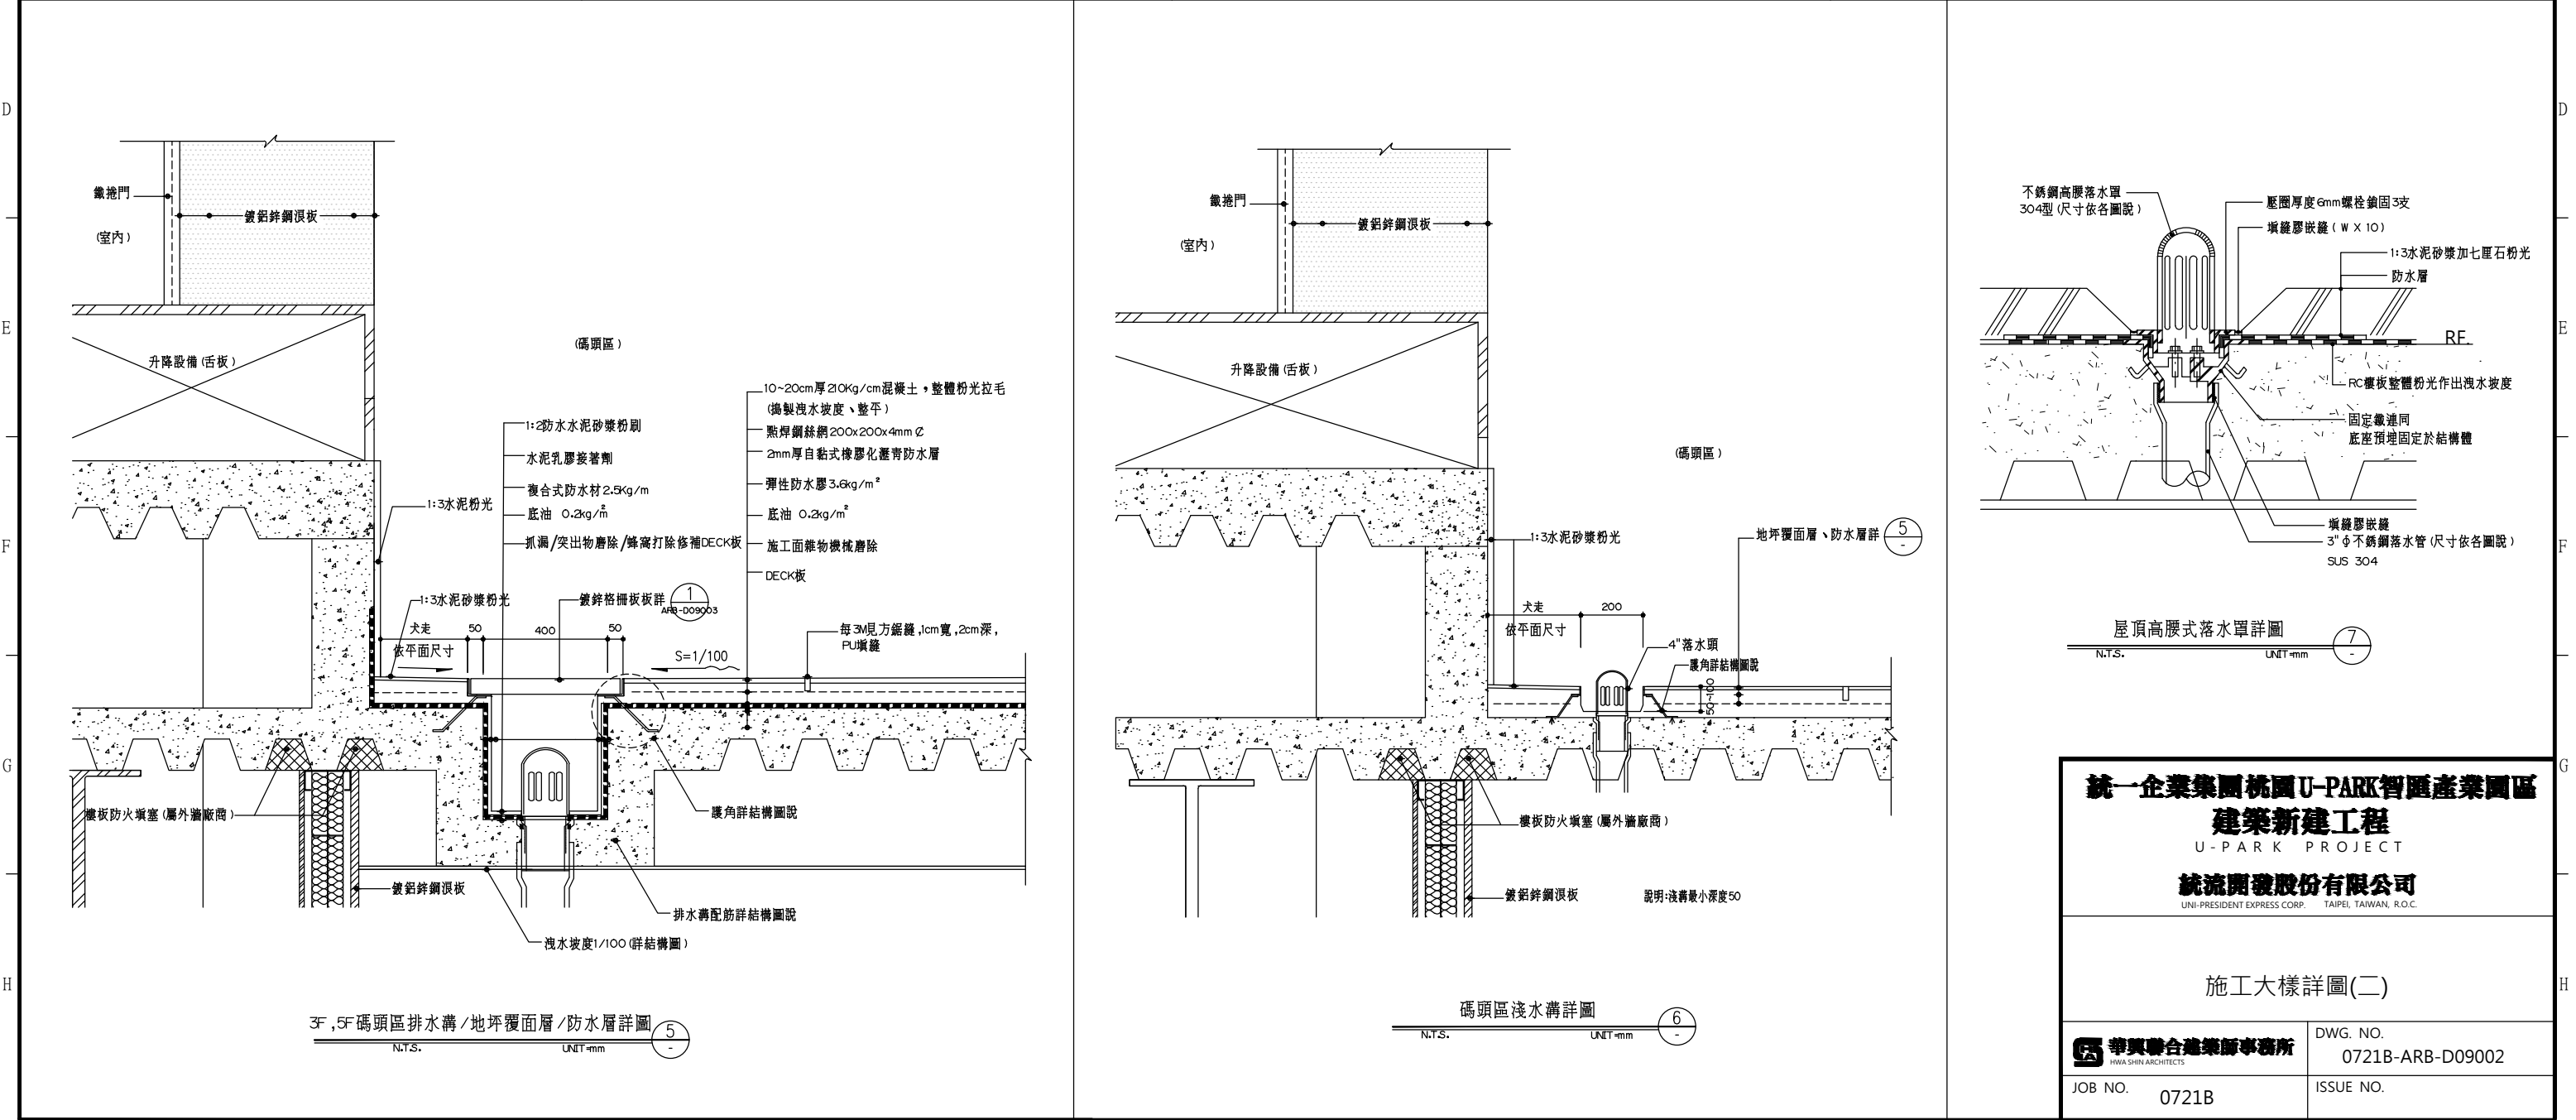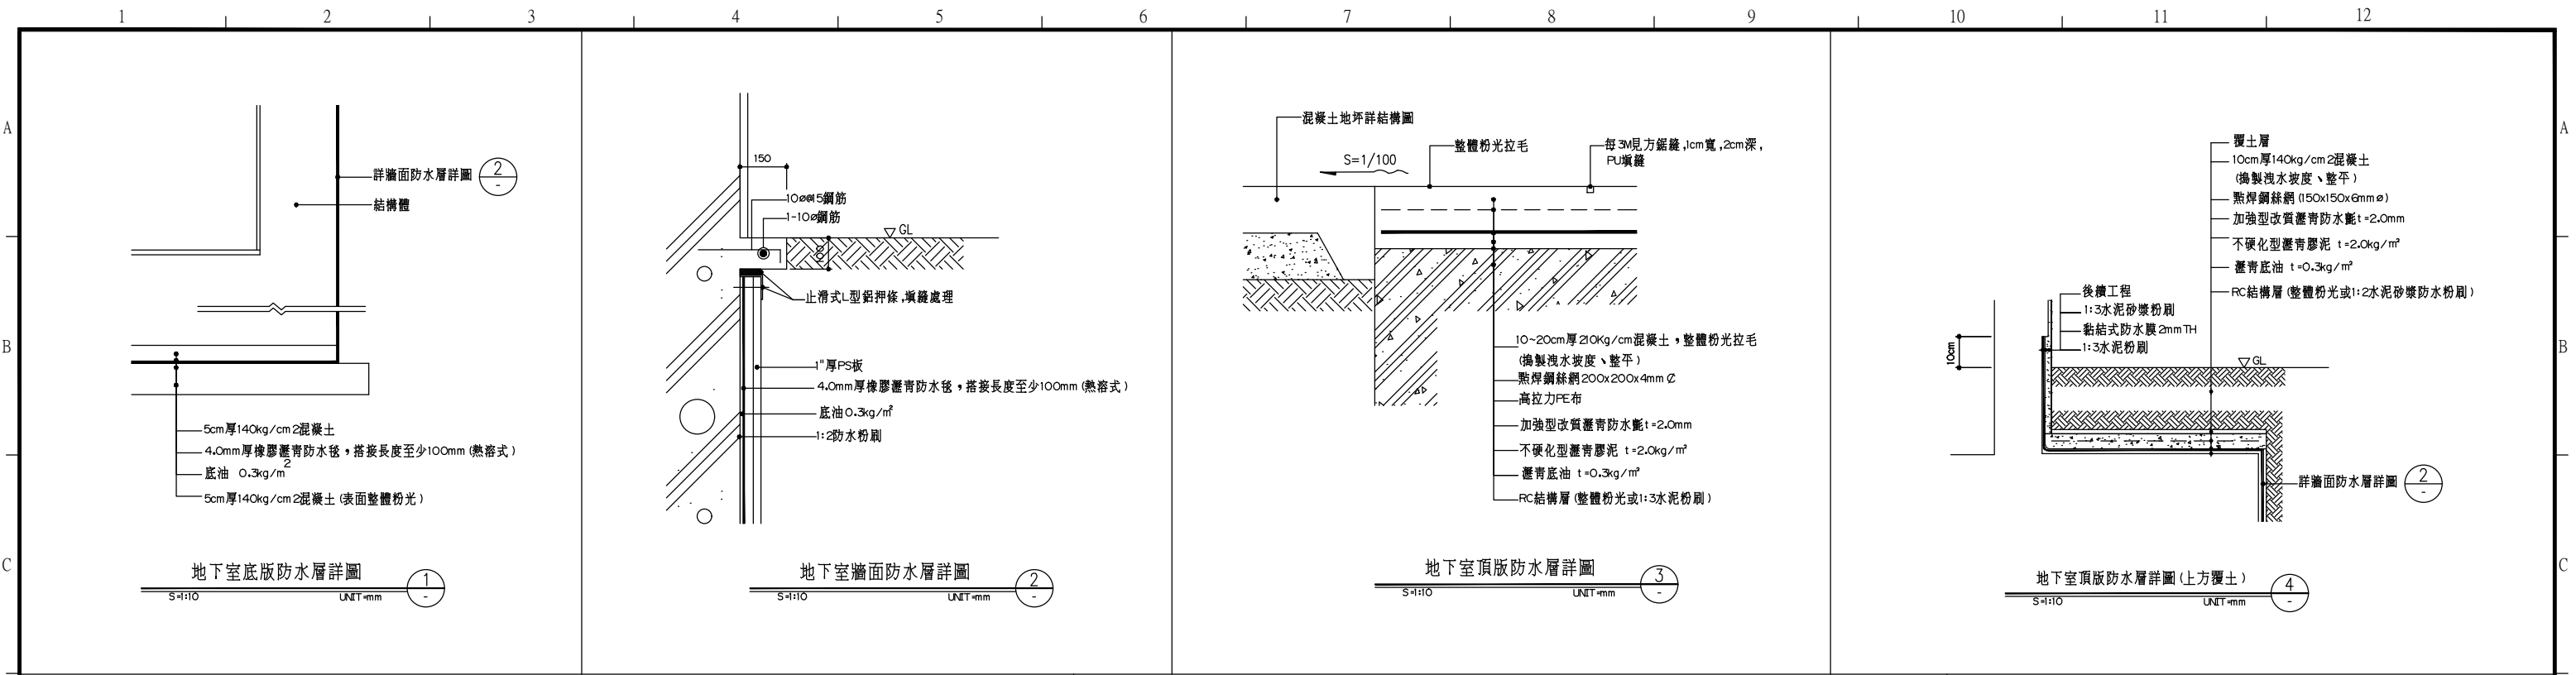

統一企業集團桃園U-PARK智匯產業園區

建築新建工程

U-PARK PROJECT

統流開發股份有限公司

UNI-PRESIDENT EXPRESS CORP. TAIPEI, TAIWAN, R.O.C.

施工大樣詳圖(二)


 華興聯合建築師事務所

HWA SHIN ARCHITECTS

DWG. NO.
0721B-ARB-D09002









JOB NO.
0721B

ISSUE NO.

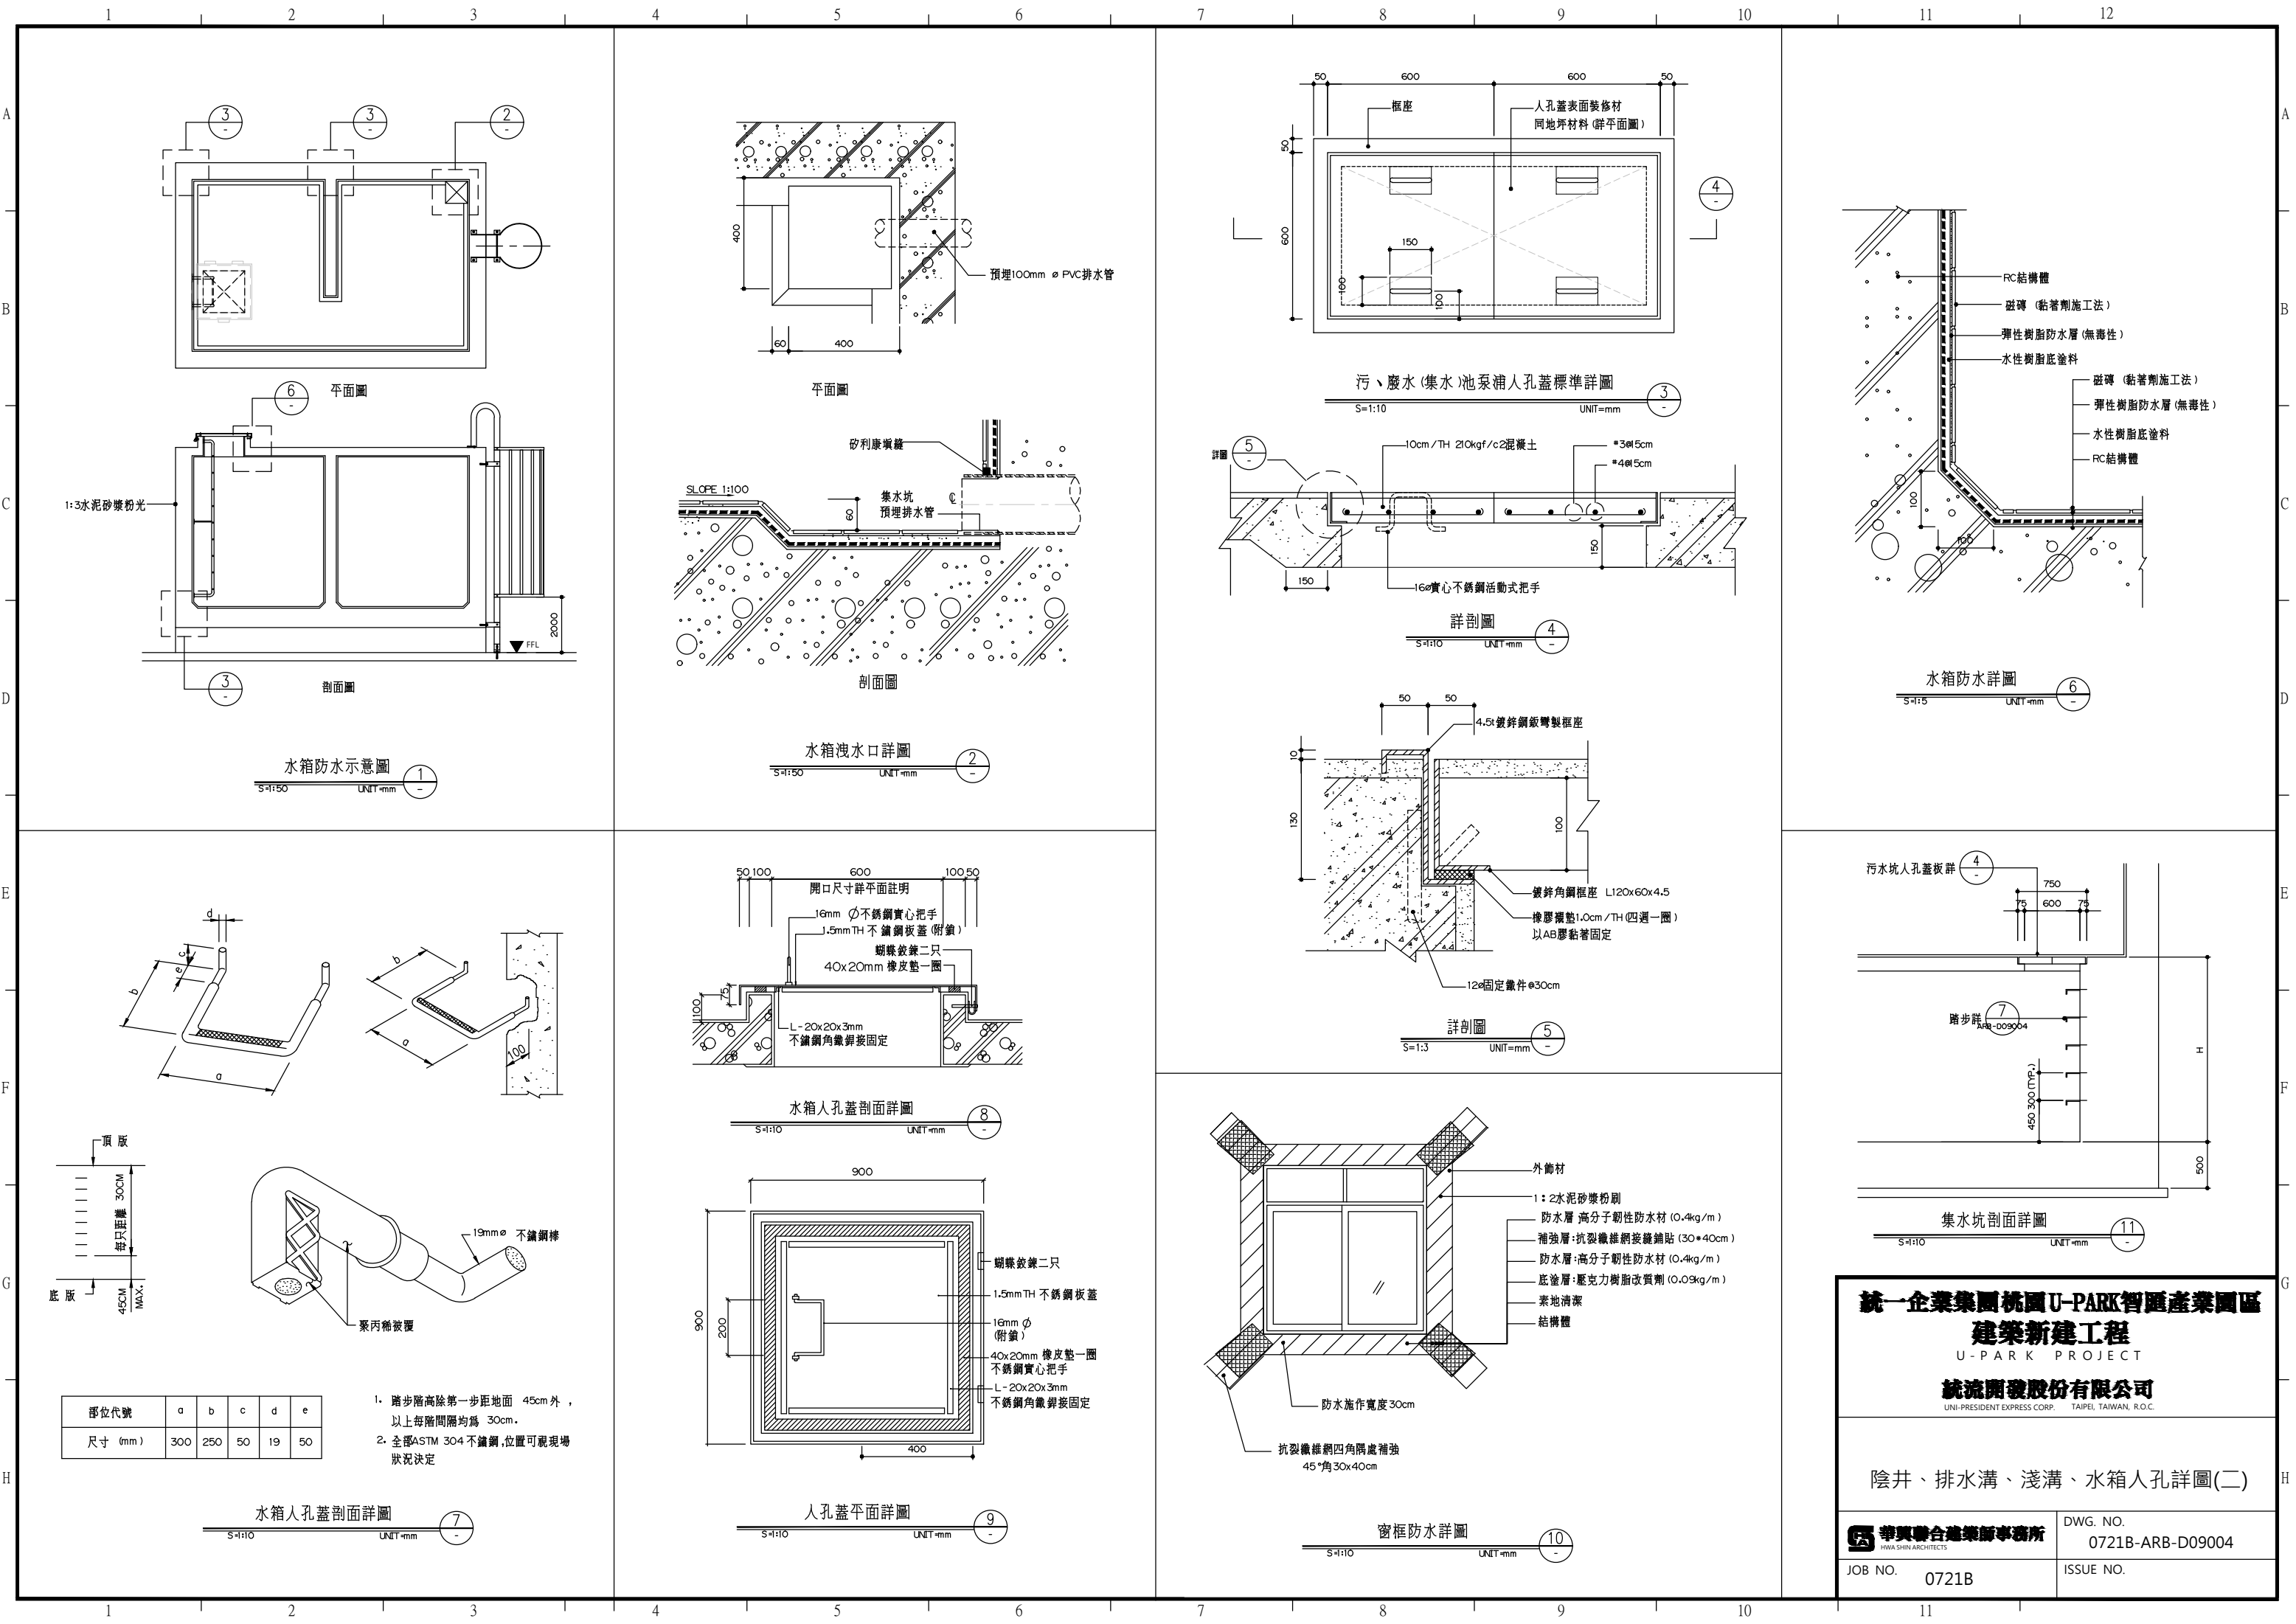

A
B
C
D
E
F
G
H

A
B
C
D
E
F
G
H

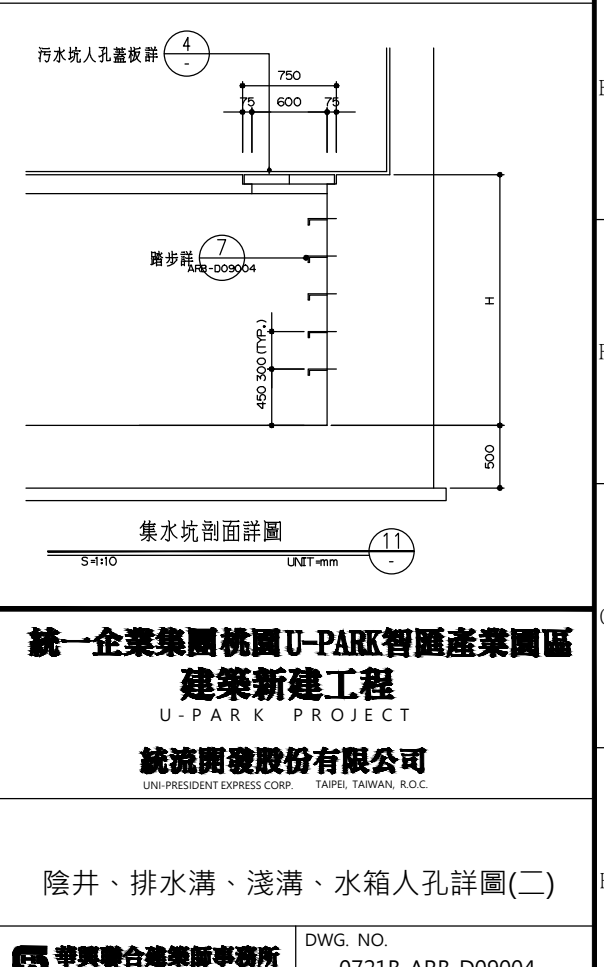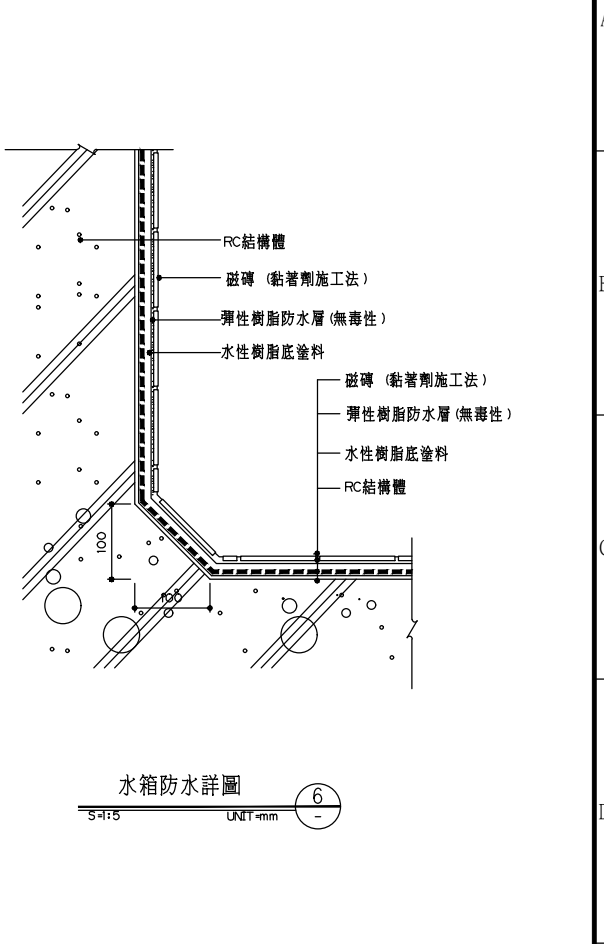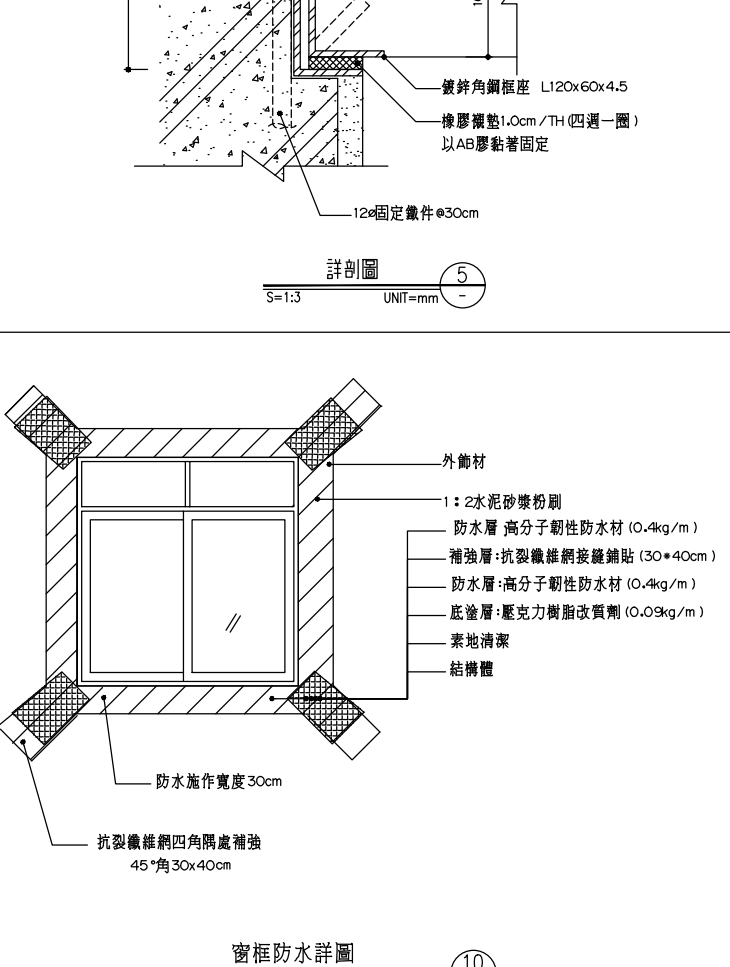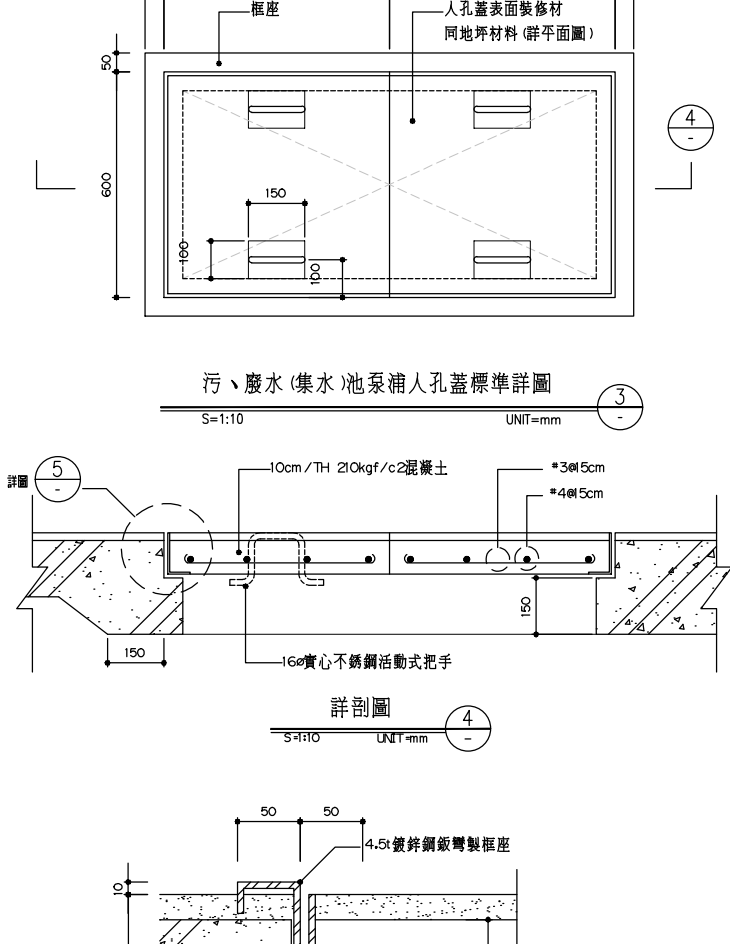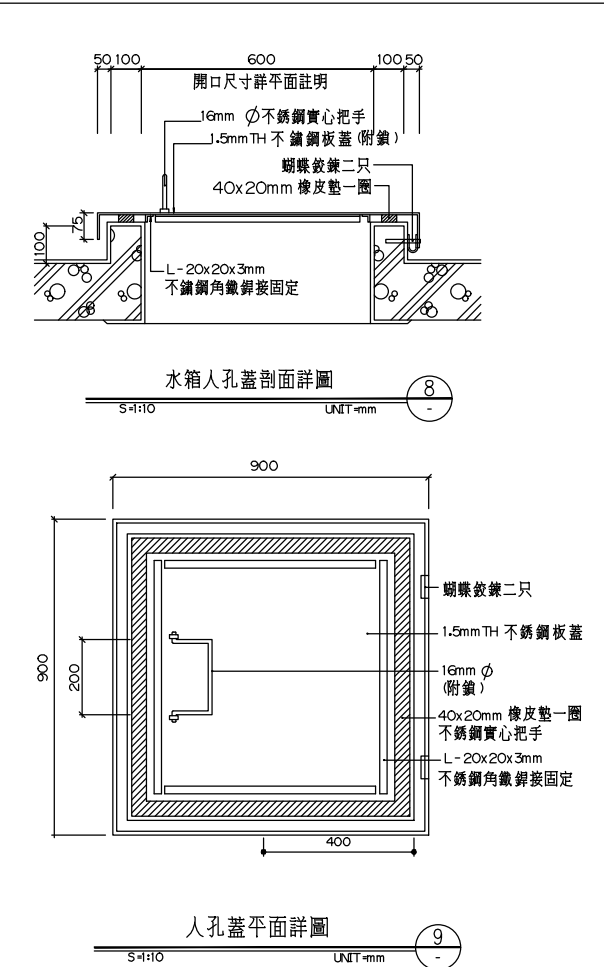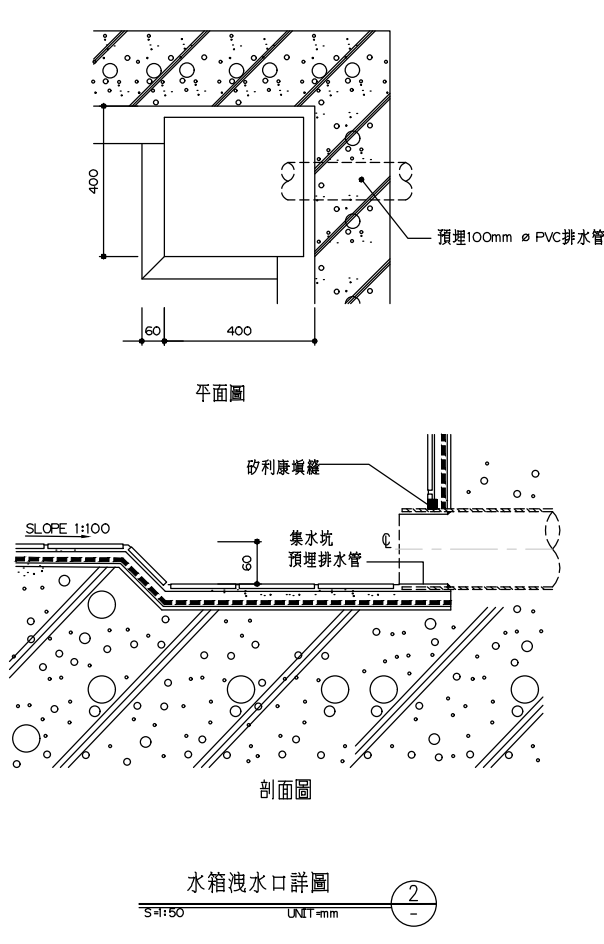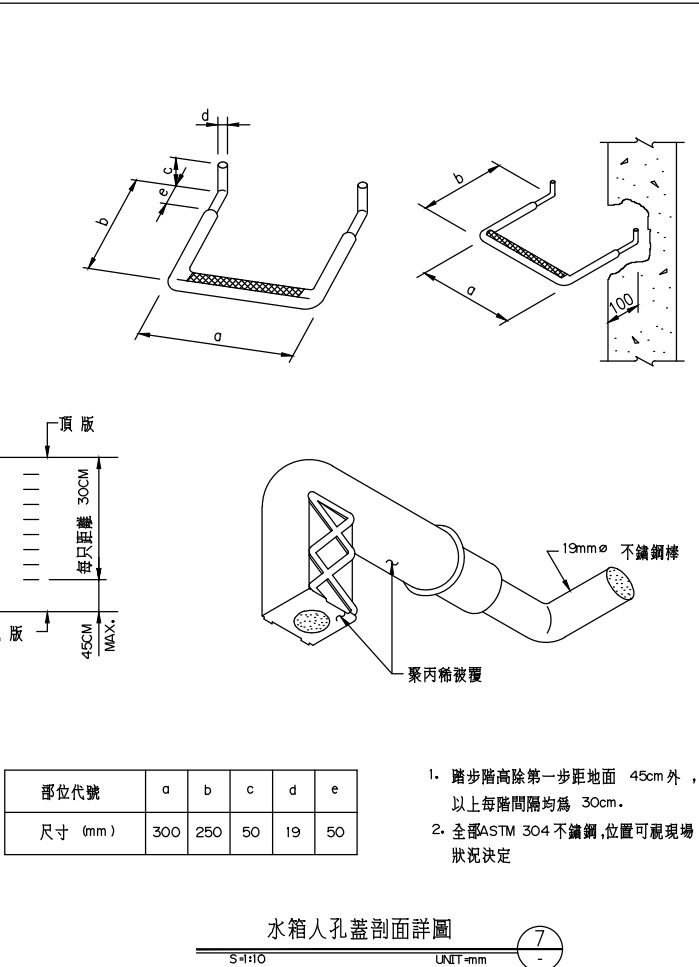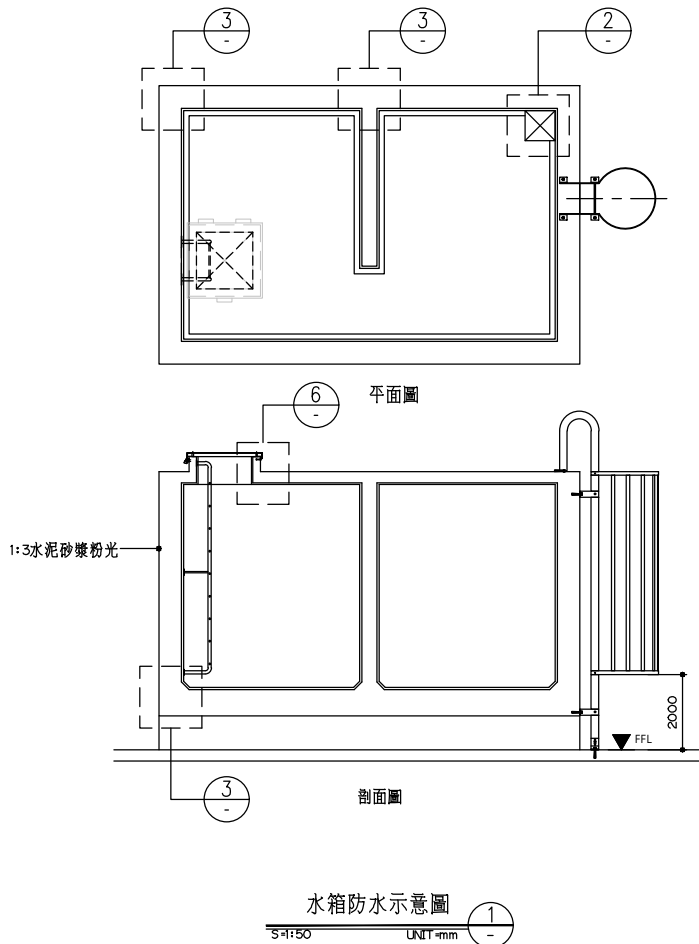

統一企業集團桃園U-PARK智匯產業園區

建築新建工程

U-PARK PROJECT

統流開發股份有限公司

UNI-PRESIDENT EXPRESS CORP. TAIPEI, TAIWAN, R.O.C.

陰井、排水溝、淺溝、水箱人孔詳圖(二)


華興聯合建築師事務所

HWA SHIN ARCHITECTS

DWG. NO.
0721B-ARB-D09004

ISSUE NO.

JOB NO.
0721B

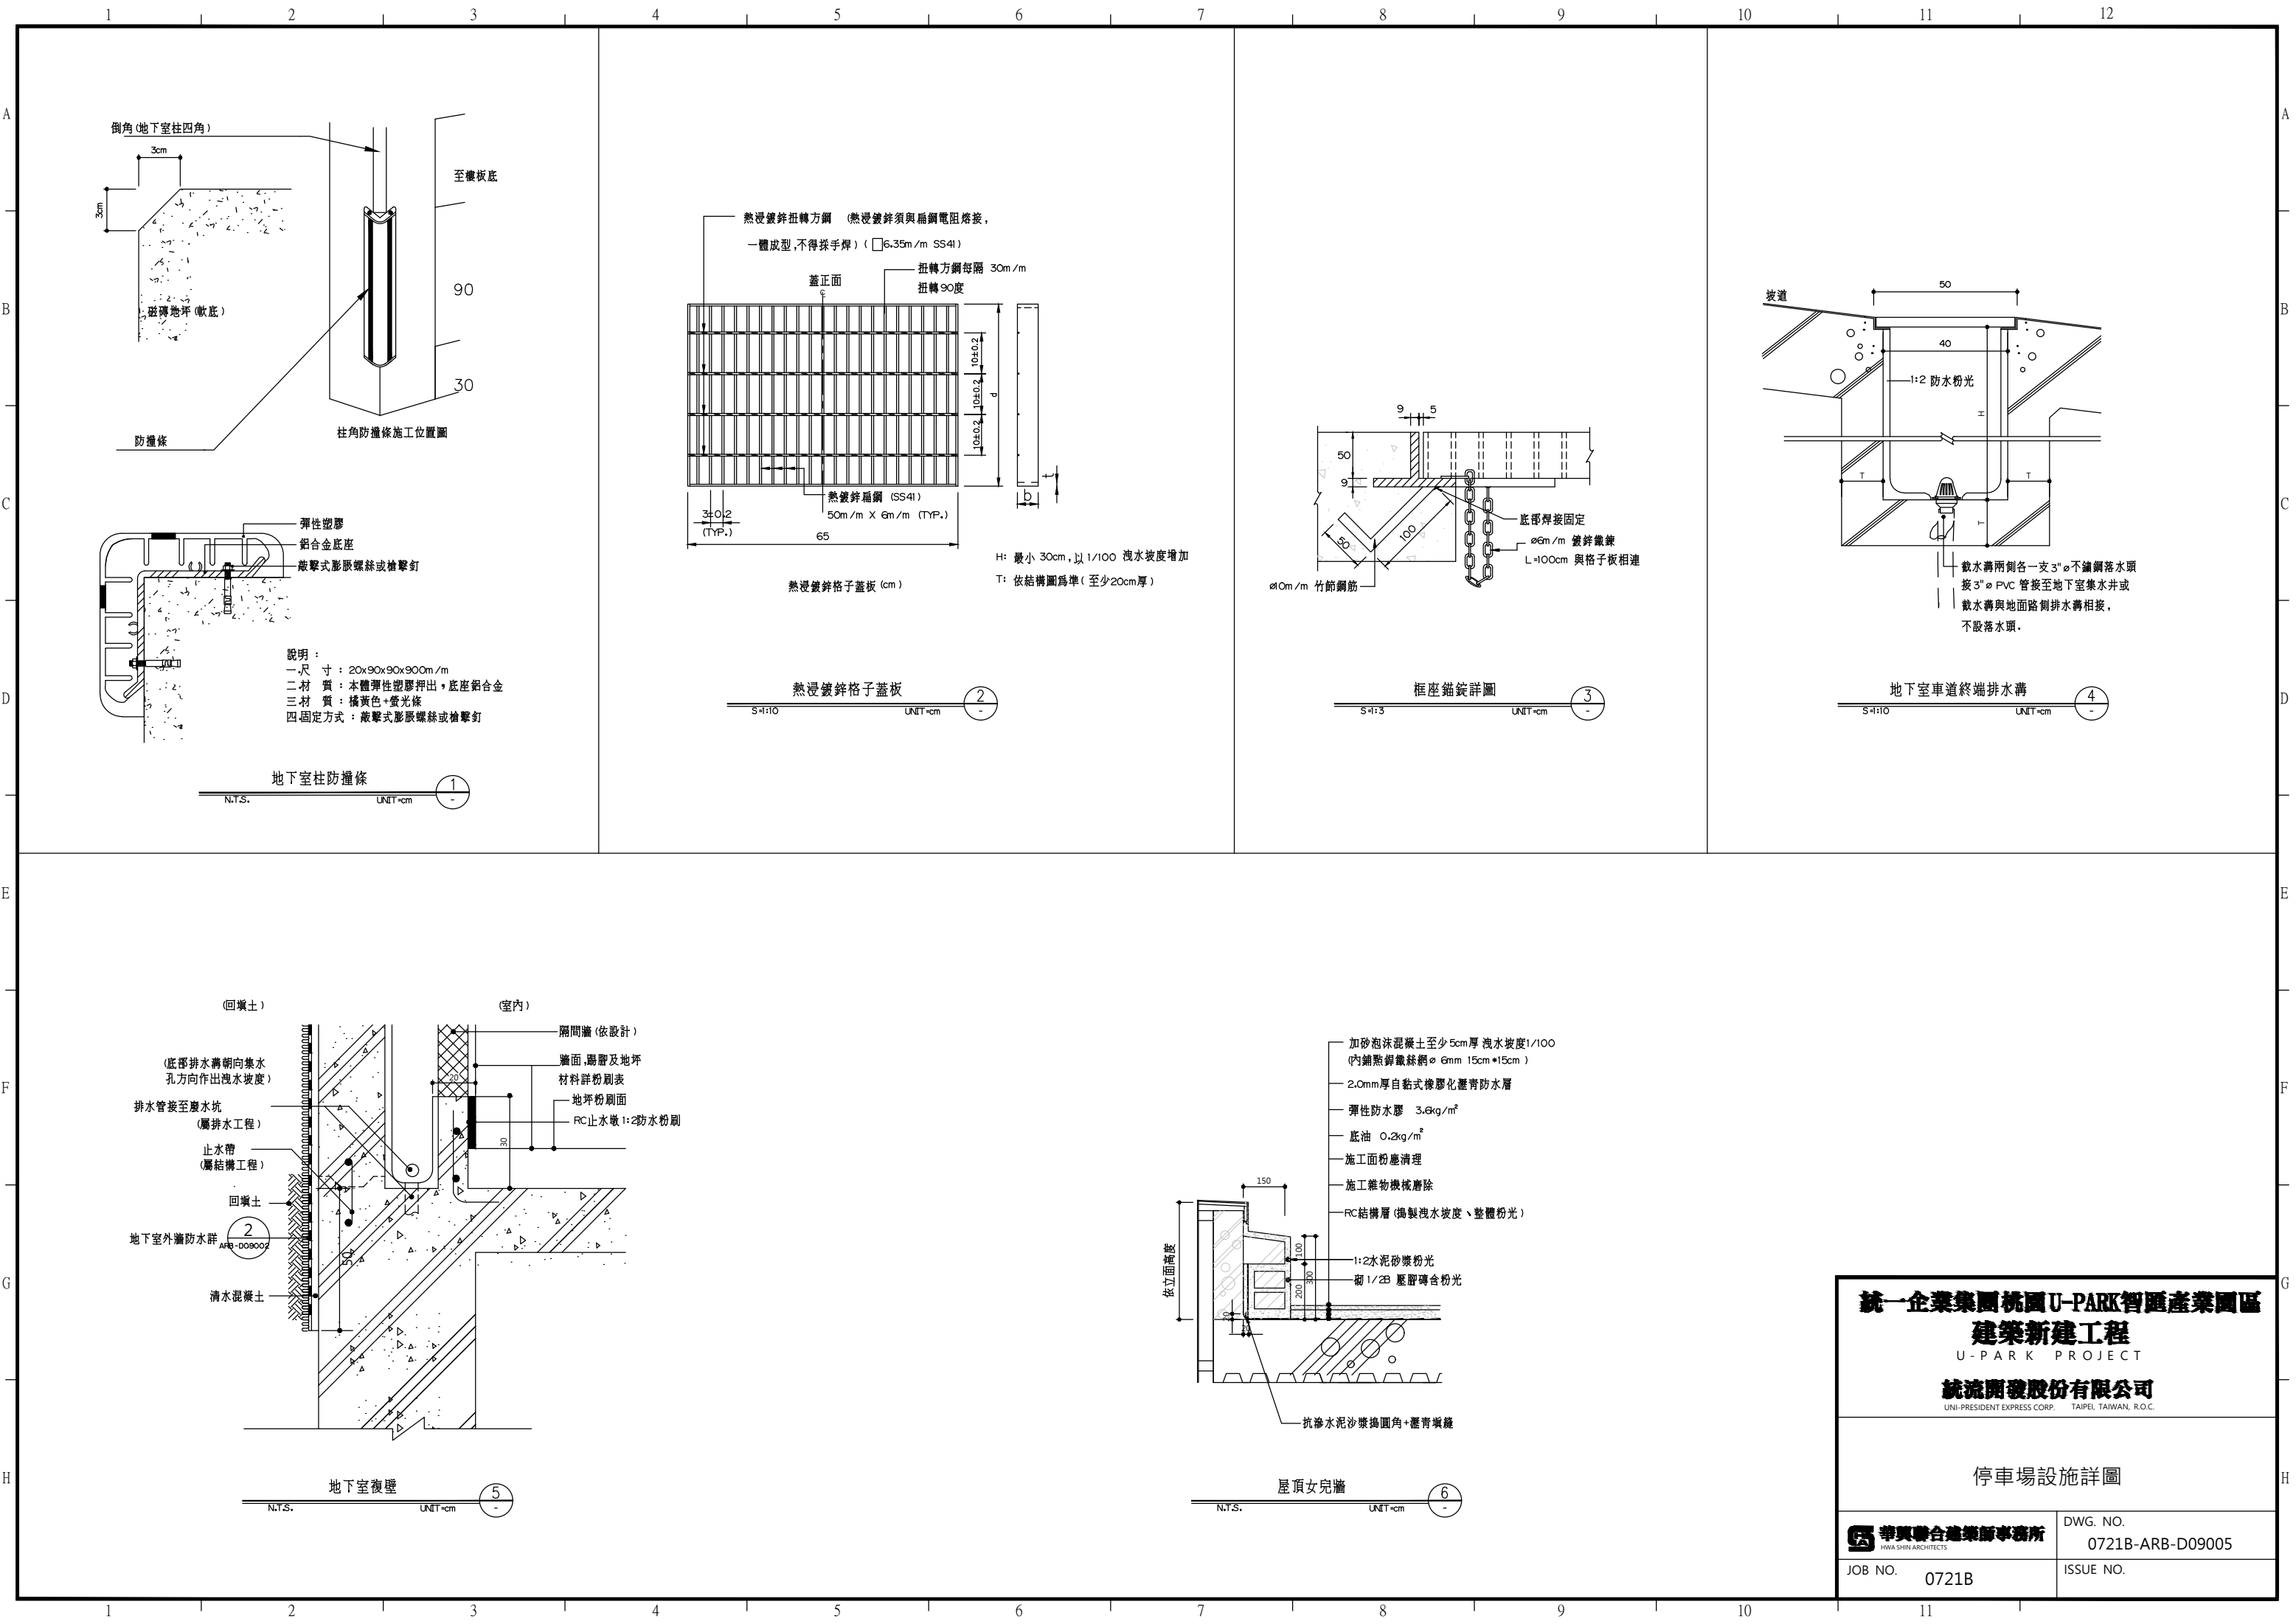



統一企業集團
桃園U-PARK智匯產業園區
建築新建工程
U-PARK PROJECT
統流開發股份有限公司
UNI-PRESIDENT EXPRESS CORP.
TAIPEI, TAIWAN, R.O.C.

停車場設施詳圖

華興聯合建築師事務所
HWA SHIN ARCHITECTS

DWG. NO. 0721B-ARB-D09005

JOB NO. 0721B
ISSUE NO.

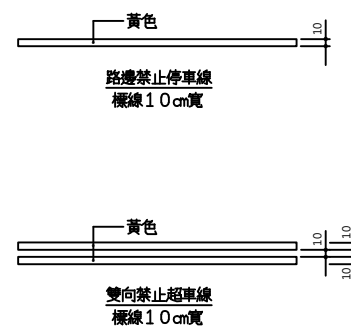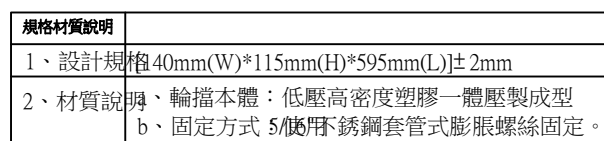

	白色熱拌聚醯標線
	黃色熱拌聚醯標線

1. 各停車位詳細尺寸由建築師指定。
2. 指向線用以指示車輛進行方向對於車道上本標線為白色箭頭其式樣依其指示目的規定如下：
 - 一、指示直行直線箭頭。
 - 二、指示轉彎弧形箭頭。
 - 三、指示直行與轉彎直線與弧形合併之分叉箭頭。
3. 本圖標線之製作，請依照交通部編印「道路交通標誌標線號誌設置規則」製作。

※行車方向指向線詳圖、停車位標線、路邊禁止停車線詳圖
(依據道路交通標誌、標線、號誌設置規則製作)



統一企業集團桃園U-PARK智匯產業園區
建築新建工程
U-PARK PROJECT
統流開發股份有限公司
UNI-PRESIDENT EXPRESS CORP., TAIPEI, TAIWAN, R.O.C.


防火被覆、門檻、車擋、停車標線詳圖

 **華興聯合建築師事務所**
HWA SHIN ARCHITECTS

JOB NO. 0721B

DWG. NO.	0721B-ARB-D09006
----------	------------------


ISSUE NO.	
-----------	--

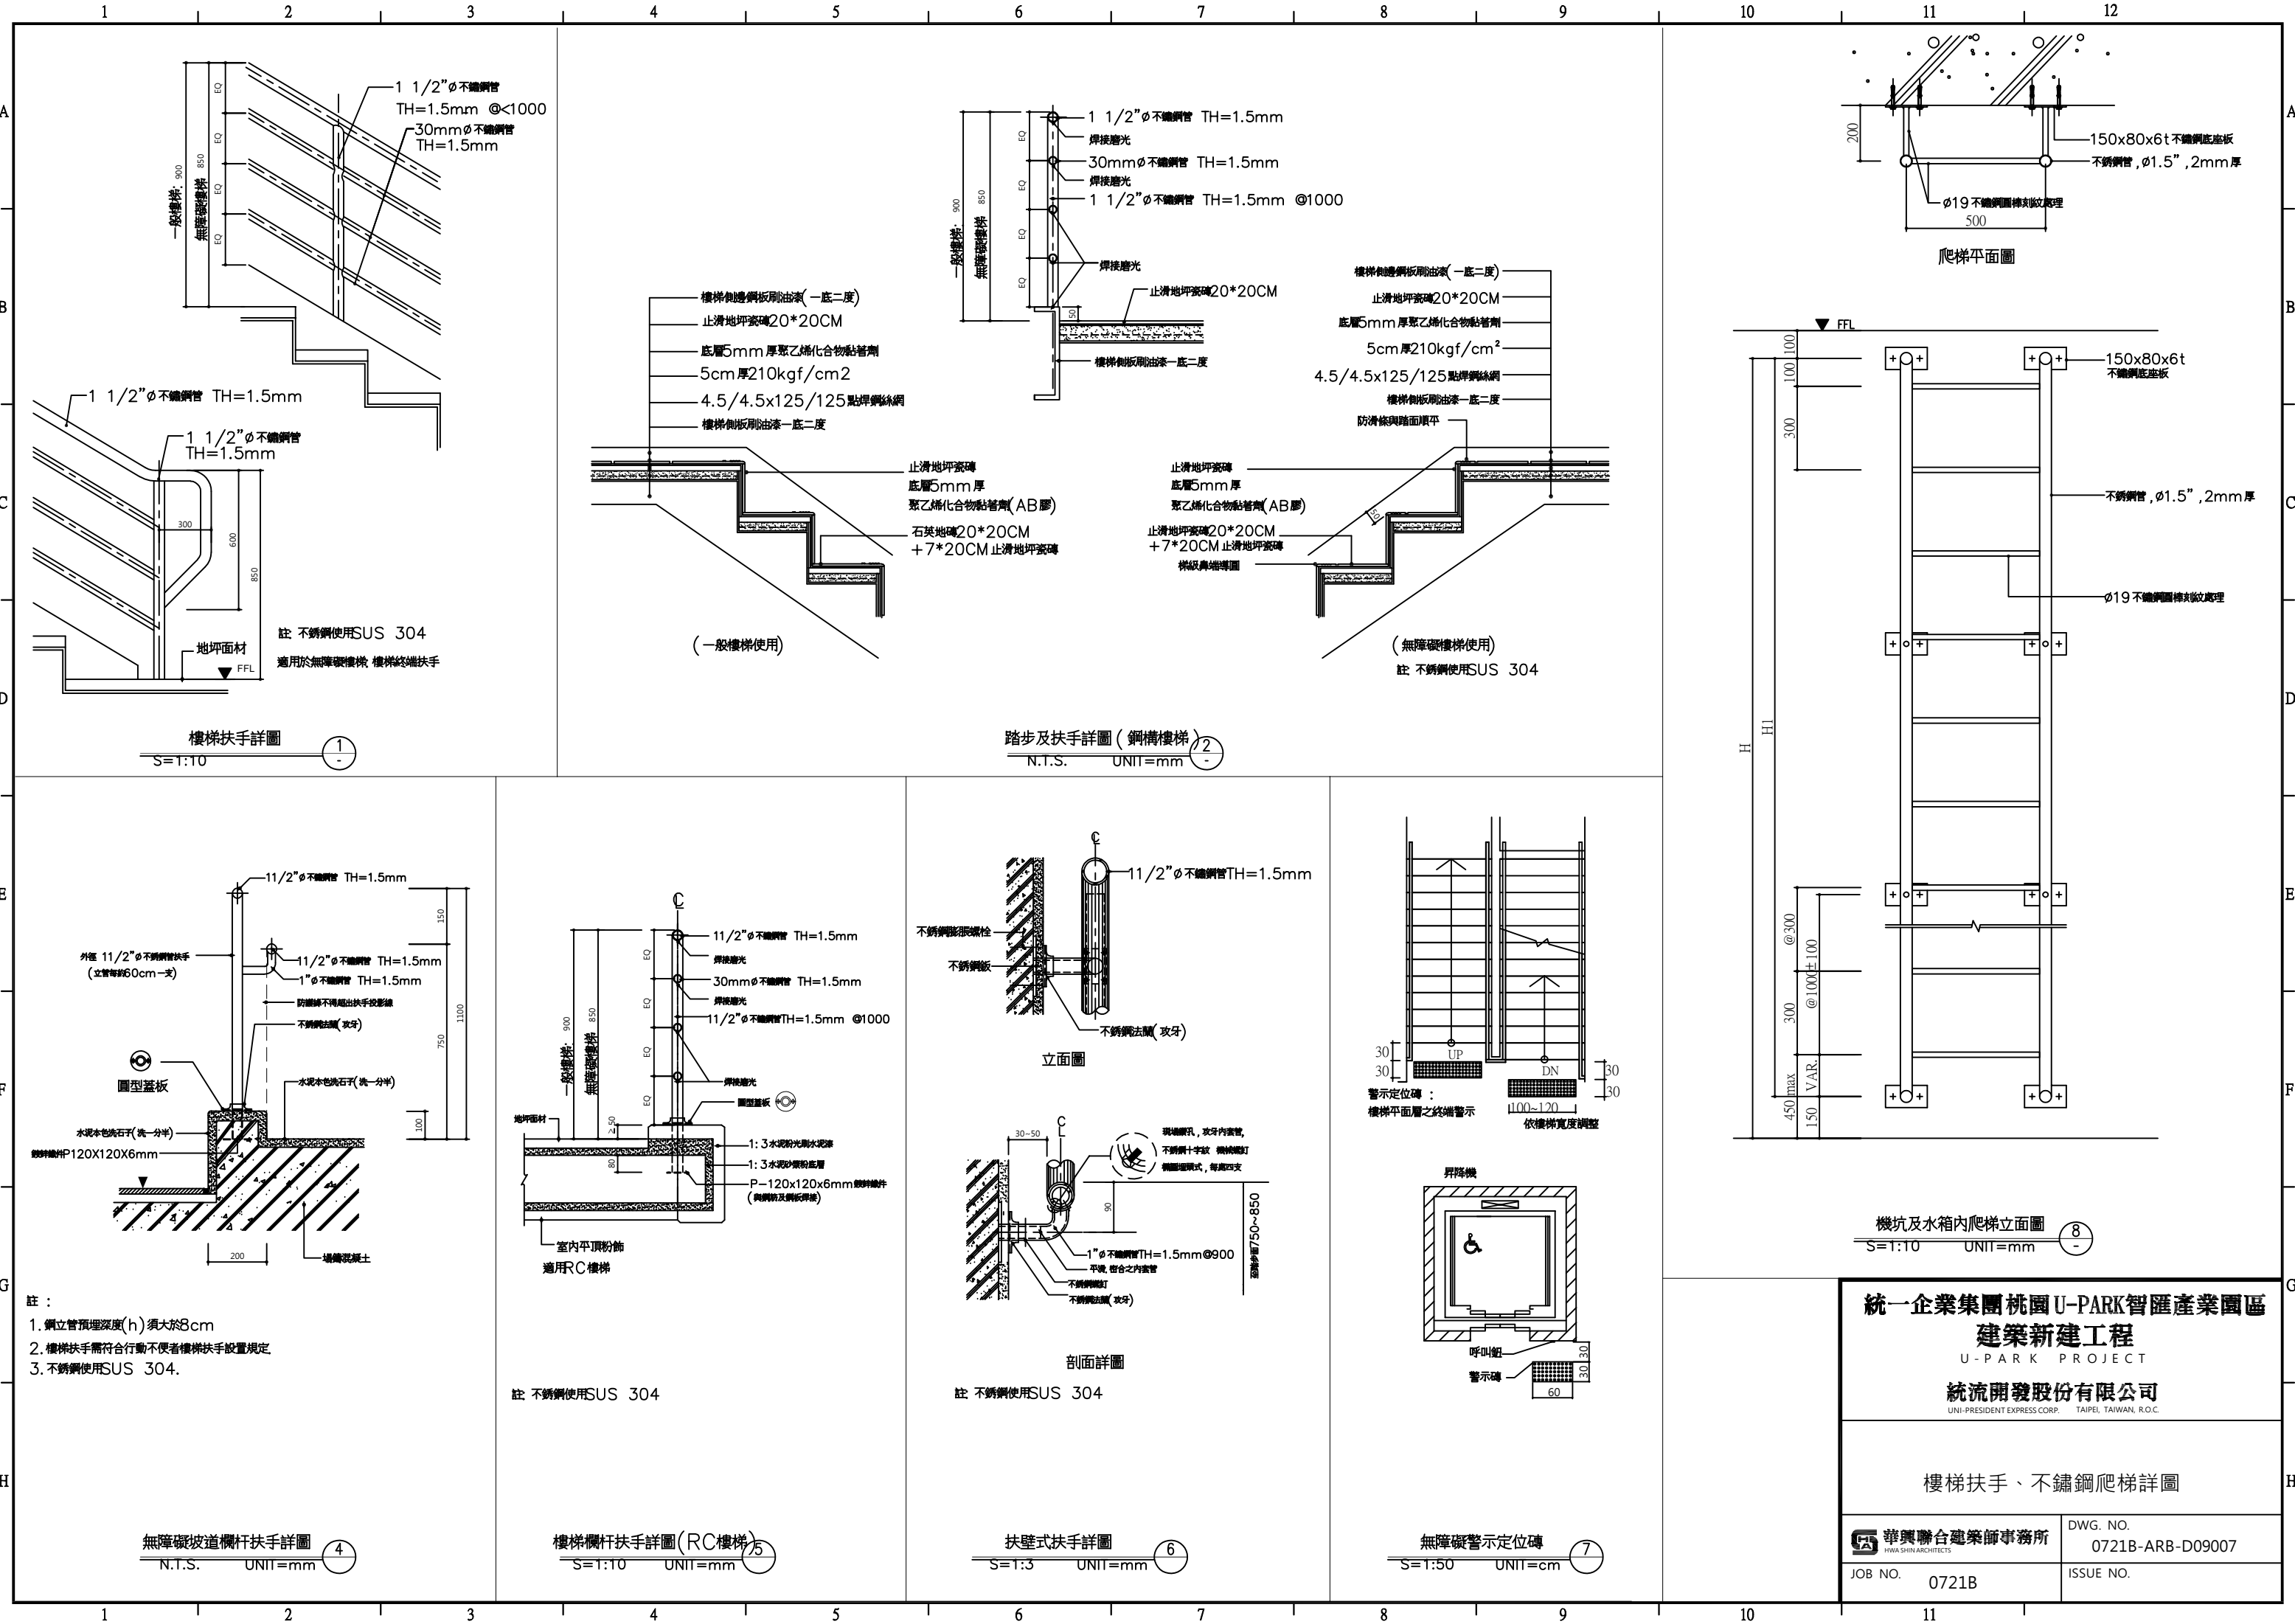

統一企業集團桃園U-PARK智匯產業園區
建築新建工程
U-PARK PROJECT
統流開發股份有限公司
UNI-PRESIDENT EXPRESS CORP. TAIPEI, TAIWAN, R.O.C.

樓梯扶手、不銹鋼爬梯詳圖

華興聯合建築師事務所 HWA SHIN ARCHITECTS	DWG. NO. 0721B-ARB-D09007
JOB NO. 0721B	ISSUE NO.

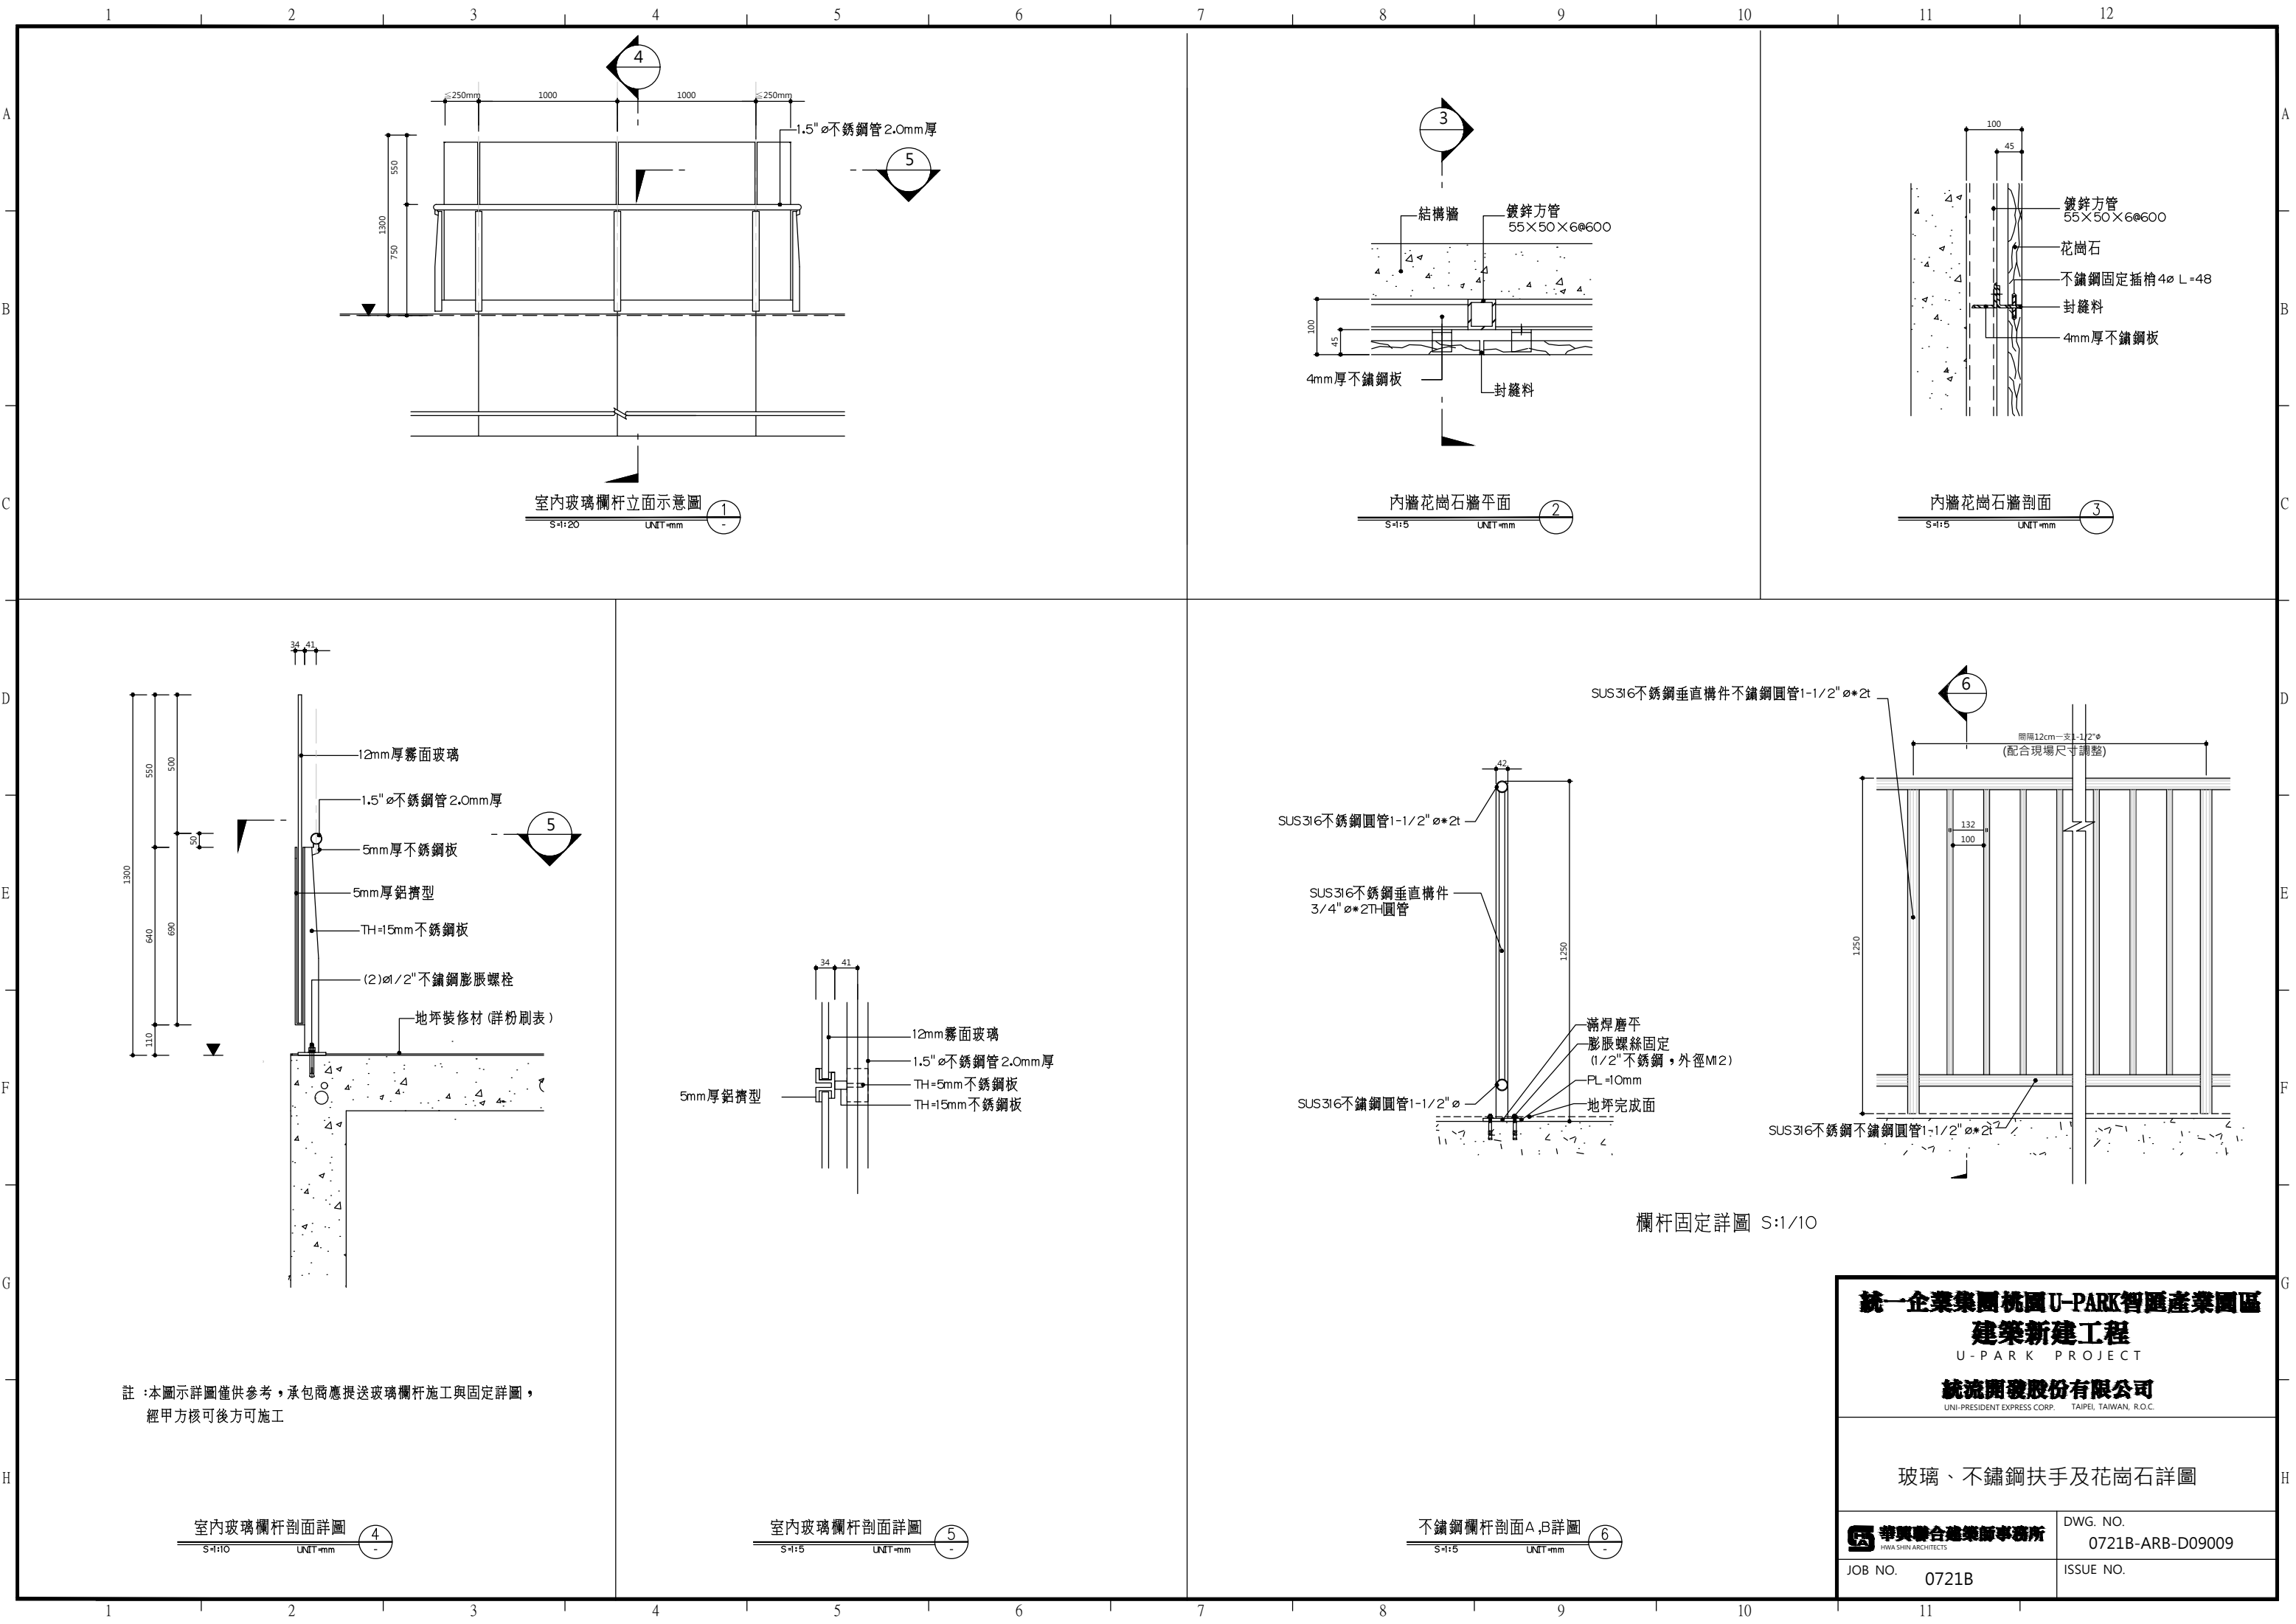

註：本圖示詳圖僅供參考，承包商應提送玻璃欄杆施工與固定詳圖，經甲方核可後方可施工

欄杆固定詳圖 S:1/10

統一企業集團桃園U-PARK智匯產業園區

建築新建工程

U-PARK PROJECT

統流開發股份有限公司

UNI-PRESIDENT EXPRESS CORP. TAIPEI, TAIWAN, R.O.C.

玻璃、不銹鋼扶手及花崗石詳圖

華興聯合建築師事務所

HWA SHIN ARCHITECTS


DWG. NO.
0721B-ARB-D09009

JOB NO.
0721B


ISSUE NO.

TYPE A1 乾式輕隔間 (一般空間)

N.T.S.	UNIT = mm	1
		-

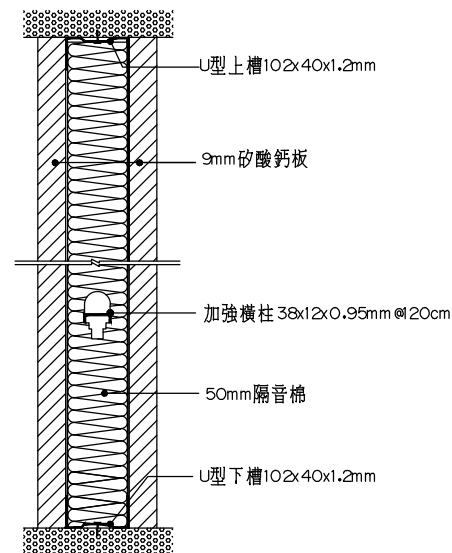


TYPE A2 乾式輕隔間 (一般空間) 2

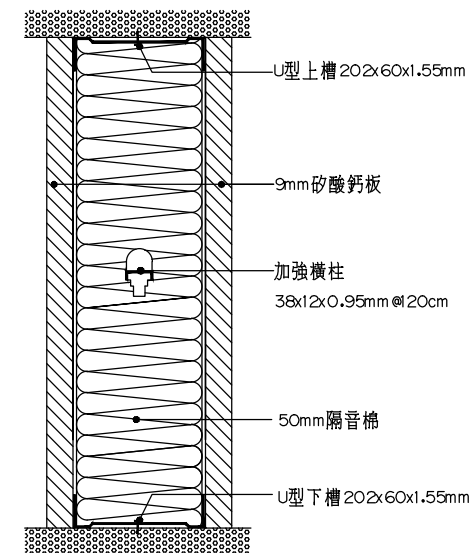


TYPE C 乾式輕隔間牆 (管道間)

N.T.S.	UNIT = mm	3
		-

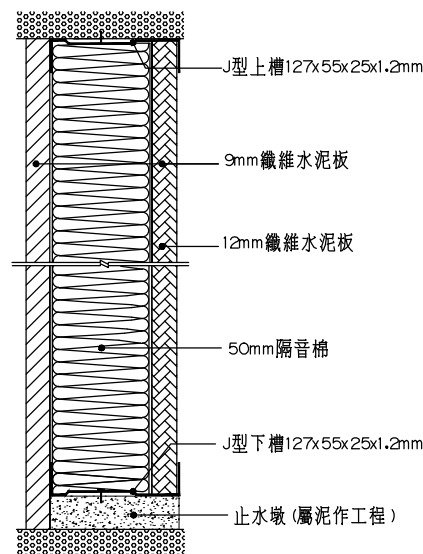


TYPE DI 乾式輕隔間(單面封板) 4

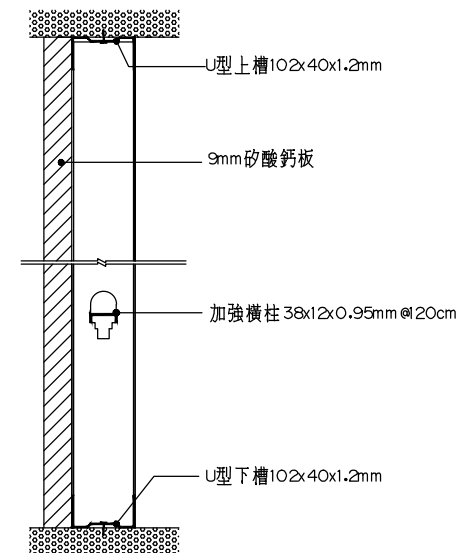

TYPE D2 乾式輕隔間 (單面封板)

N.T.S.	UNIT=mm	5
		-

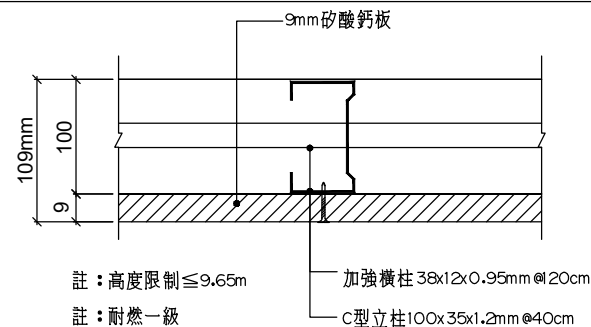

A、乾燥區域採 9mm (含以上) 矽酸鈣板：

材料符合CNS 13777表5中1.0FK規定，為維護產品耐久性，減少接觸有害風險。

應檢附環境部廢棄物再利用情形資料，原廠切結保證產品無購入添加非經許可再利用廢棄物及未經燒結底渣汙泥（蠟紙汙泥及石材汙泥）。本工程材料不得採用原產地為大陸地區板材，其相關性能要求如下：

1.防火隔音性：CNS 14705-1耐火一級（另須檢附原廠逐批自主檢驗設備證明及檢測報告）。及主管機關認證防火證明。依圖說隔音需求提供最小系統隔音性能 R_w (TAF或主管機關認證)。

2.提供不含石綿；甲酉基及TVOC符合未檢出(依綠建材公開資訊資料)。
材料通過環境部環保標章綠建材認證。


3.矽酸鈣板防潮性需符合CNS相關測試通過1365天吸水耐剝離或耐水性測試達無剝離標準。

4.矽酸鈣板耐久性需符合CNS耐候或老化相關測試達1365天符合無龜裂剝離標準。

5.政策性：配合政府政策原廠應提供產品經台灣當地EPD認證證明及經盤查碳足跡資料，

依行政院2030年再生能源政策目標，原廠應採30%以上再生能源與電力及瓦斯等總能源佔比(證明文件)。

統一企業集團桃園U-PARK智匯產業園區 建築新建工程 U - P A R K P R O J E C T 統一流開發股份有限公司 UNI-PRESIDENT EXPRESS CORP. TAIPEI, TAIWAN, R.O.C.	
輕隔間詳圖(一)	
 華興聯合建築師事務所 HWA SHIN ARCHITECTS	DWG. NO. 0721B-ARB-D09010
JOB NO. 0721B	ISSUE NO.

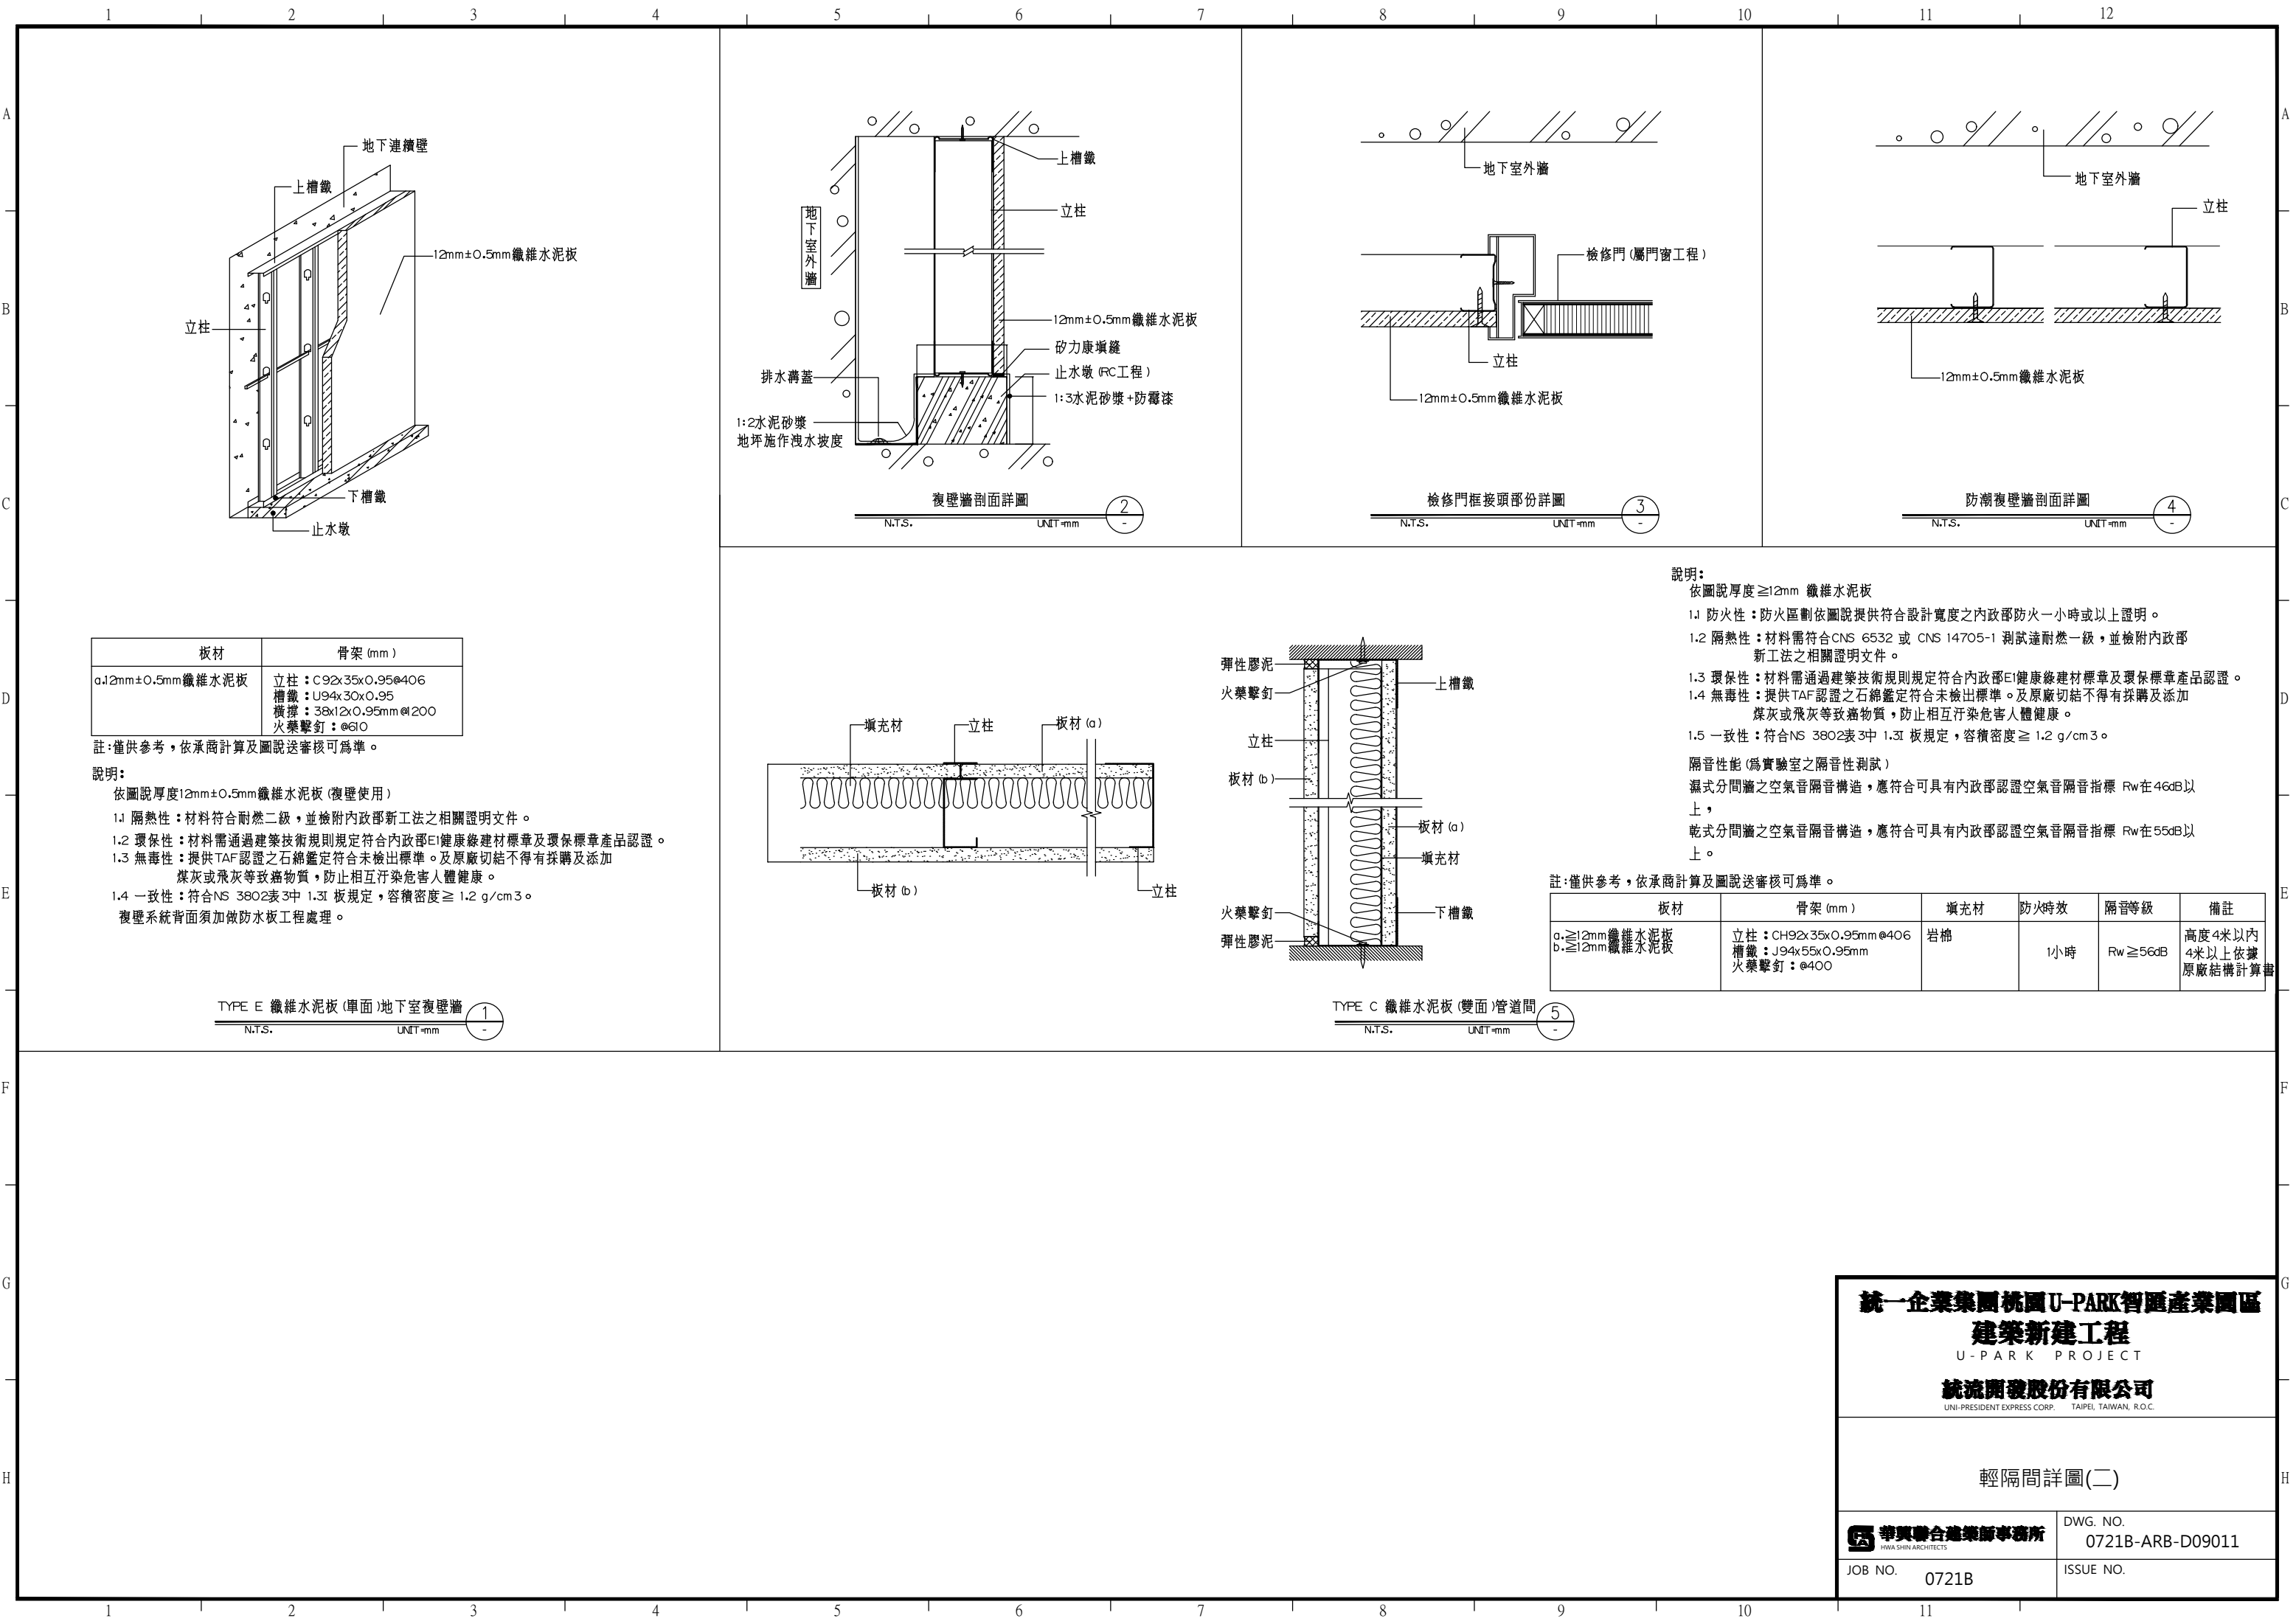

板材	骨架 (mm)
a.12mm±0.5mm纖維水泥板	立柱：C92x35x0.95@406 槽鐵：U94x30x0.95 橫撐：38x12x0.95mm@200 火藥擊釘：@610

註:僅供參考，依承商計算及圖說送審核可為準。

說明:






依圖說厚度12mm±0.5mm纖維水泥板 (復壁使用)

- 1.1 隔熱性：材料符合耐燃二級，並檢附內政部新工法之相關證明文件。
 - 1.2 環保性：材料需通過建築技術規則規定符合內政部E1健康綠建材標章及環保標章產品認證。
 - 1.3 無毒性：提供TAF認證之石棉鑑定符合未檢出標準。及原廠切結不得有採購及添加 煤灰或飛灰等致癌物質，防止相互汙染危害人體健康。
 - 1.4 一致性：符合NS 3802表3中 1.3I 板規定，容積密度 $\geq 1.2\text{ g/cm}^3$ 。
- 復壁系統背面須加做防水板工程處理。

TYPE E 纖維水泥板 (單面)地下室復壁牆

N.T.S. UNIT:mm

1

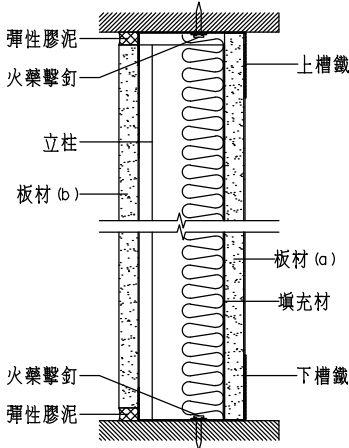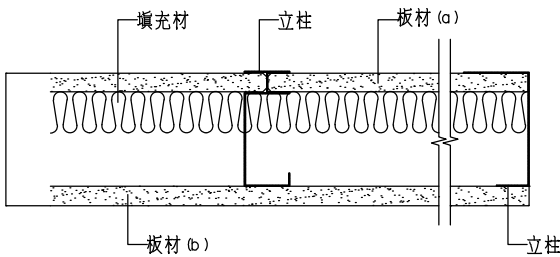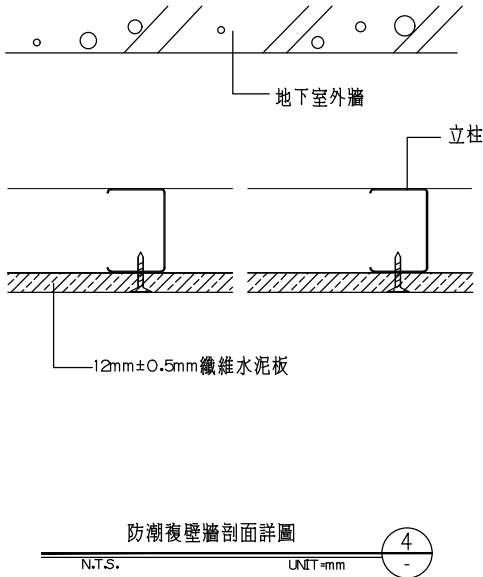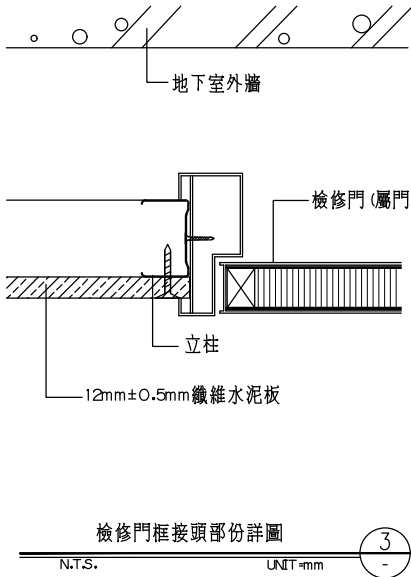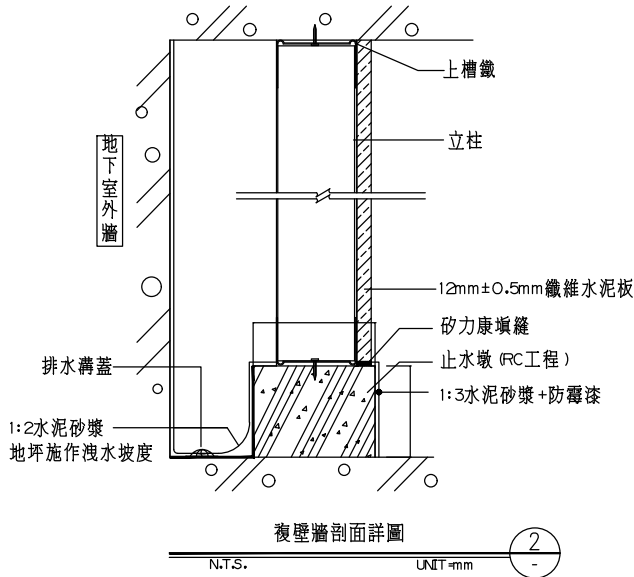

TYPE C 纖維水泥板 (雙面)管道間

N.T.S. UNIT:mm

5

說明:

依圖說厚度 $\geq 12\text{mm}$ 纖維水泥板

- 1.1 防火性：防火區劃依圖說提供符合設計寬度之內政部防火一小時或以上證明。
- 1.2 隔熱性：材料需符合CNS 6532 或 CNS 14705-1 測試達耐燃一級，並檢附內政部新工法之相關證明文件。
- 1.3 環保性：材料需通過建築技術規則規定符合內政部E1健康綠建材標章及環保標章產品認證。
- 1.4 無毒性：提供TAF認證之石棉鑑定符合未檢出標準。及原廠切結不得有採購及添加 煤灰或飛灰等致癌物質，防止相互汙染危害人體健康。
- 1.5 一致性：符合NS 3802表3中 1.3I 板規定，容積密度 $\geq 1.2\text{ g/cm}^3$ 。

隔音性能 (為實驗室之隔音性測試)

濕式分間牆之空氣音隔音構造，應符合可具有內政部認證空氣音隔音指標 R_w 在46dB以上，

乾式分間牆之空氣音隔音構造，應符合可具有內政部認證空氣音隔音指標 R_w 在55dB以上。

註:僅供參考，依承商計算及圖說送審核可為準。

板材	骨架 (mm)	填充材	防火時效	隔音等級	備註
a. $\geq 12\text{mm}$ 纖維水泥板 b. $\geq 12\text{mm}$ 纖維水泥板	立柱：CH92x35x0.95mm@406 槽鐵：J94x55x0.95mm 火藥擊釘：@400	岩棉	1小時	$R_w \geq 56\text{dB}$	高度4米以內 4米以上依據 原廠結構計算書

統一企業集團桃園U-PARK智匯產業園區

建築新建工程

U-PARK PROJECT

統流開發股份有限公司

UNI-PRESIDENT EXPRESS CORP. TAIPEI, TAIWAN, R.O.C.


輕隔間詳圖(二)

華興聯合建築師事務所
HWA SHIN ARCHITECTS

DWG. NO.
0721B-ARB-D09011

JOB NO.
0721B

ISSUE NO.

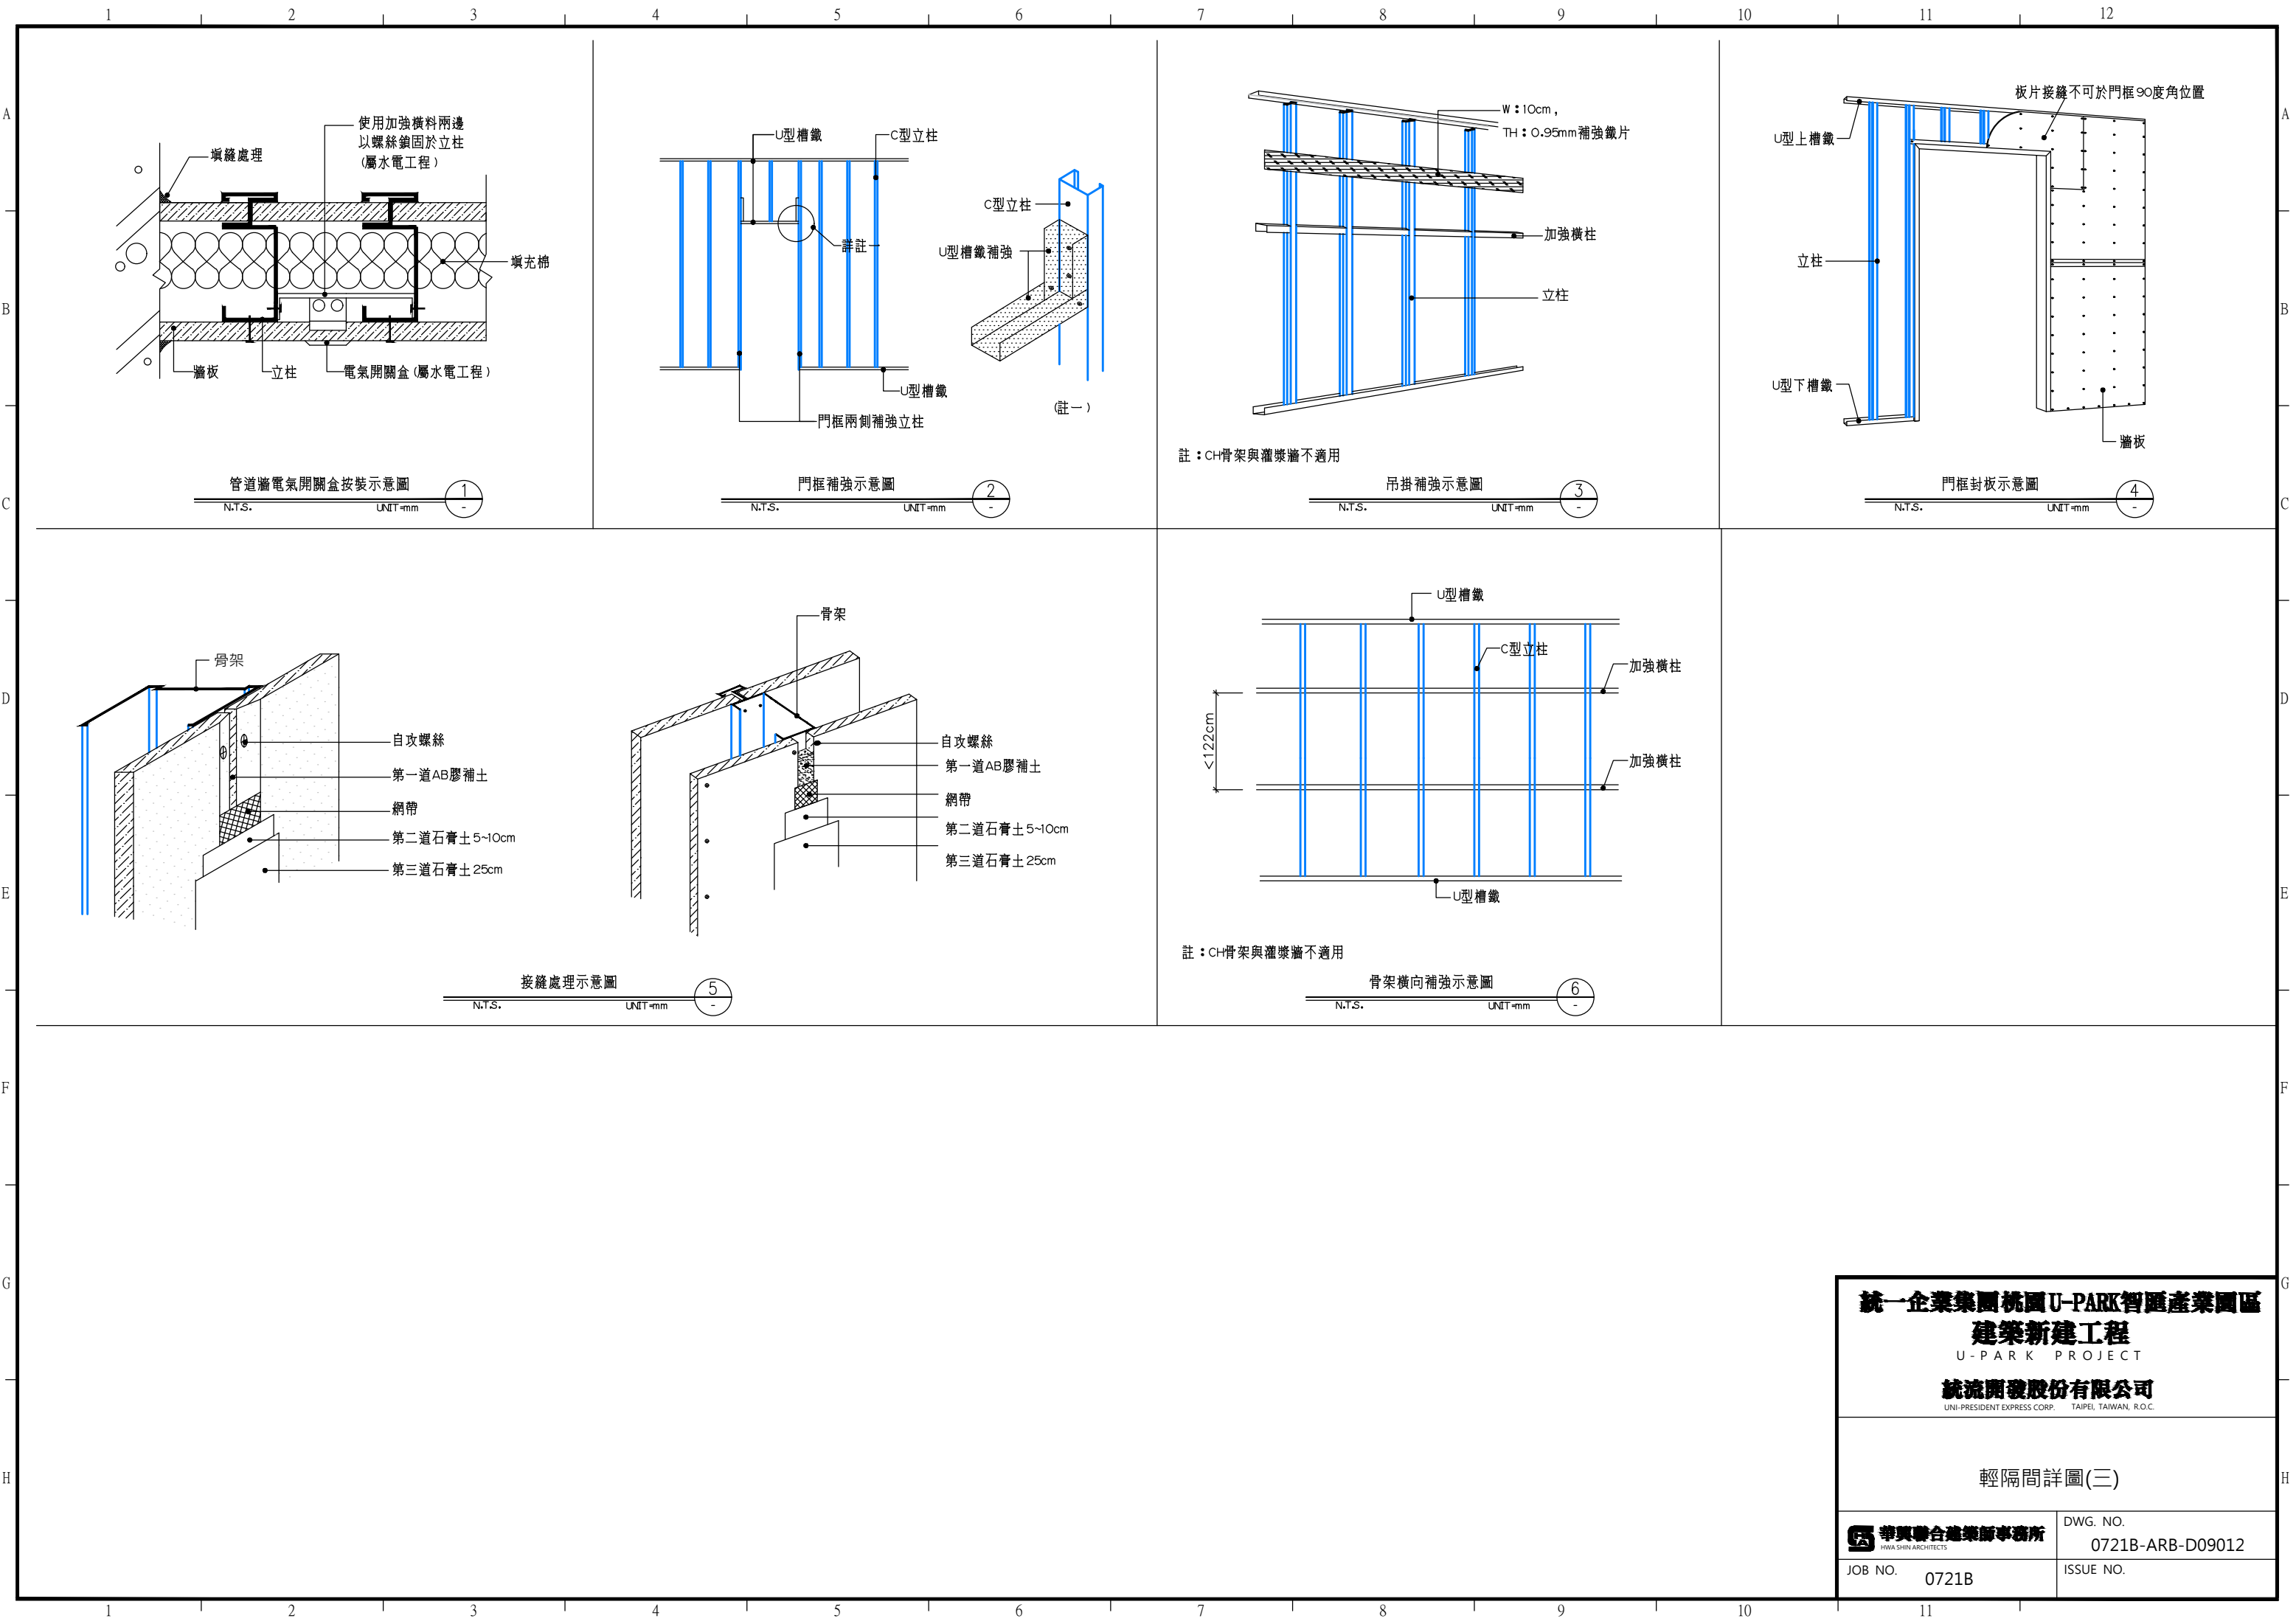

統一企業集團桃園U-PARK智匯產業園區

建築新建工程

U-PARK PROJECT

統流開發股份有限公司

UNI-PRESIDENT EXPRESS CORP. TAIPEI, TAIWAN, R.O.C.

輕隔間詳圖(三)


華興聯合建築師事務所

HWA SHIN ARCHITECTS

DWG. NO.
0721B-ARB-D09012

JOB NO.
0721B

ISSUE NO.

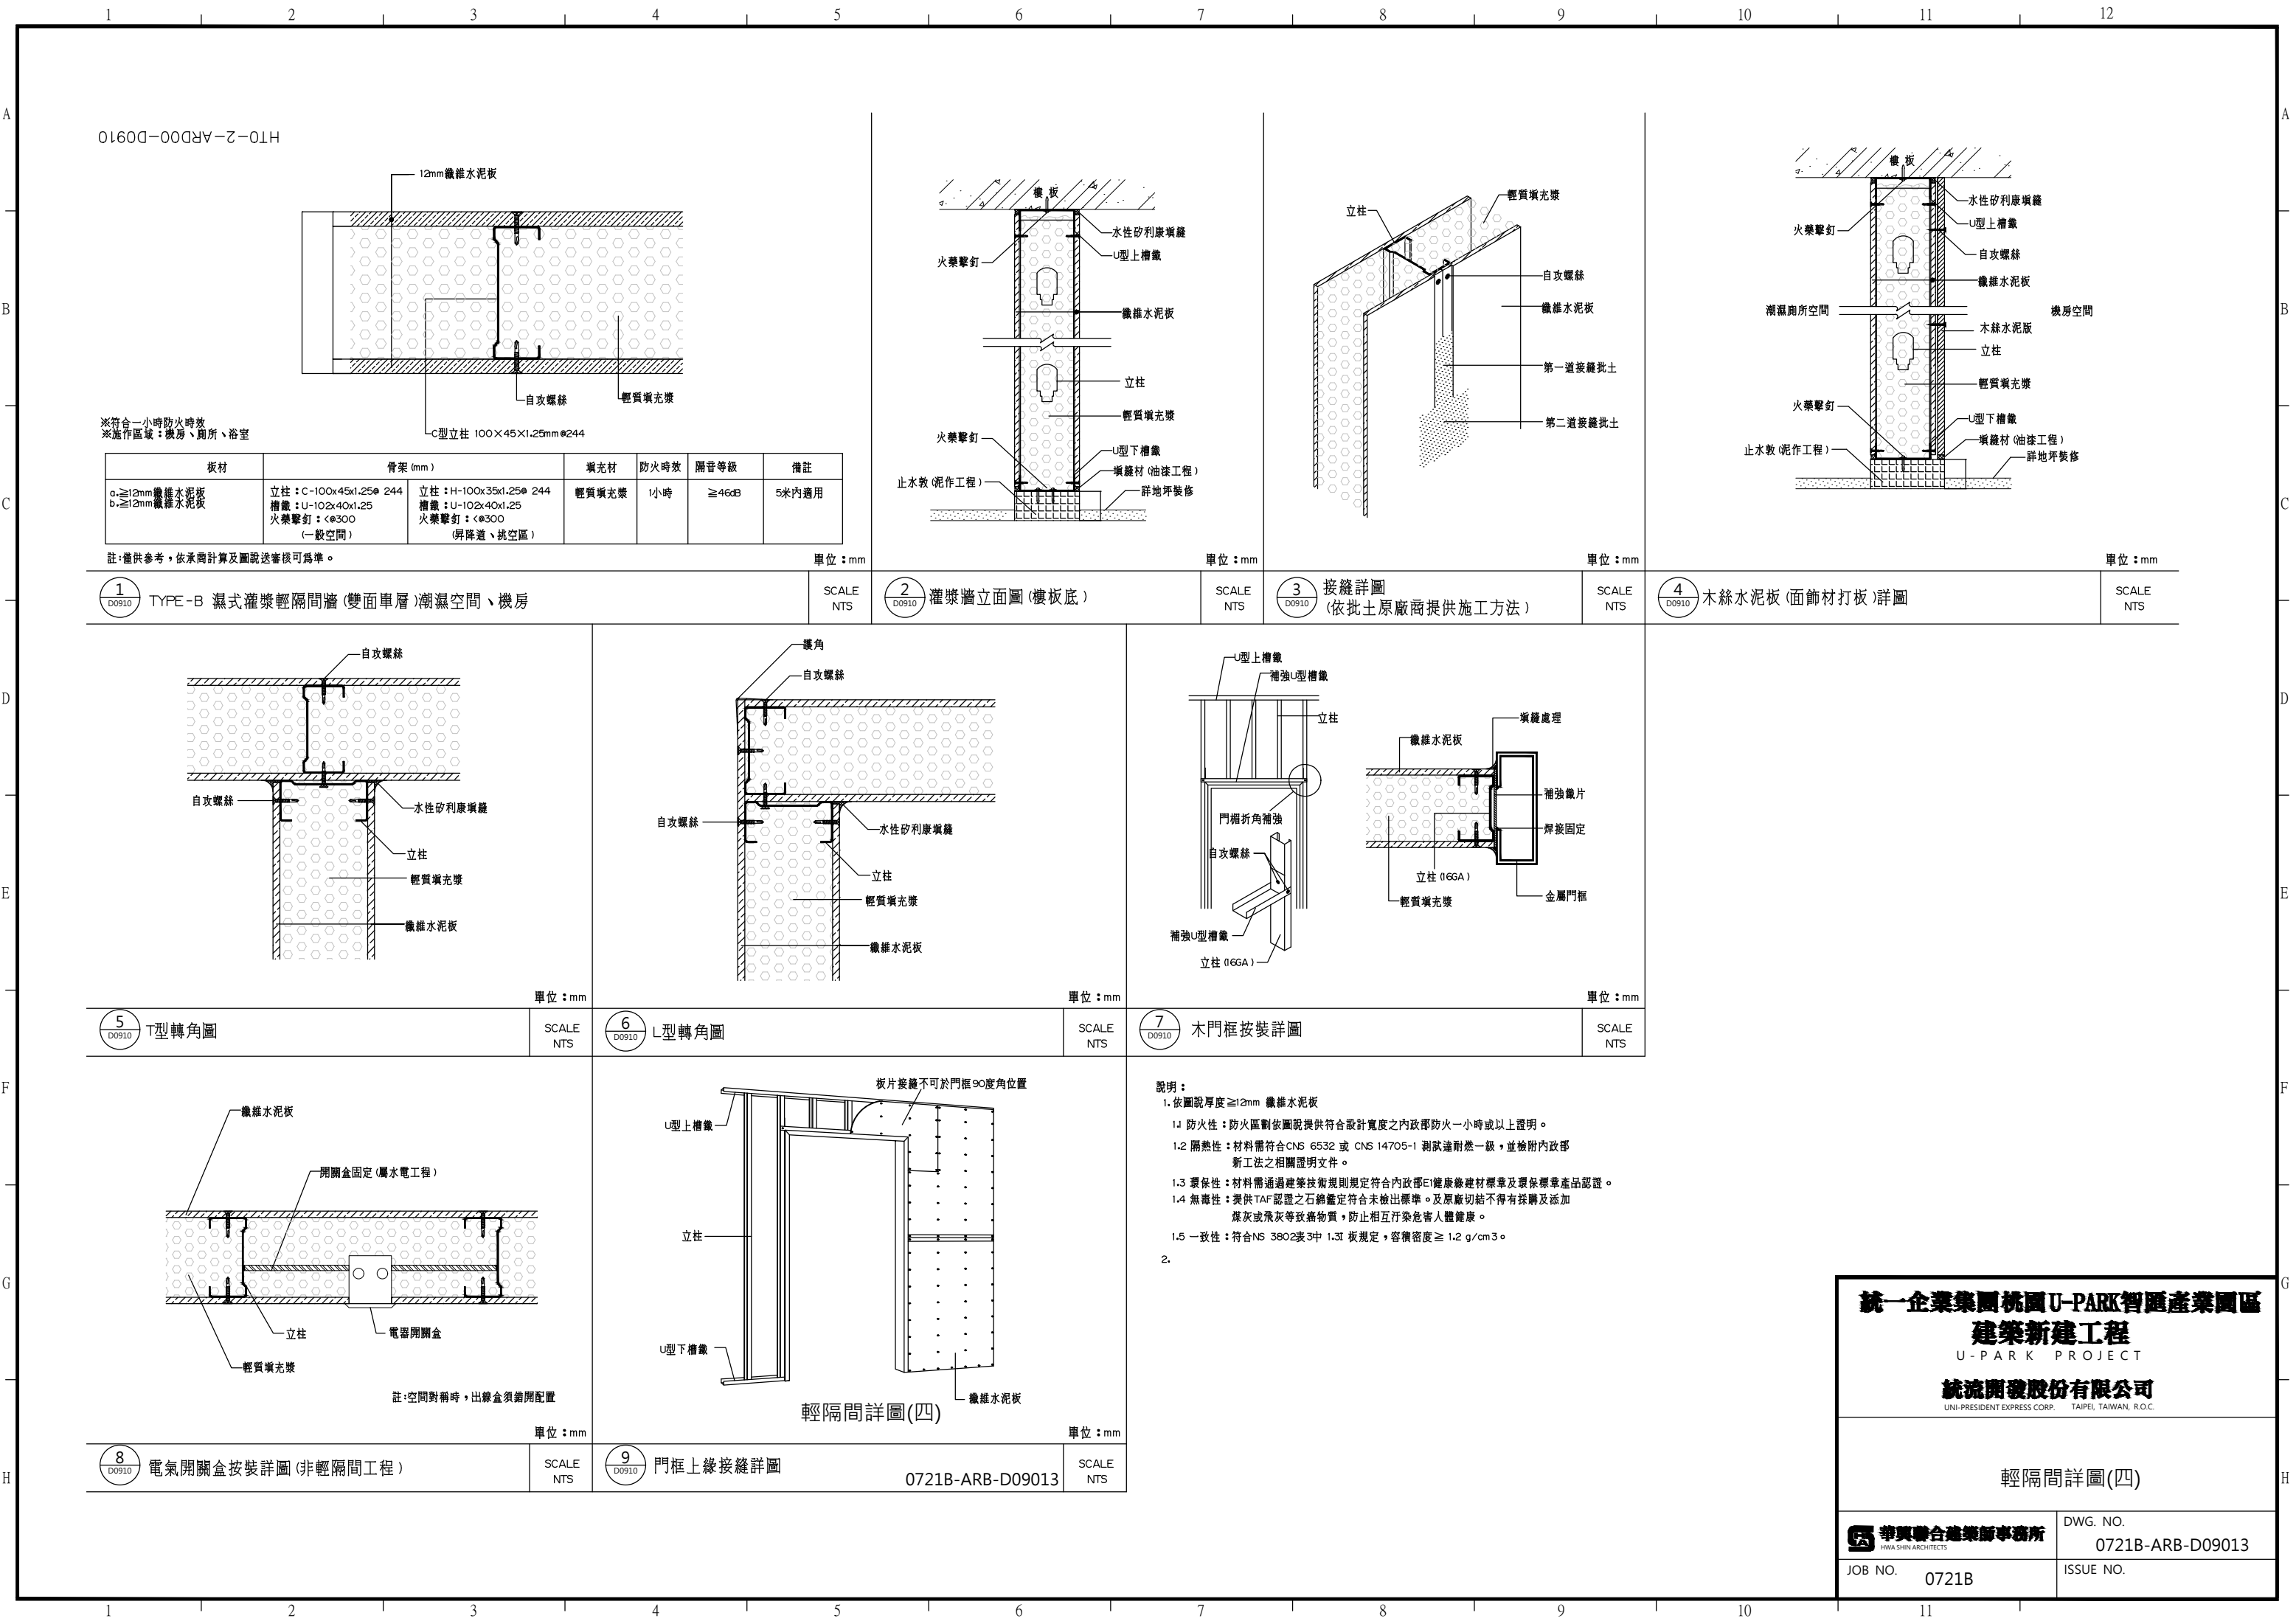

統一企業集團桃園U-PARK智匯產業園區

建築新建工程

U-PARK PROJECT

統流開發股份有限公司

UNI-PRESIDENT EXPRESS CORP. TAIPEI, TAIWAN, R.O.C.

輕隔間詳圖(四)


華興聯合建築師事務所


HWA SHIN ARCHITECTS

DWG. NO.
0721B-ARB-D09013

JOB NO.
0721B

ISSUE NO.

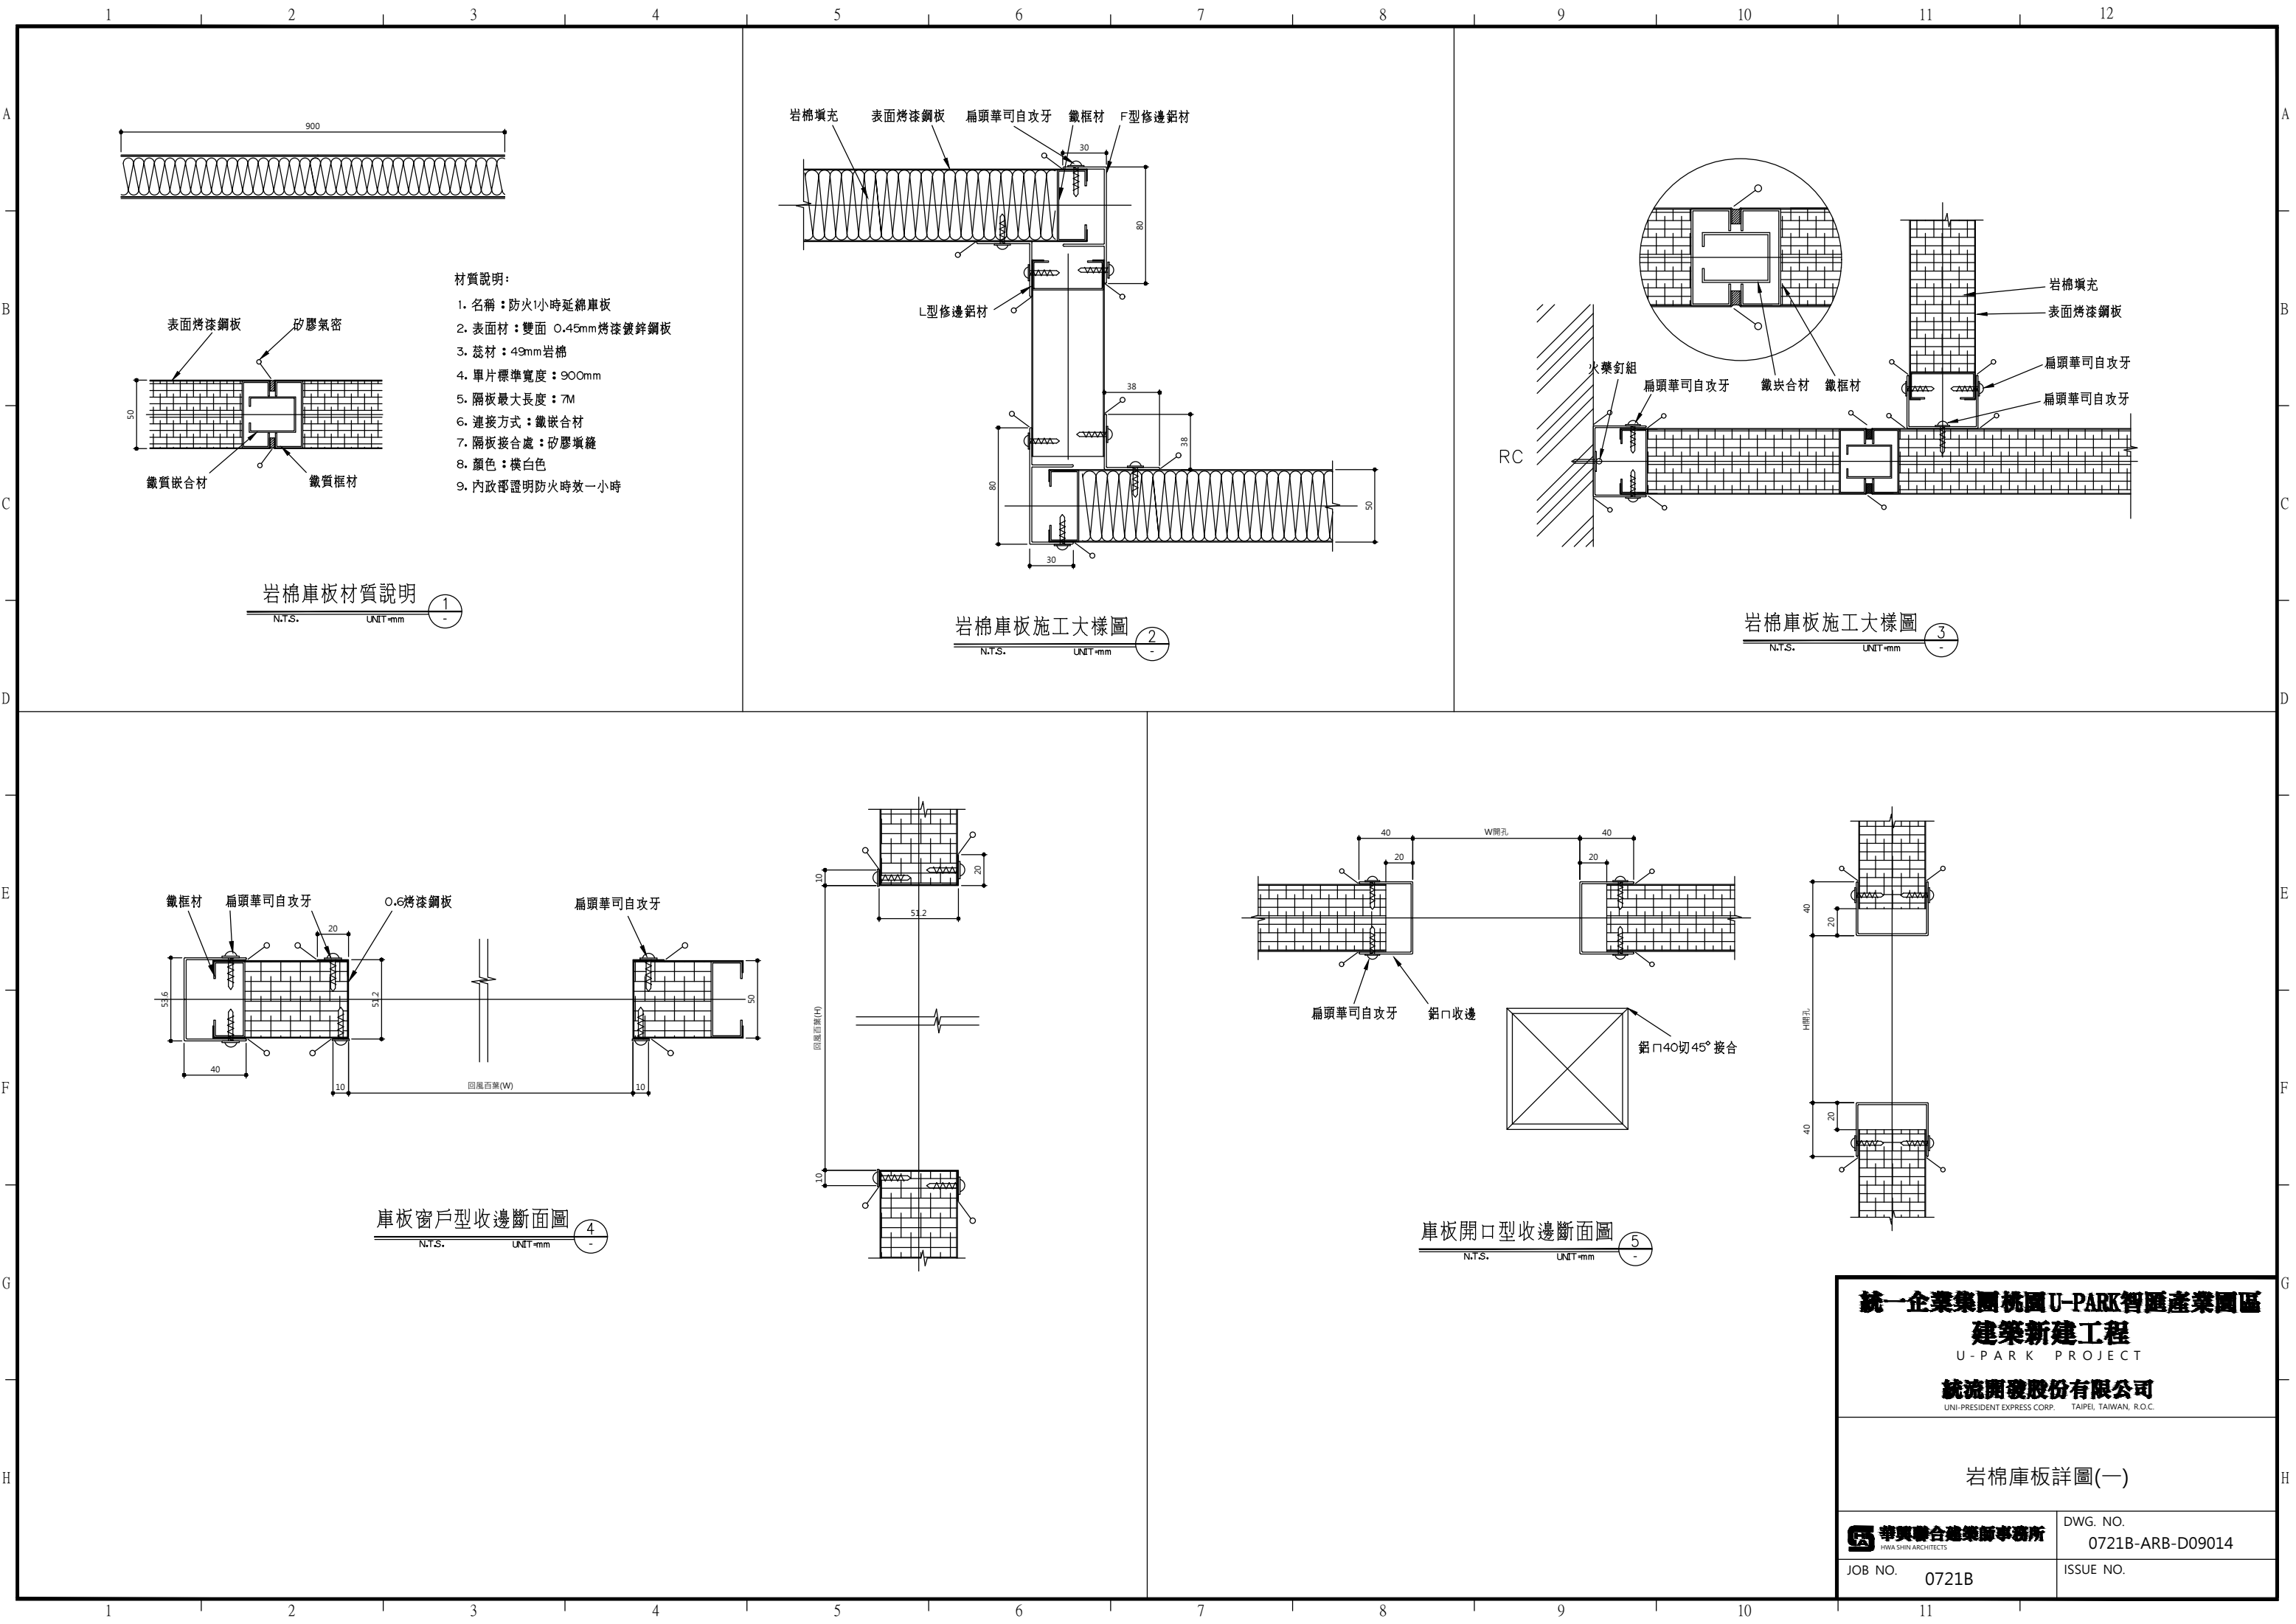

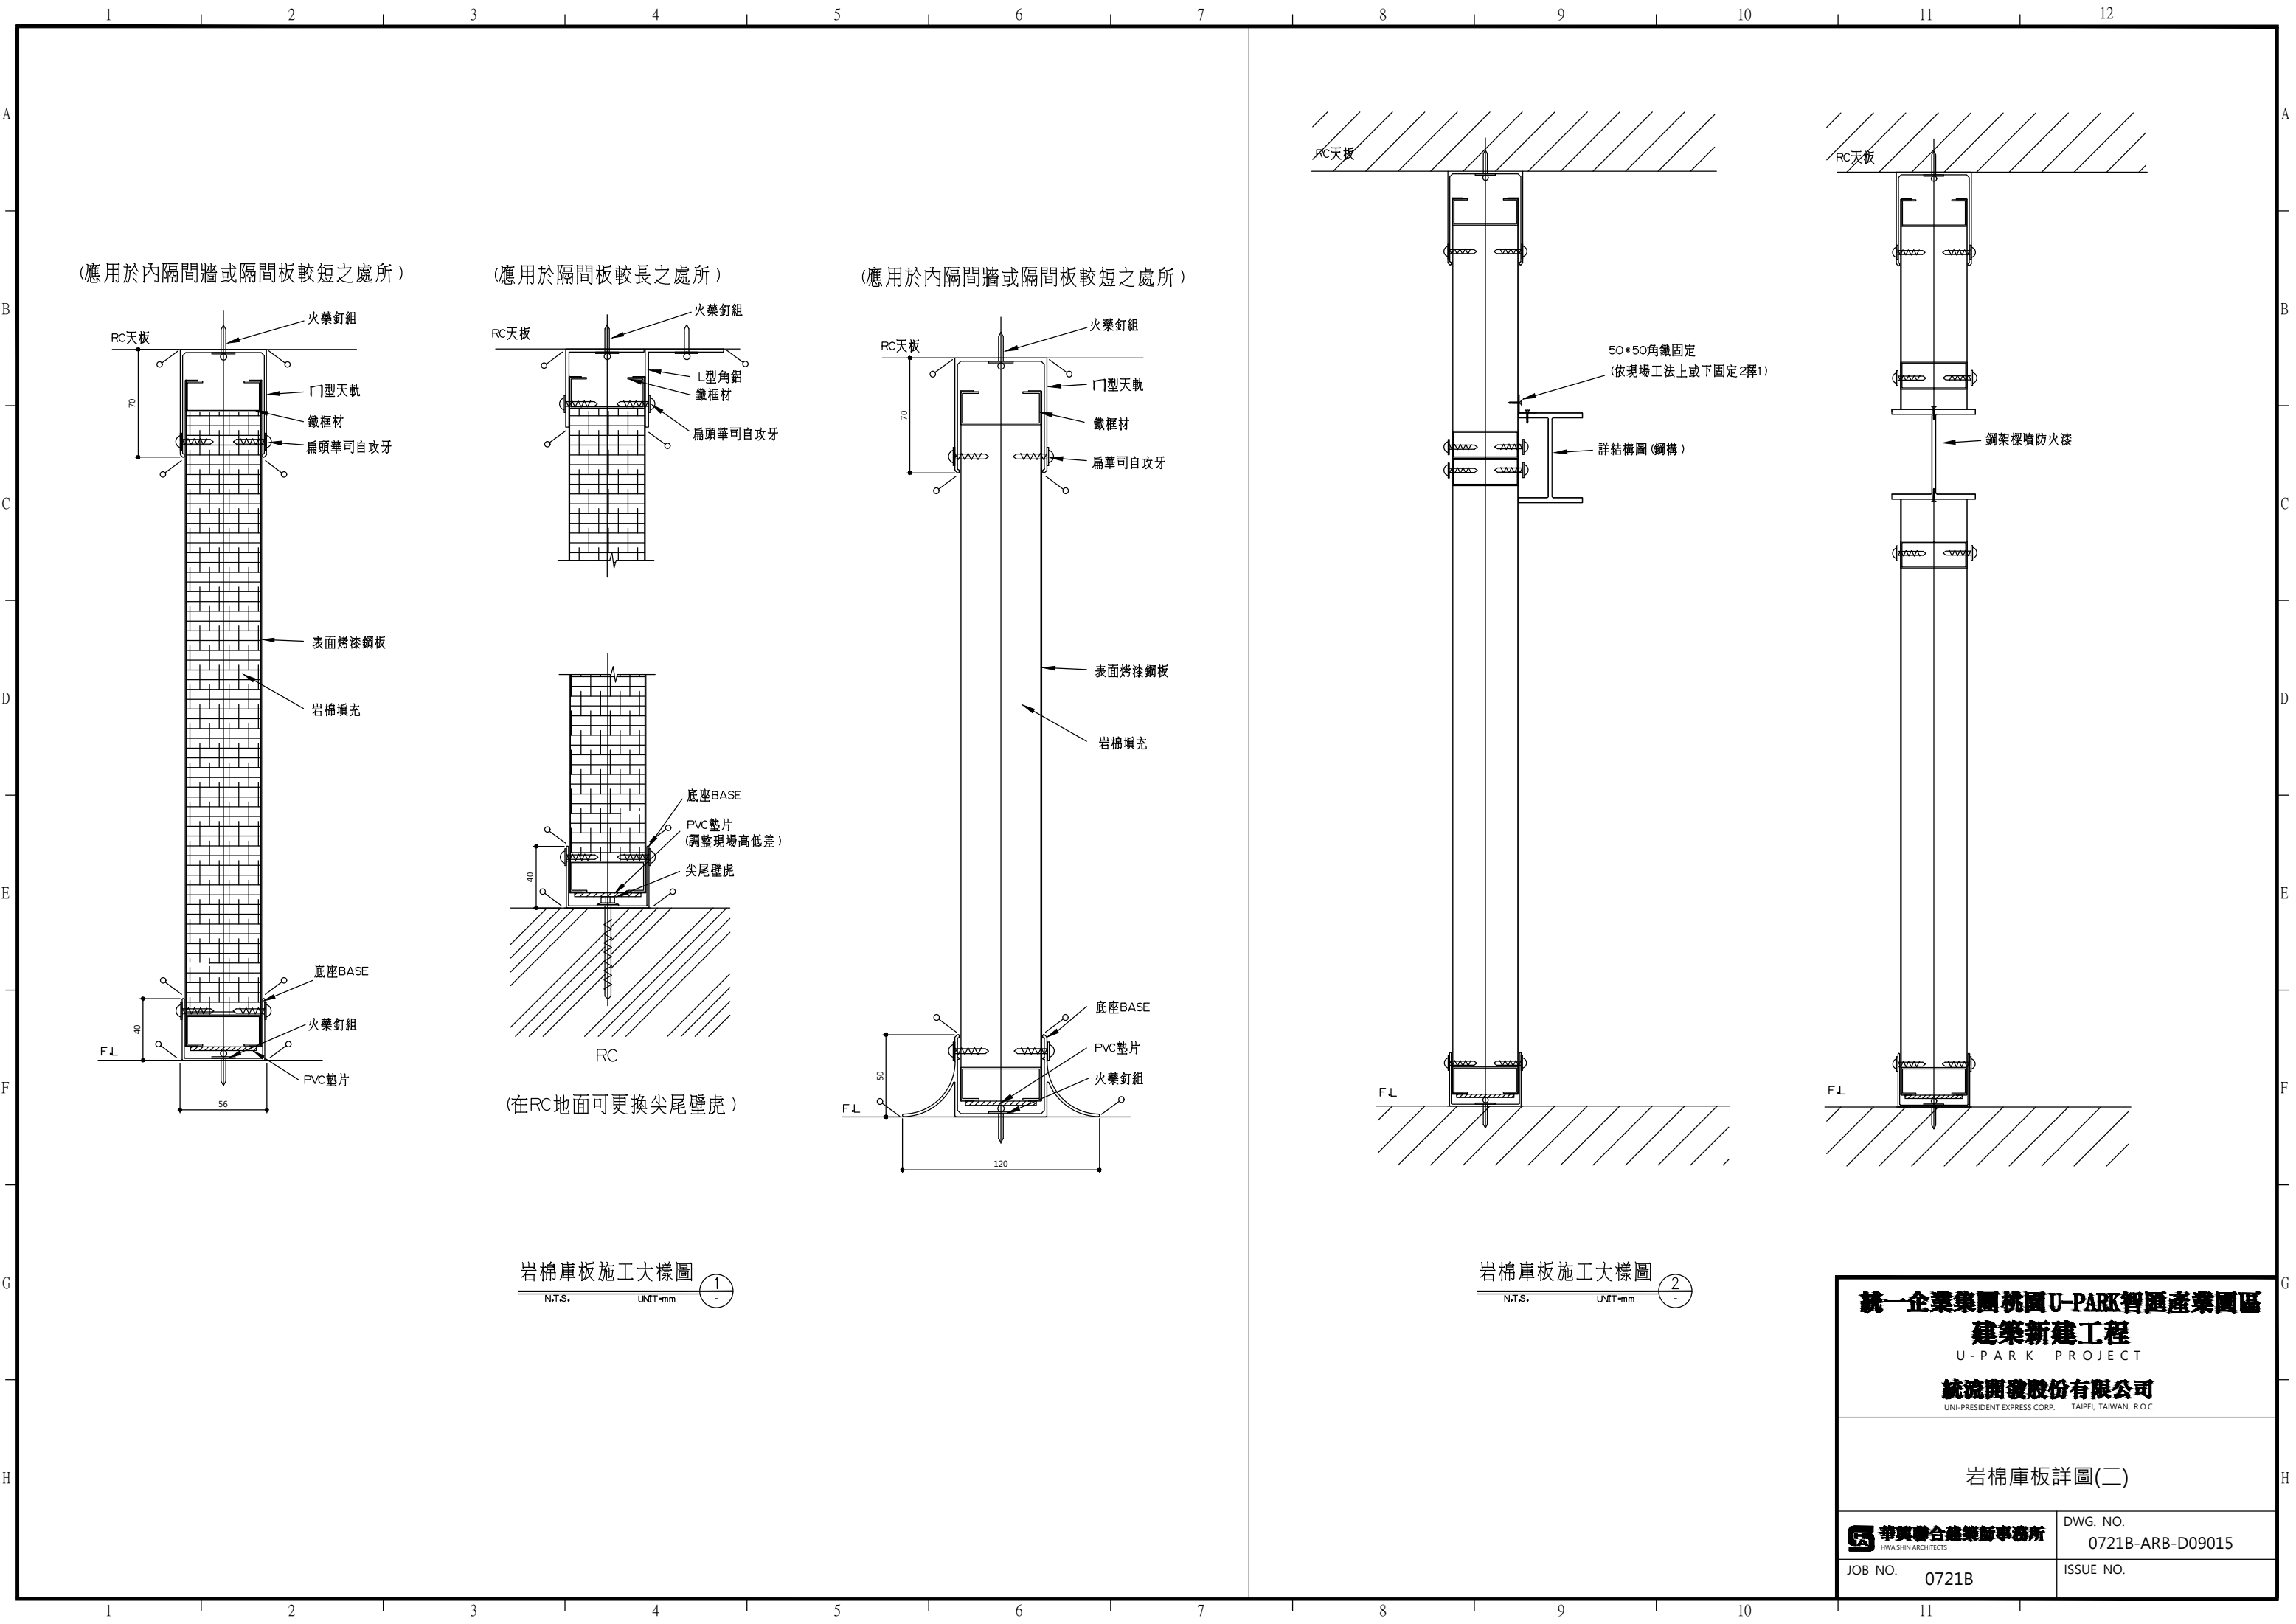

(應用於內隔間牆或隔間板較短之處所)

(應用於隔間板較長之處所)

(應用於內隔間牆或隔間板較短之處所)

50*50角鐵固定
(依現場工法上或下固定2擇1)

詳結構圖(鋼構)

鋼架樑噴防火漆

岩棉庫板施工大樣圖

N.T.S.

UNIT:mm

1

岩棉庫板施工大樣圖

N.T.S.

UNIT:mm

2

統一企業集團桃園U-PARK智匯產業園區

建築新建工程

U-PARK PROJECT

統流開發股份有限公司

UNI-PRESIDENT EXPRESS CORP. TAIPEI, TAIWAN, R.O.C.

岩棉庫板詳圖(二)

華興聯合建築師事務所

HWA SHIN ARCHITECTS


DWG. NO.

0721B-ARB-D09015

JOB NO.

0721B

ISSUE NO.

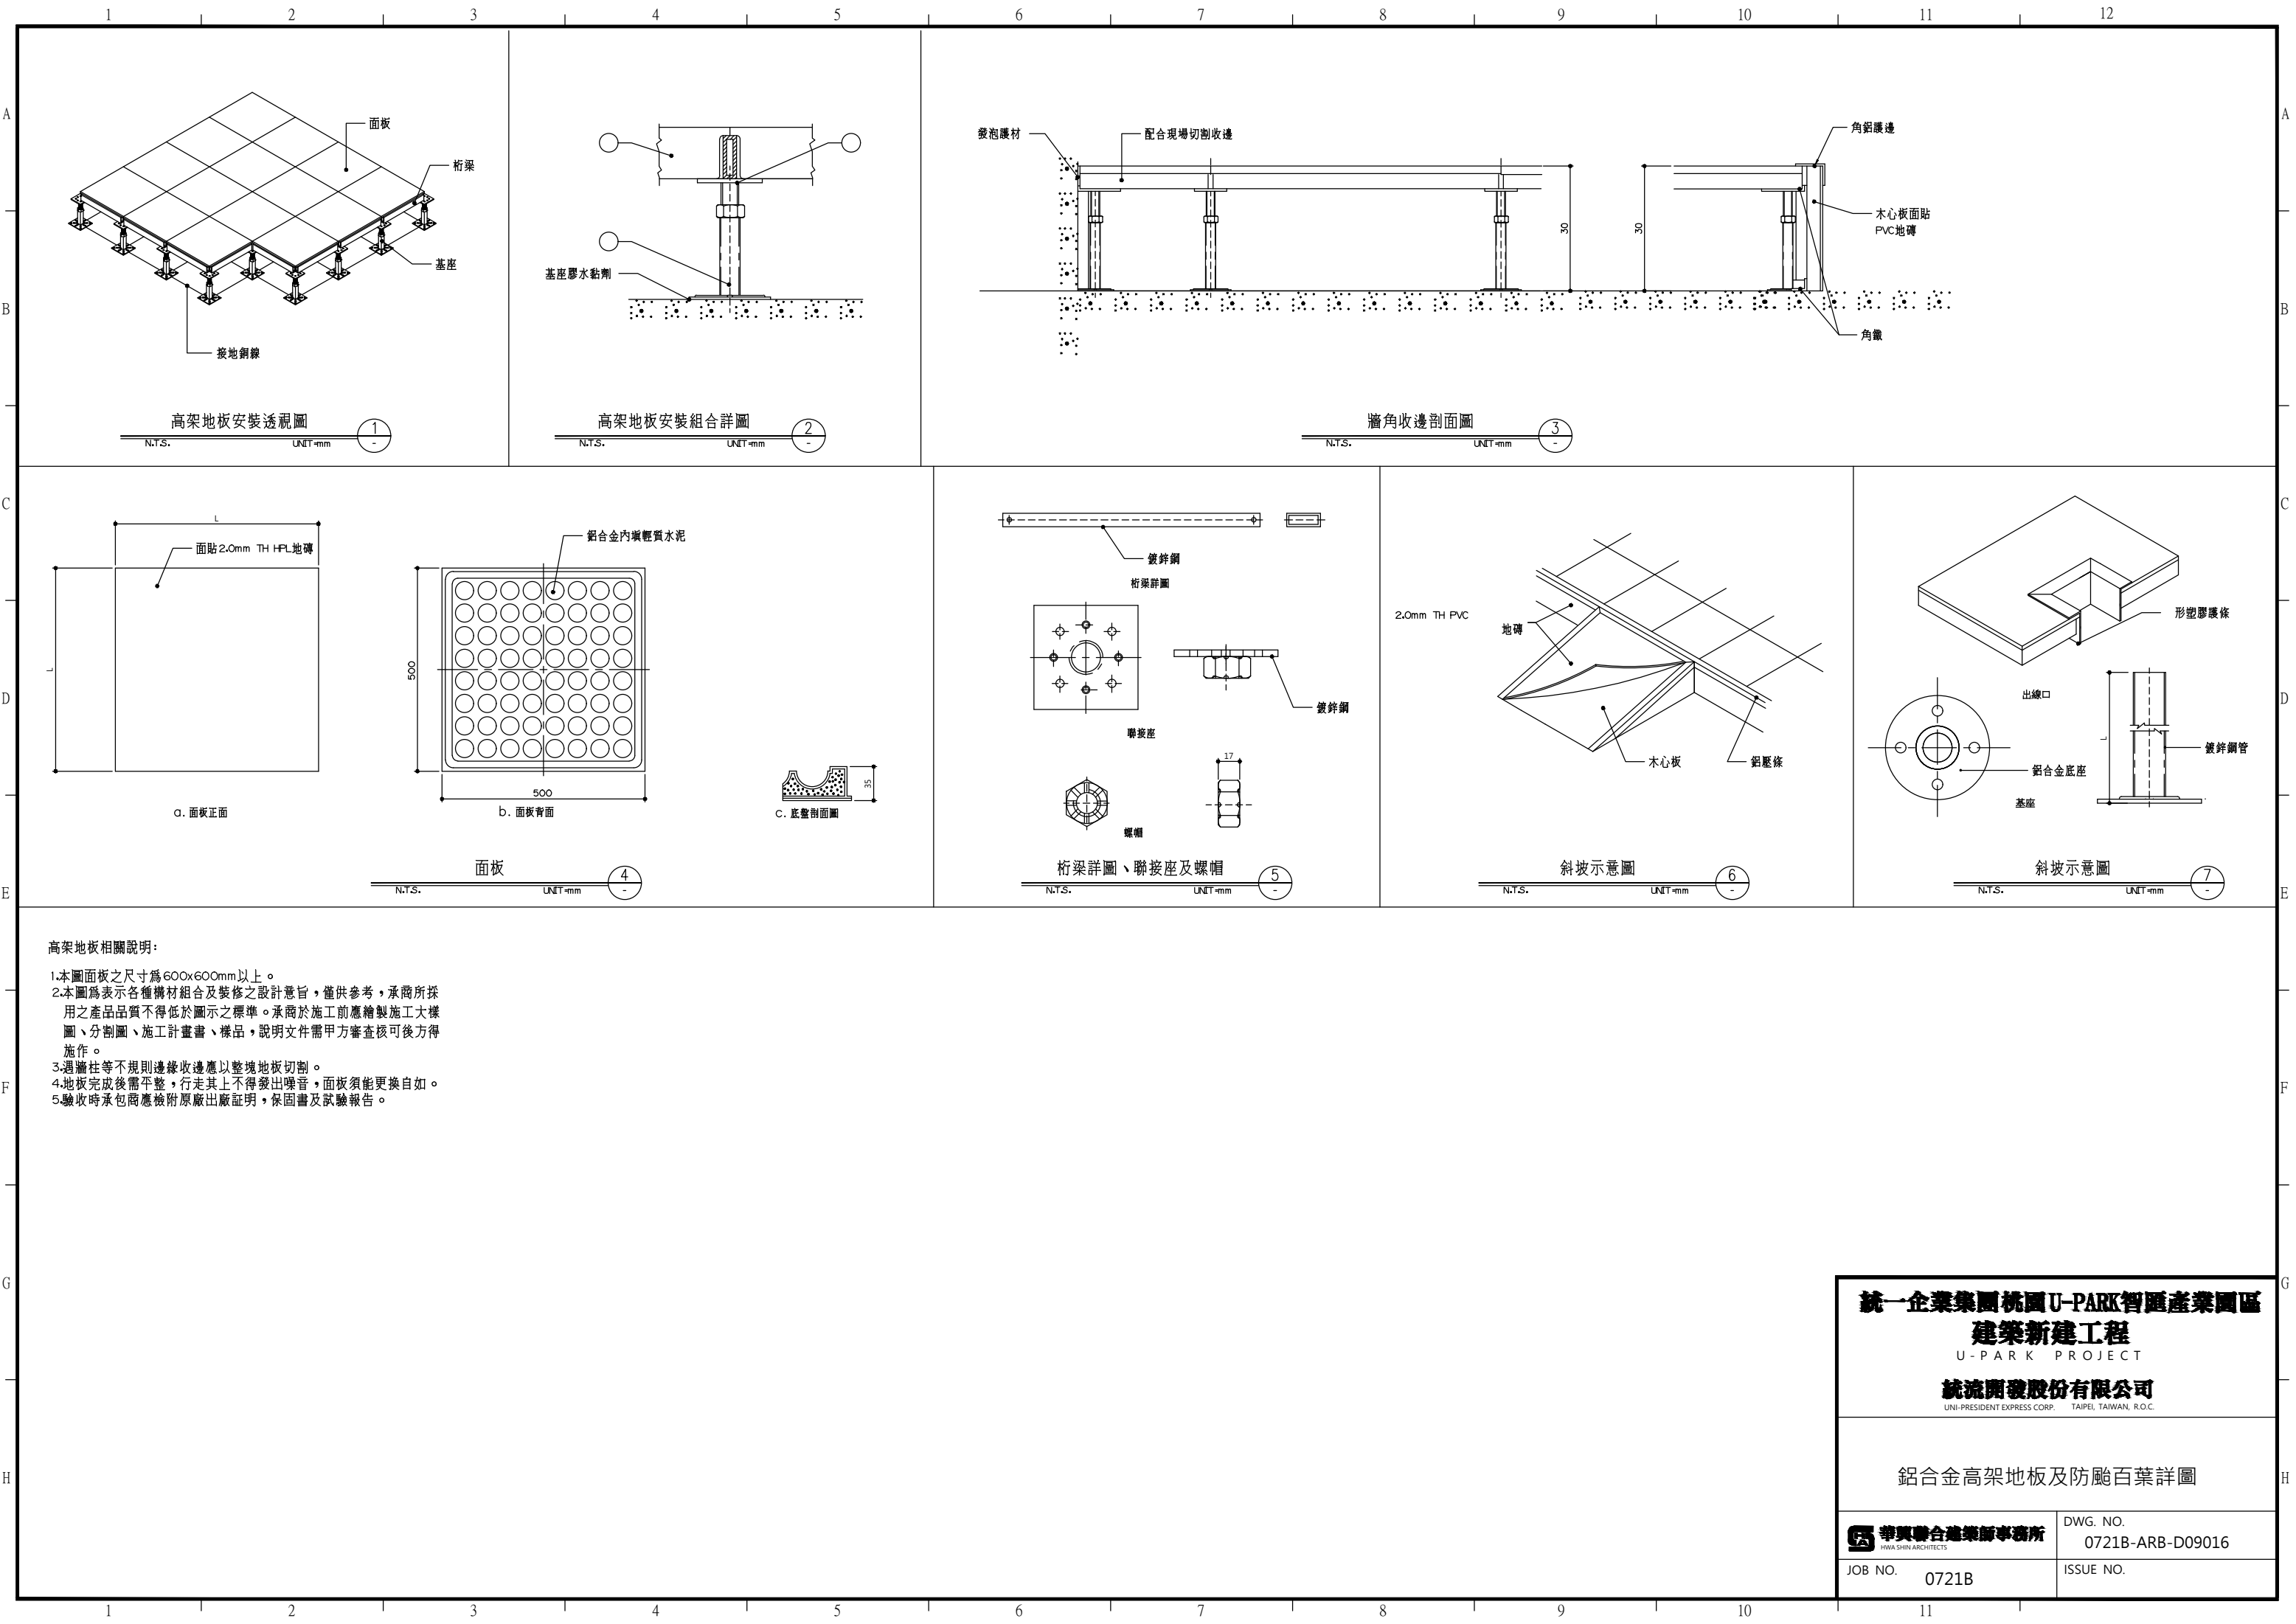

高架地板相關說明:

- 1.本圖面板之尺寸為600x600mm以上。
- 2.本圖為表示各種構材組合及裝修之設計意旨，僅供參考，承商所採用之產品品質不得低於圖示之標準。承商於施工前應繪製施工大樣圖、分割圖、施工計畫書、樣品，說明文件需甲方審查核可後方得施作。
- 3.遇牆柱等不規則邊緣收邊應以整塊地板切割。
- 4.地板完成後需平整，行走其上不得發出噪音，面板須能更換自如。
- 5.驗收時承包商應檢附原廠出廠證明，保固書及試驗報告。

統一企業集團桃園U-PARK智匯產業園區
建築新建工程
U-PARK PROJECT

統流開發股份有限公司
UNI-PRESIDENT EXPRESS CORP. TAIPEI, TAIWAN, R.O.C.


鋁合金高架地板及防颱百葉詳圖

華興聯合建築師事務所
HWA SHIN ARCHITECTS

DWG. NO.
0721B-ARB-D09016

JOB NO.
0721B

ISSUE NO.

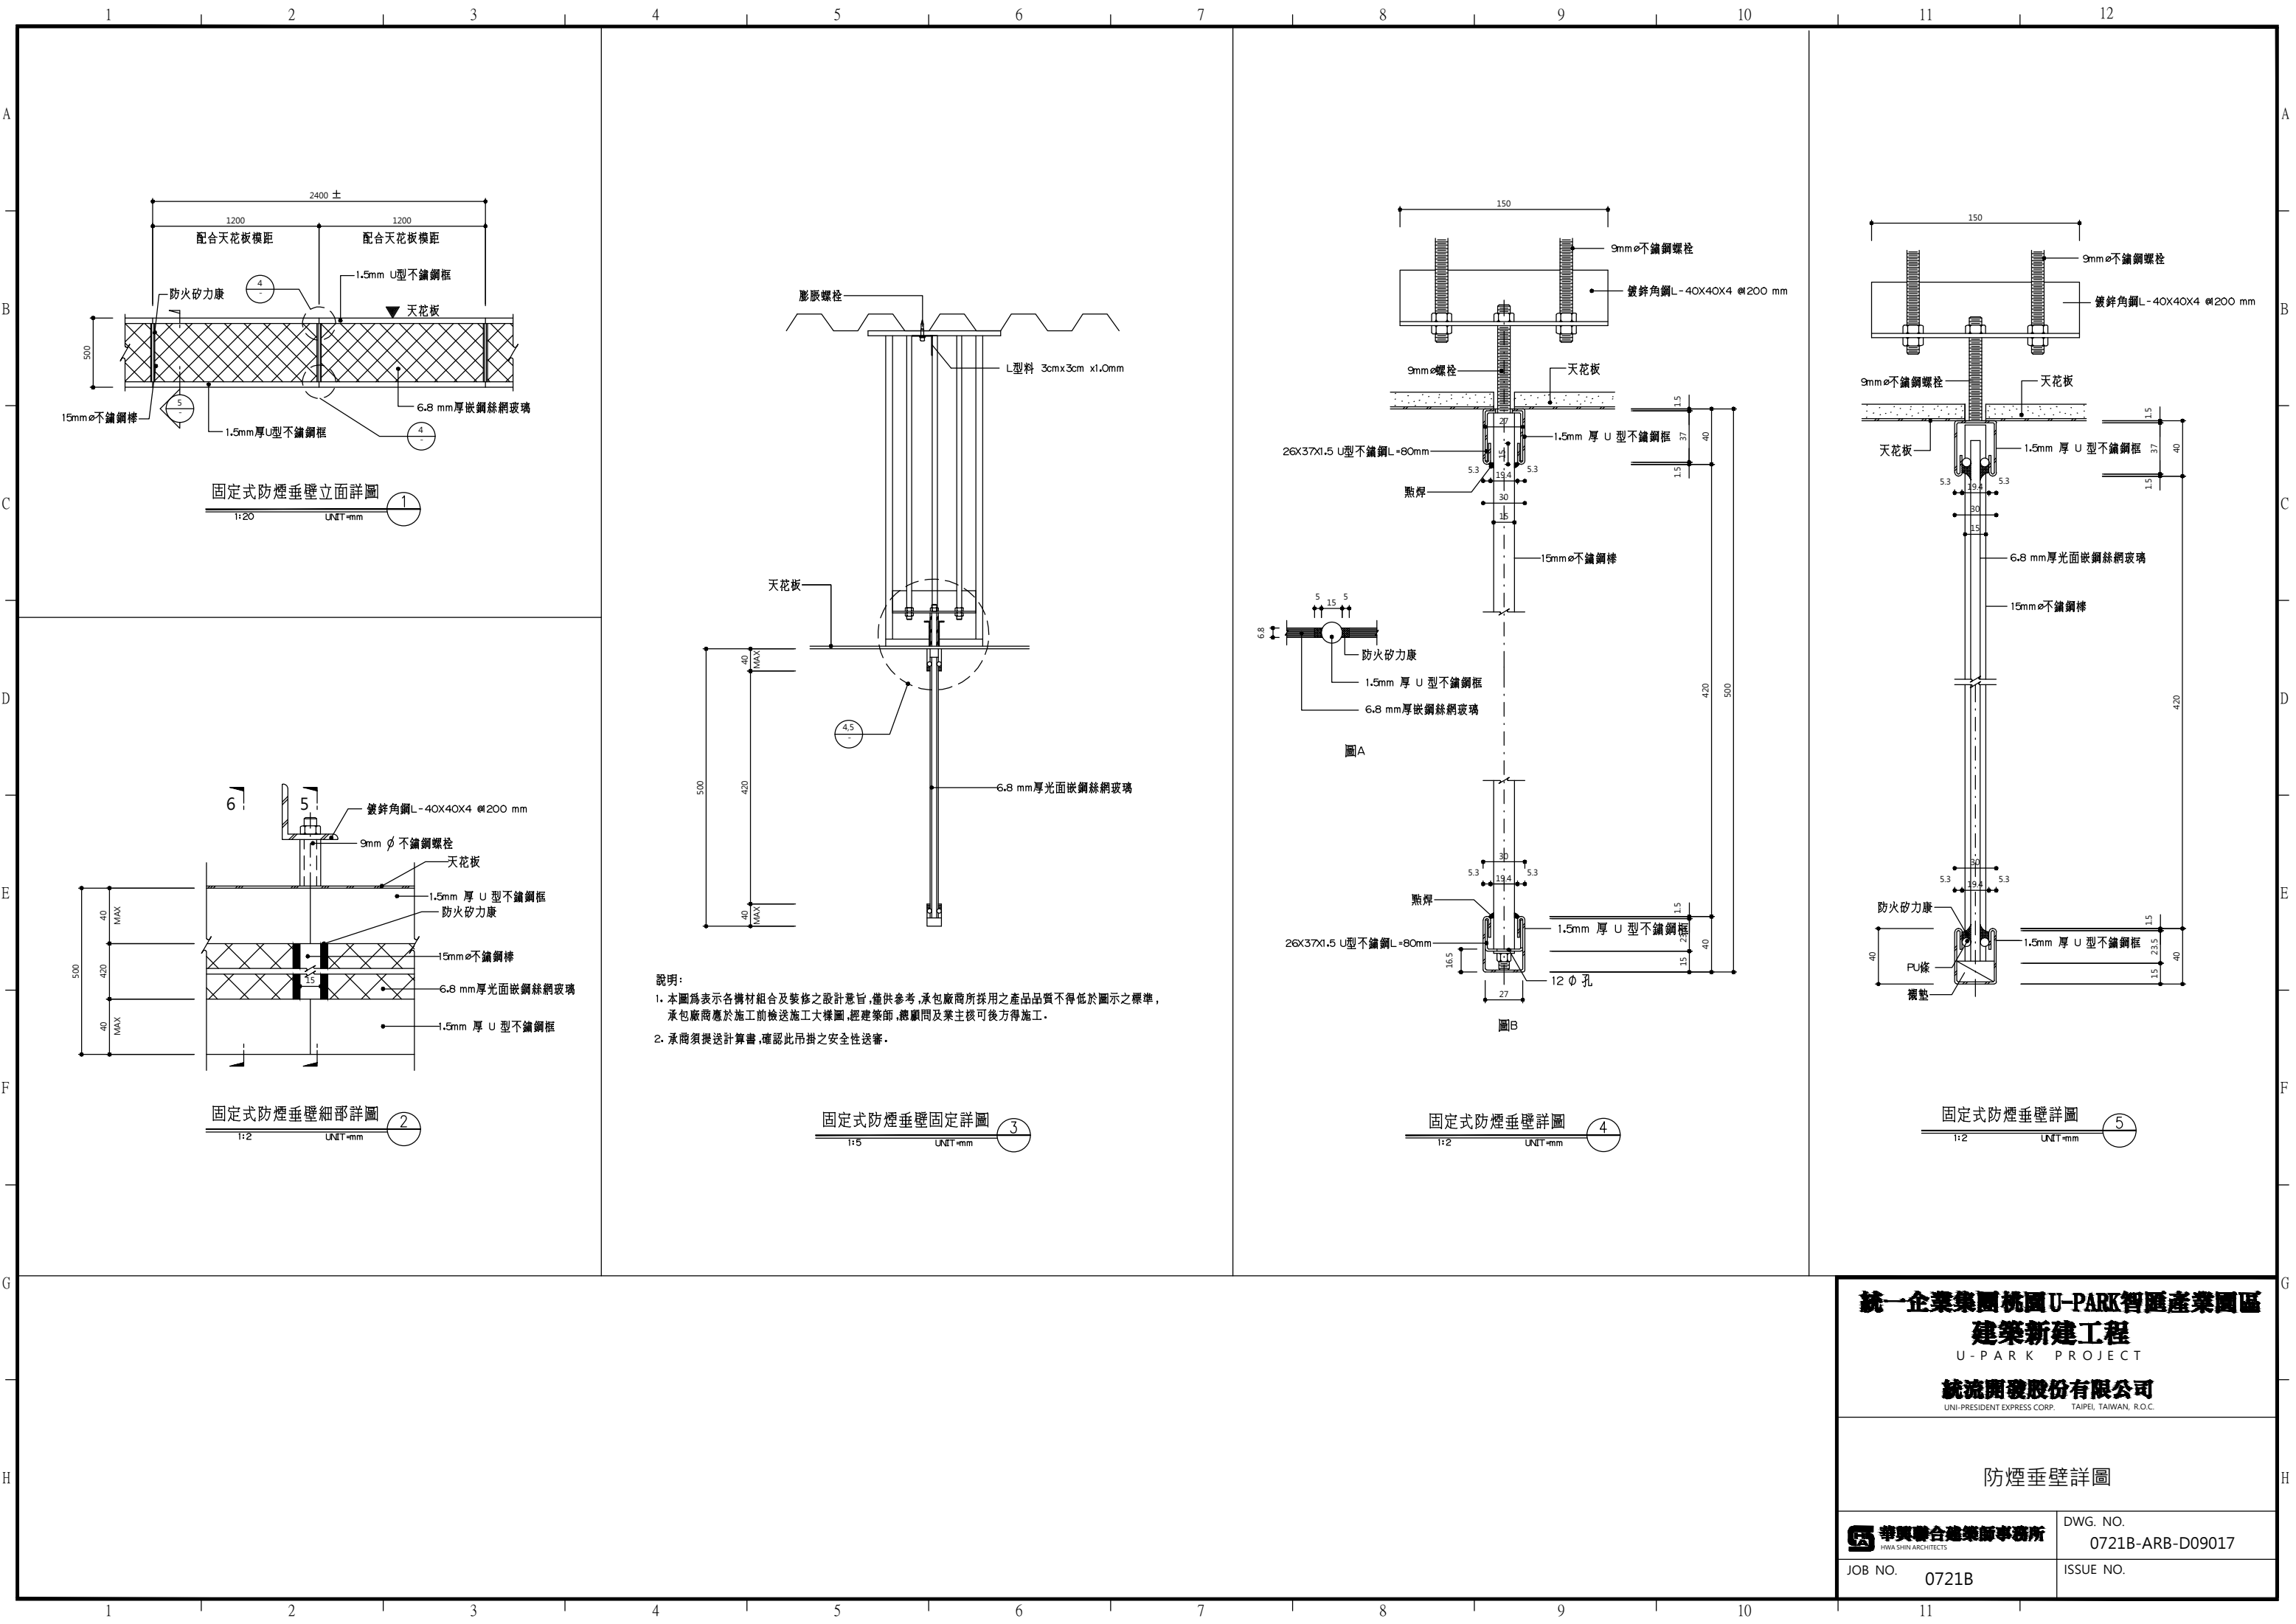

統一企業集團桃園U-PARK智匯產業園區

建築新建工程

U-PARK PROJECT

統流開發股份有限公司

UNI-PRESIDENT EXPRESS CORP. TAIPEI, TAIWAN, R.O.C.

防煙垂壁詳圖


華興聯合建築師事務所

HWA SHIN ARCHITECTS

DWG. NO.
0721B-ARB-D09017

JOB NO.
0721B

ISSUE NO.

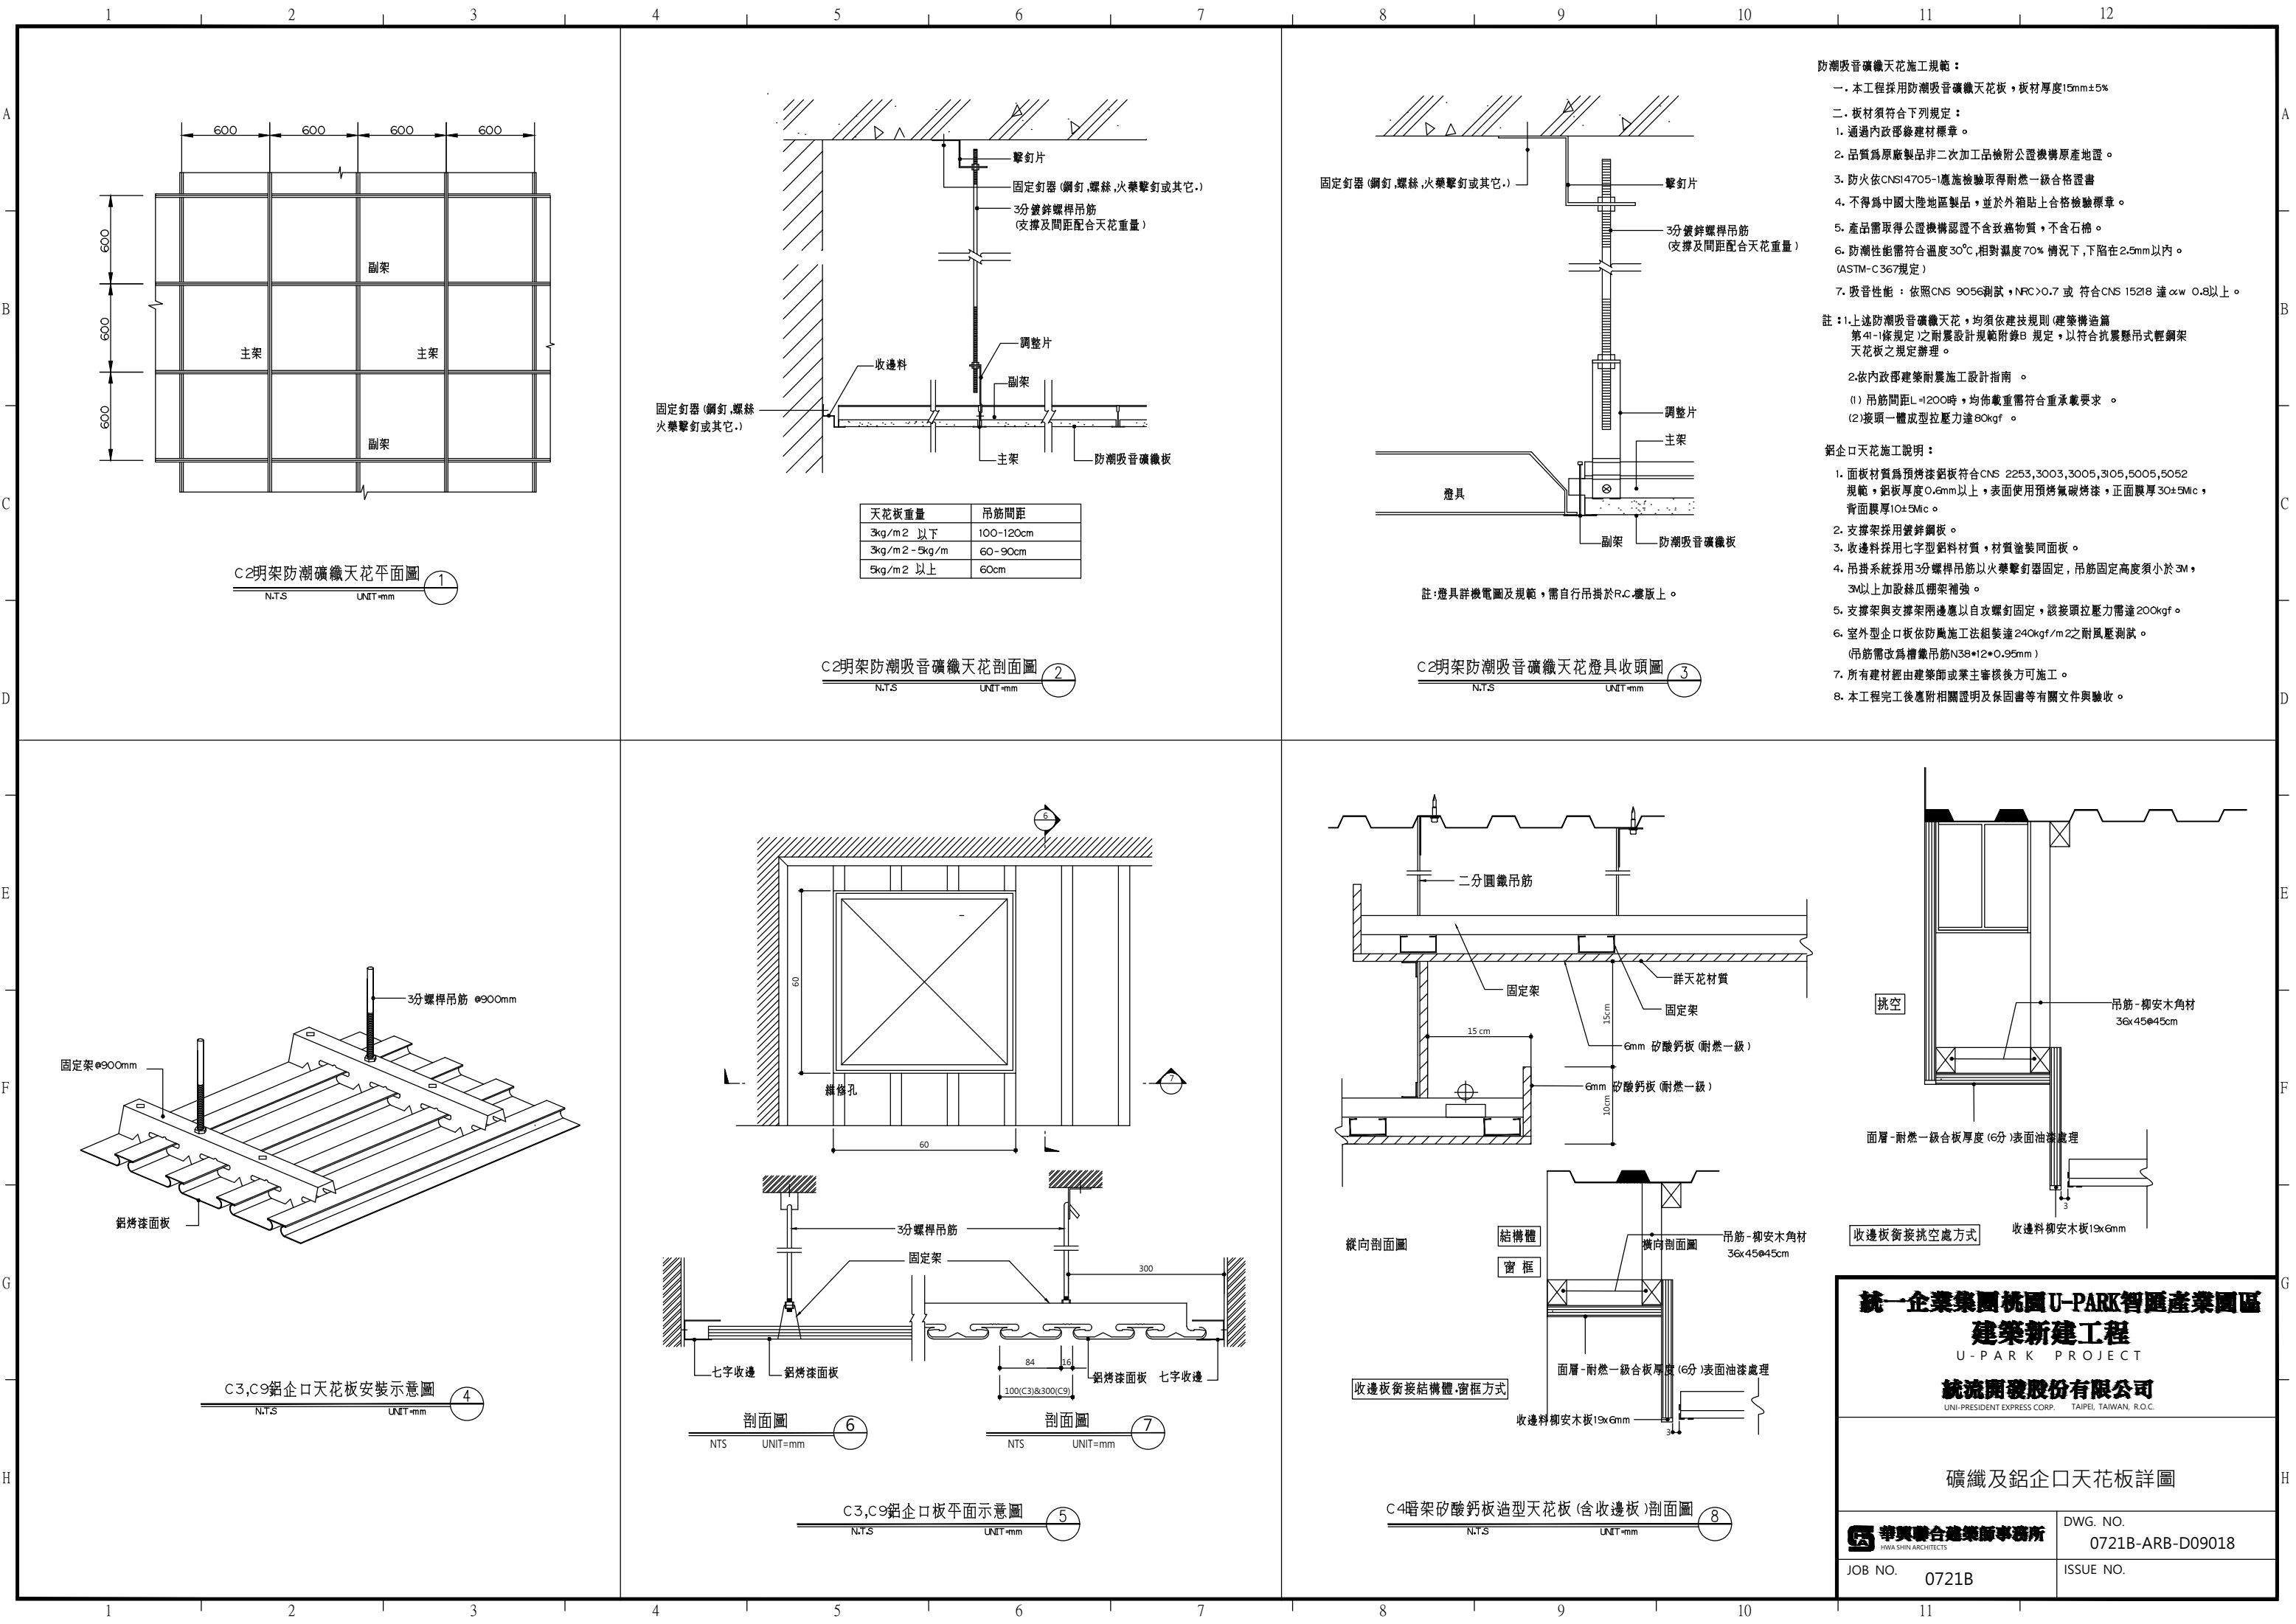

防潮吸音礦纖天花施工規範：

- 本工程採用防潮吸音礦纖天花板，板材厚度15mm±5%
- 板材須符合下列規定：
 - 通過內政部綠建材標章。
 - 品質為原廠製品非二次加工品檢附公證機構原產地證。
 - 防火依CNS14705-1應施檢驗取得耐燃一級合格證書
 - 不得為中國大陸地區製品，並於外箱貼上合格檢驗標章。
 - 產品需取得公證機構認證不含致癌物質，不含石棉。
 - 防潮性能需符合溫度30℃,相對濕度70%情況下,下陷在2.5mm以內。(ASTM-C367規定)
 - 吸音性能：依照CNS 9056測試，NRC>0.7 或 符合CNS 15218 達 α_w 0.8以上。

註：1.上述防潮吸音礦纖天花，均須依建技規則(建築構造篇 第41-1條規定)之耐震設計規範附錄B 規定，以符合抗震懸吊式輕鋼架天花板之規定辦理。

2.依內政部建築耐震施工設計指南。

- 吊筋間距L=1200時，均佈載重需符合重承載要求。
- 接頭一體成型拉壓力達80kgf。

鋁企口天花施工說明：



- 面板材質為預烤漆鋁板符合CNS 2253,3003,3005,3105,5005,5052 規範，鋁板厚度0.6mm以上，表面使用預烤氟碳烤漆，正面膜厚30±5Mic，背面膜厚10±5Mic。
- 支撐架採用鍍鋅鋼板。
- 收邊料採用七字型鋁材材質，材質塗裝同面板。
- 吊掛系統採用3分螺桿吊筋以火藥擊釘器固定，吊筋固定高度須小於3M，3M以上加設絲瓜棚架補強。
- 支撐架與支撐架兩邊應以自攻螺釘固定，該接頭拉壓力需達200kgf。
- 室外型企口板依防風施工法組裝達240kgf/m²之耐風壓測試。(吊筋需改為槽鐵吊筋N38*12*0.95mm)
- 所有建材經由建築師或業主審核後方可施工。
- 本工程完工後應附相關證明及保固書等有關文件與驗收。

統一企業集團桃園U-PARK智匯產業園區
建築新建工程
U-PARK PROJECT
統流開發股份有限公司
UNI-PRESIDENT EXPRESS CORP. TAIPEI, TAIWAN, R.O.C.

礦纖及鋁企口天花板詳圖

DWG. NO. 0721B-ARB-D09018
JOB NO. 0721B
ISSUE NO.

華興聯合建築師事務所
HWA SHIN ARCHITECTS

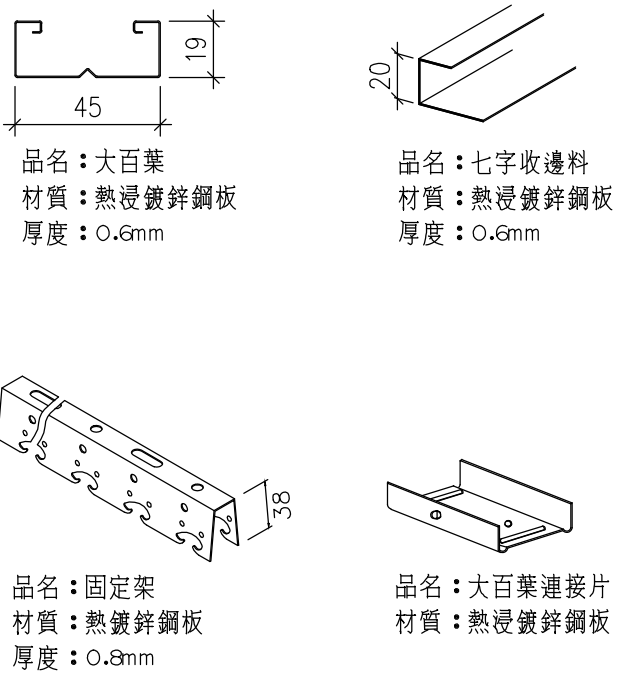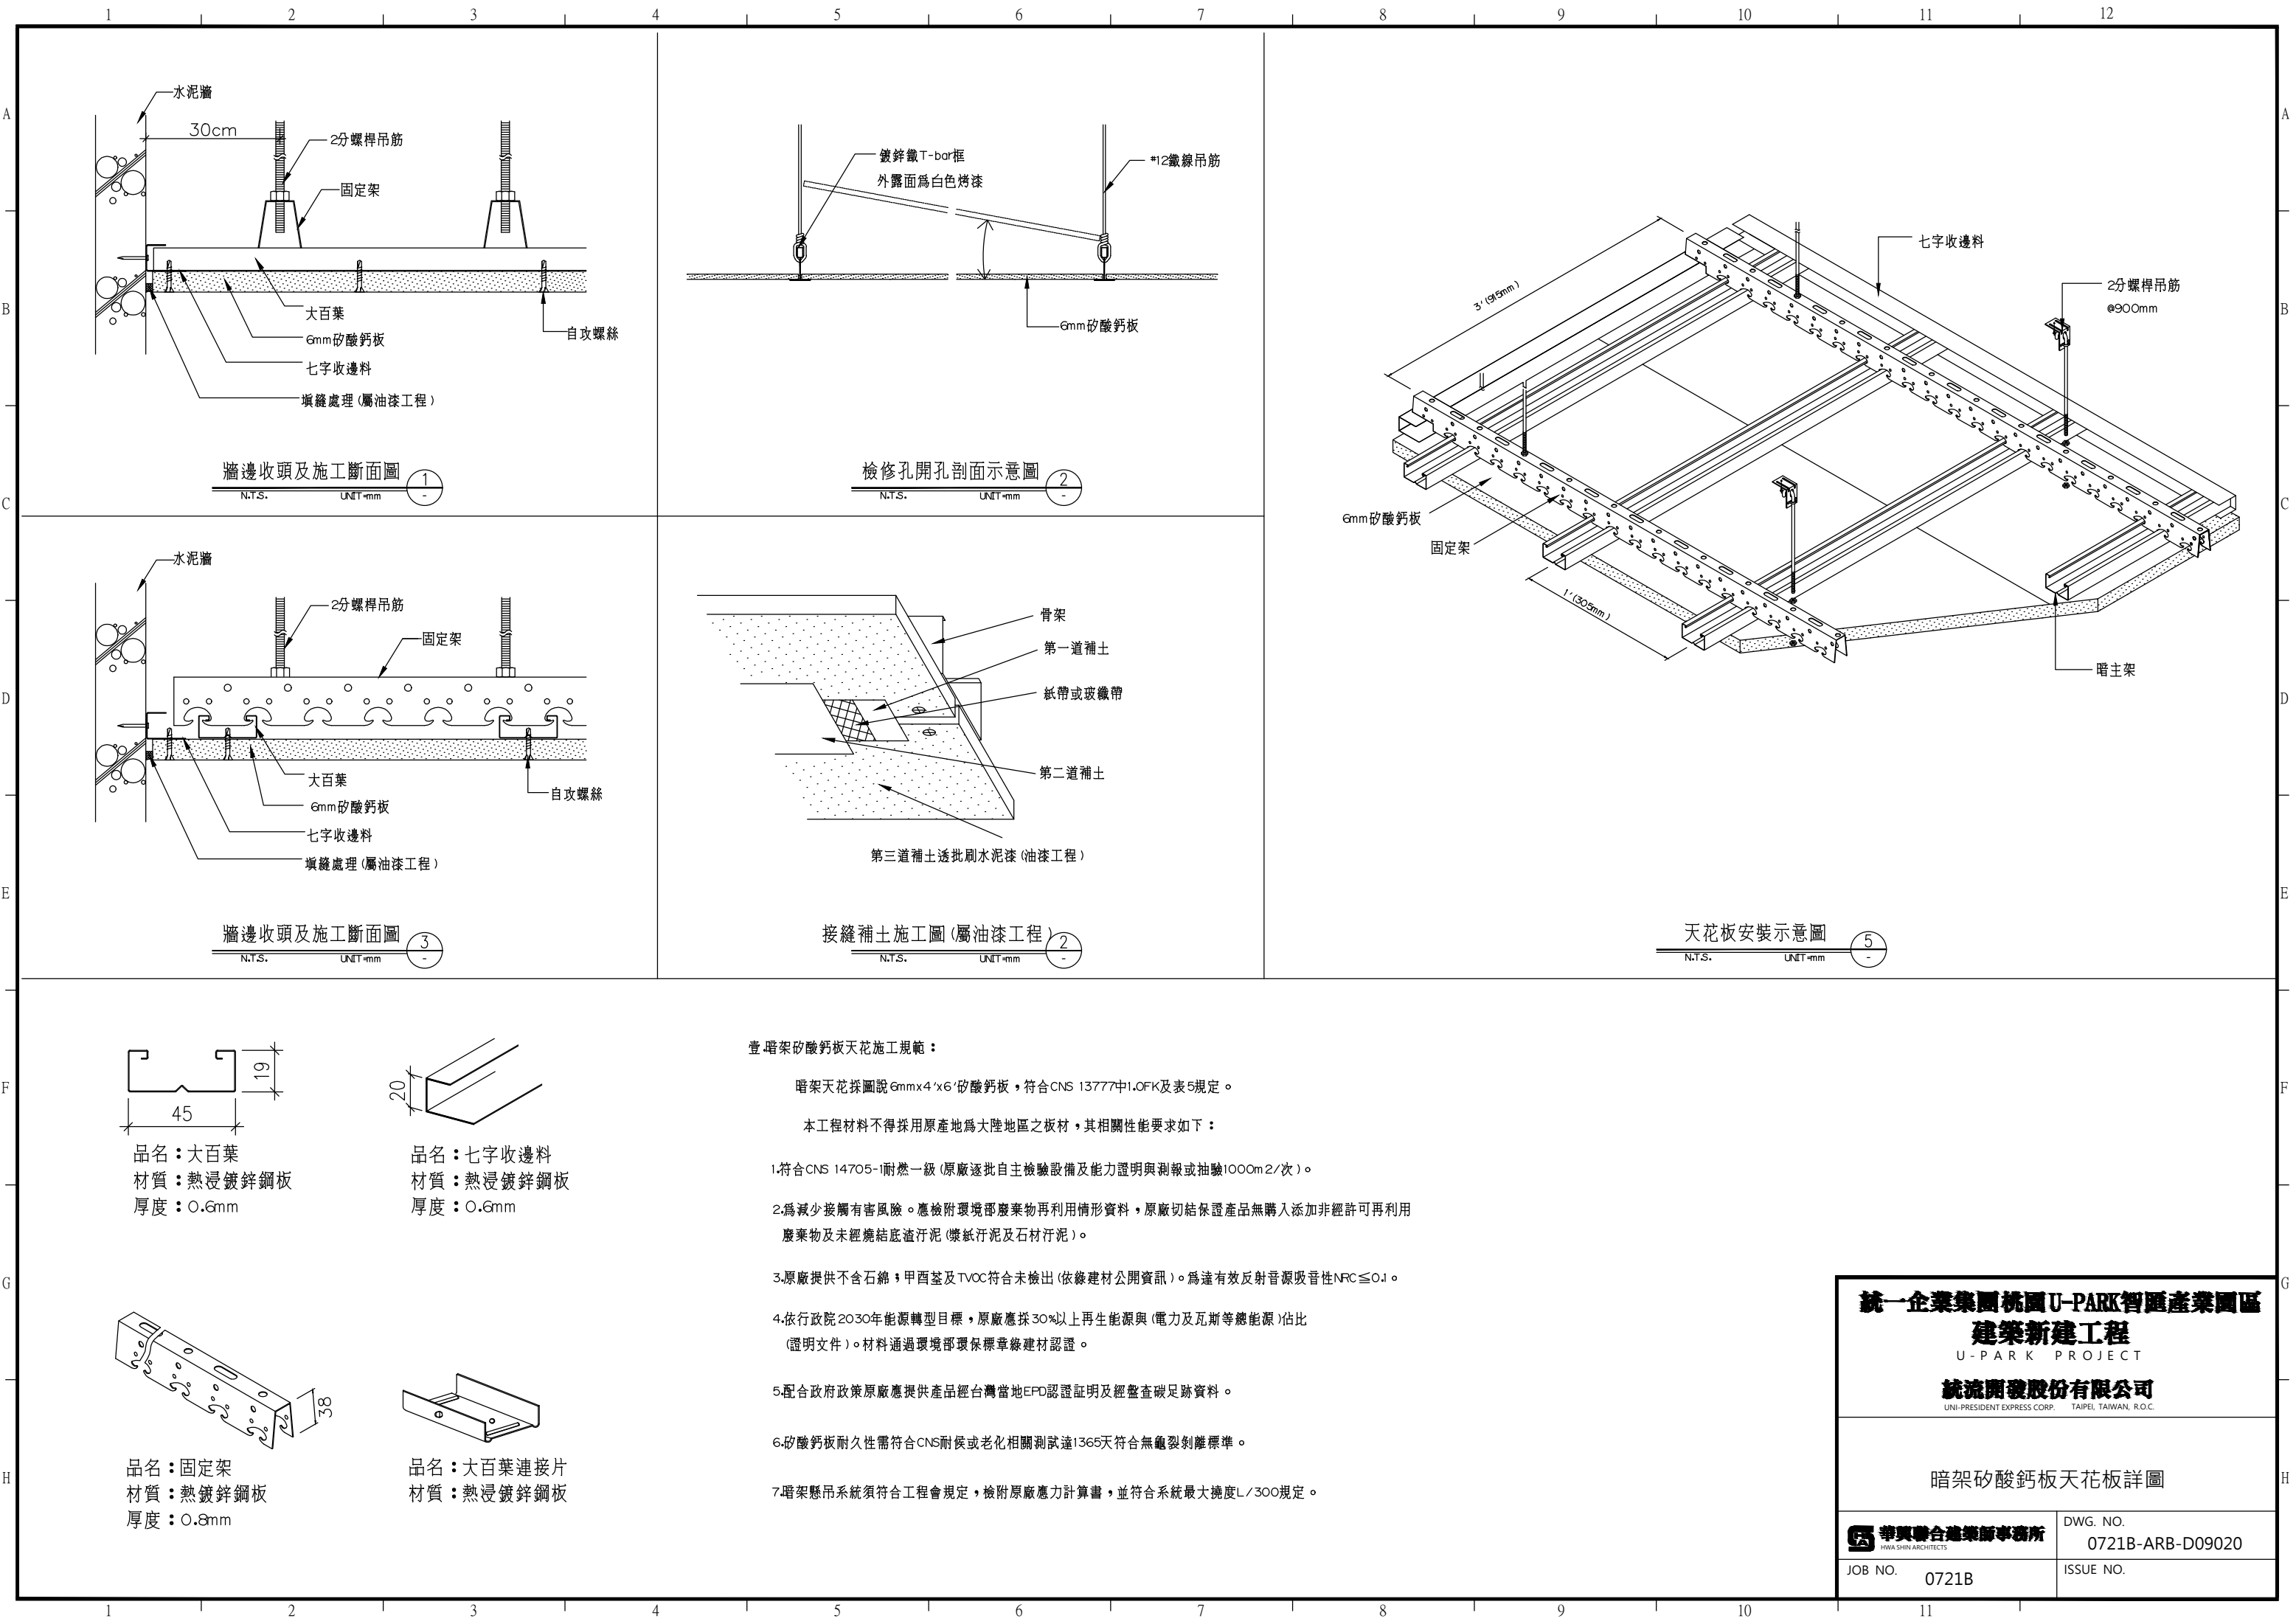

- 壹.暗架矽酸鈣板天花施工規範：
- 暗架天花採圖說 6mmx4'x6'矽酸鈣板，符合CNS 13777中1.0FK及表5規定。
- 本工程材料不得採用原產地為大陸地區之板材，其相關性能要求如下：
- 1.符合CNS 14705-1耐燃一級(原廠逐批自主檢驗設備及能力證明與測報或抽驗1000m2/次)。
 - 2.為減少接觸有害風險。應檢附環境部廢棄物再利用情形資料，原廠切結保證產品無購入添加非經許可再利用廢棄物及未經燒結底渣汙泥(漿紙汙泥及石材汙泥)。
 - 3.原廠提供不含石棉，甲酉基及TVOC符合未檢出(依綠建材公開資訊)。為達有效反射音源吸音性 $NRC \leq 0.1$ 。
 - 4.依行政院2030年能源轉型目標，原廠應採30%以上再生能源與(電力及瓦斯等總能源)佔比(證明文件)。材料通過環境部環保標章綠建材認證。
 - 5.配合政府政策原廠應提供產品經台灣當地EPD認證證明及經盤查碳足跡資料。
 - 6.矽酸鈣板耐久性需符合CNS耐候或老化相關測試達1365天符合無龜裂剝離標準。
 - 7.暗架懸吊系統須符合工程會規定，檢附原廠應力計算書，並符合系統最大撓度 $L/300$ 規定。

統一企業集團桃園U-PARK智匯產業園區

建築新建工程

U-PARK PROJECT

統流開發股份有限公司

UNI-PRESIDENT EXPRESS CORP. TAIPEI, TAIWAN, R.O.C.

暗架矽酸鈣板天花板詳圖

華興聯合建築師事務所

HWA SHIN ARCHITECTS


DWG. NO.

0721B-ARB-D09020

JOB NO.

0721B

ISSUE NO.

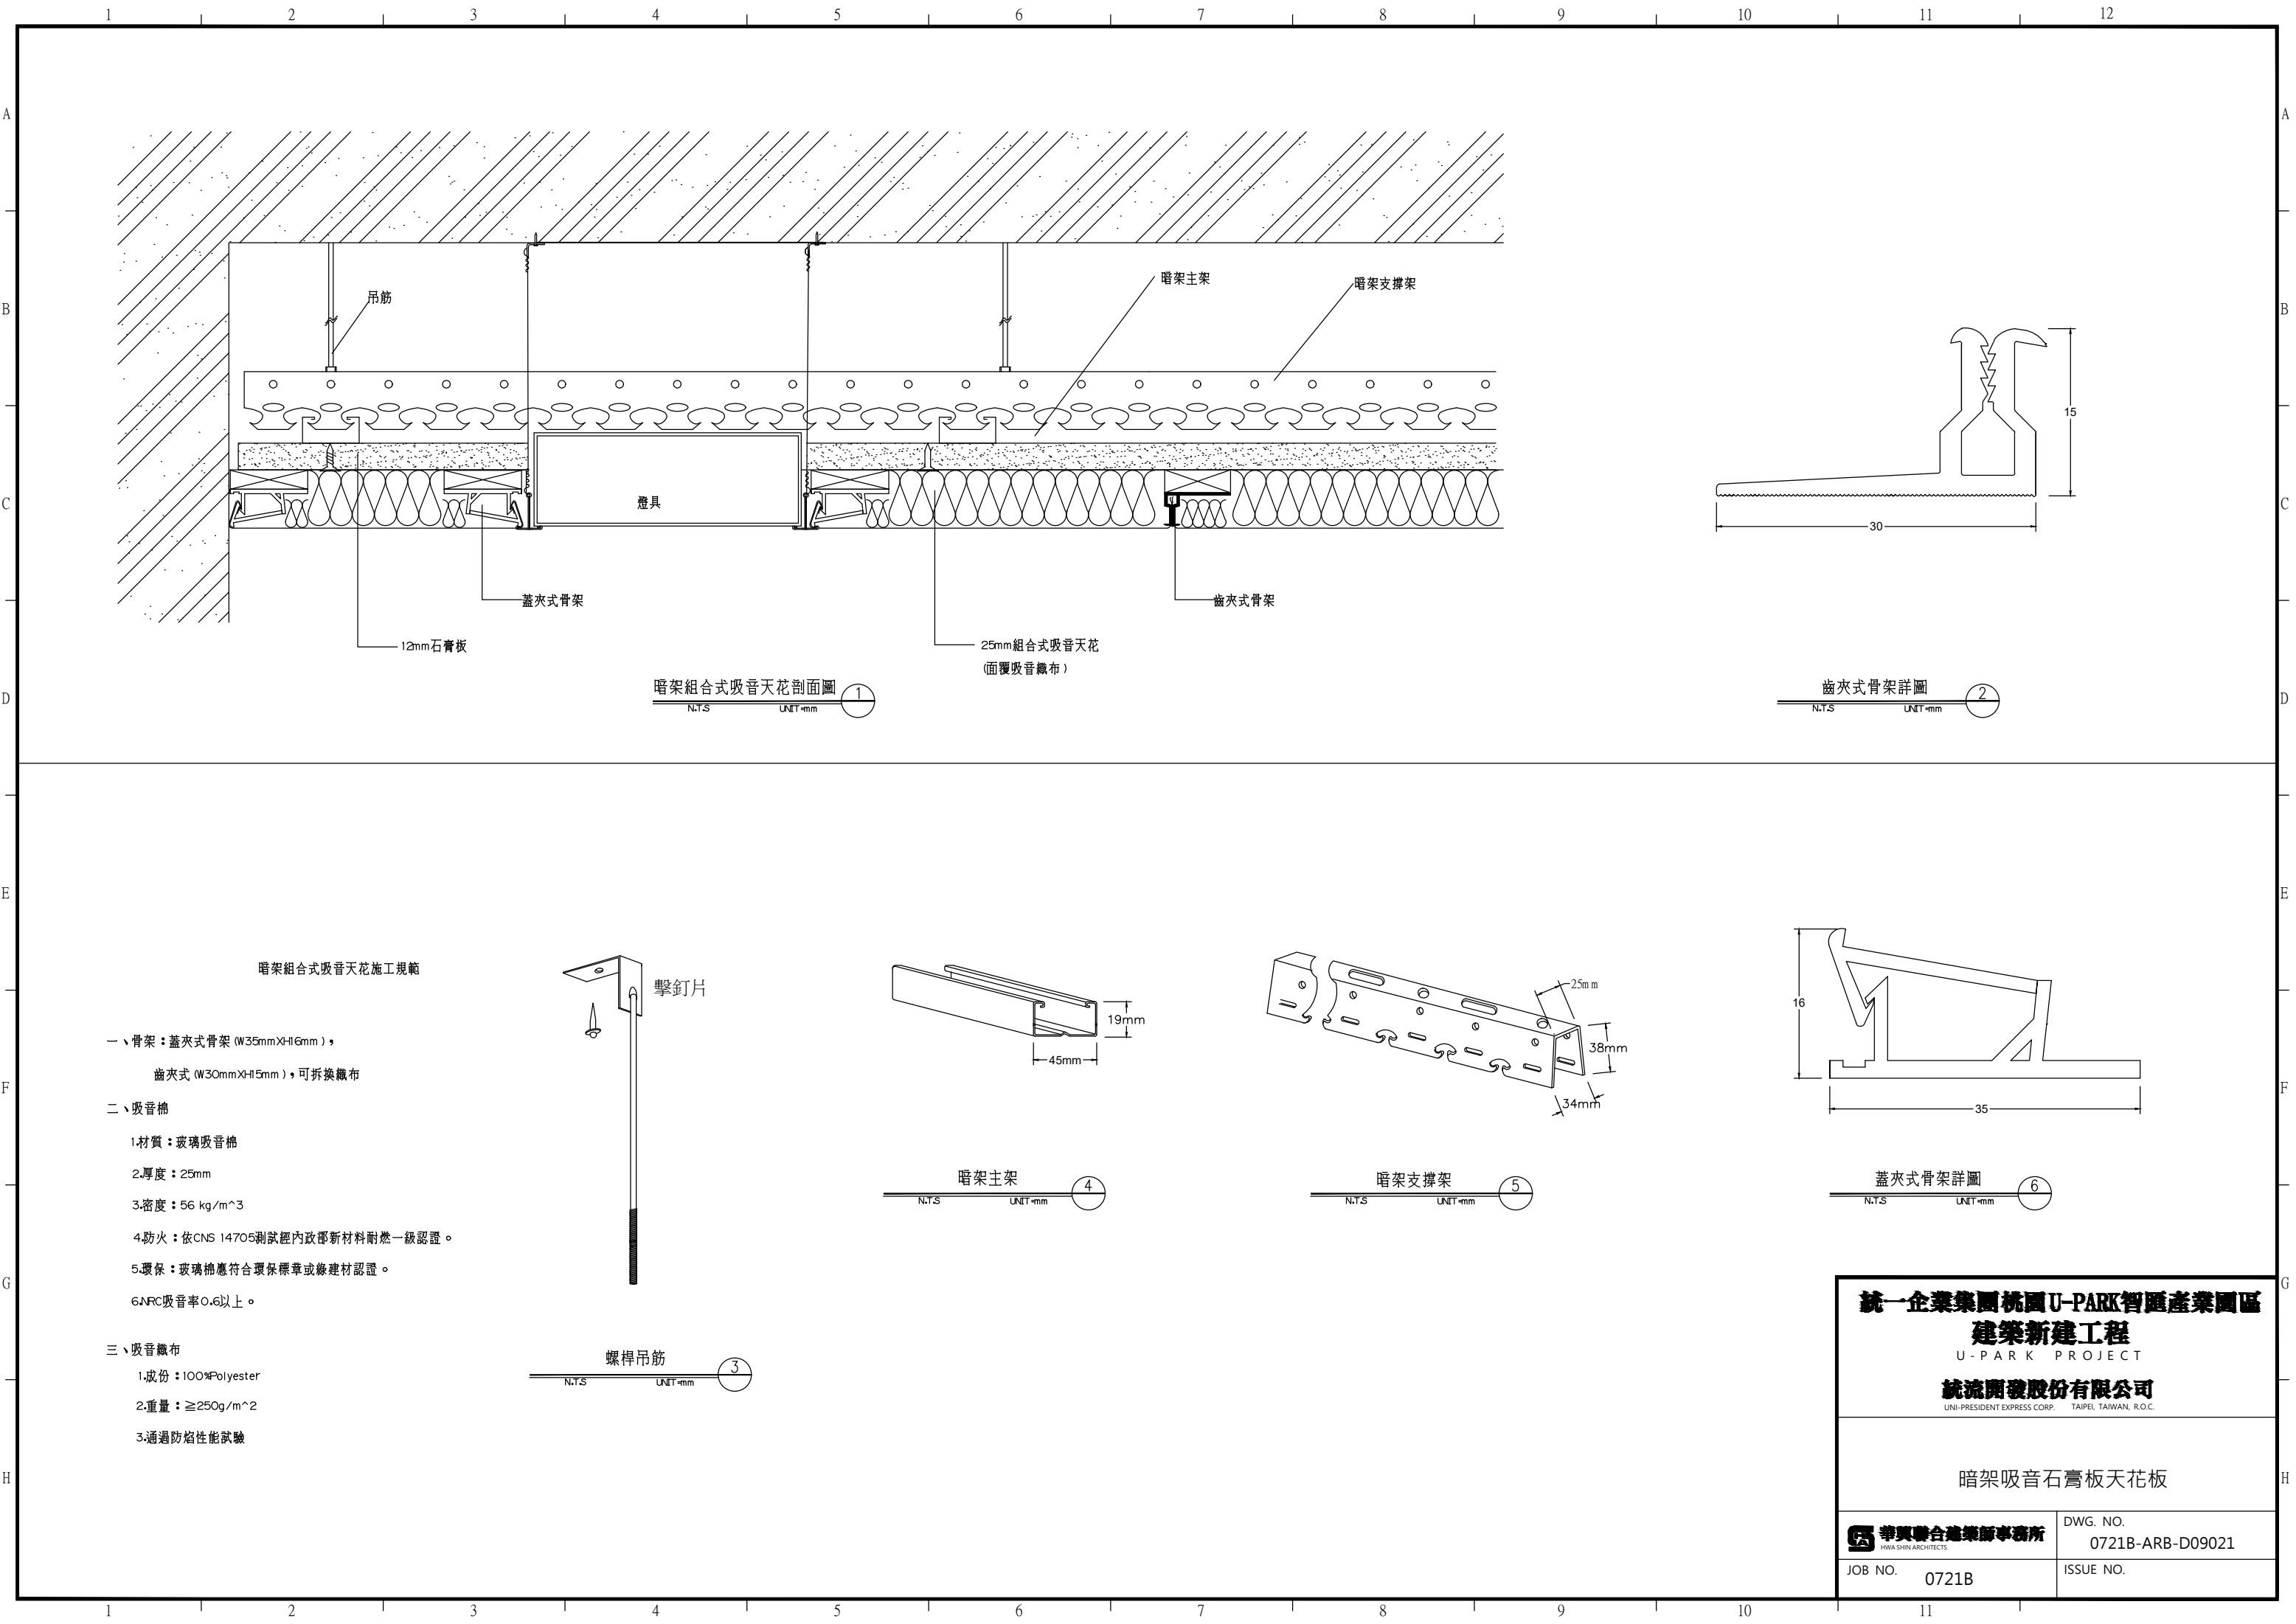

1 2 3 4 5 6 7 8 9 10 11 12

A B C D E F G H

吊筋

暗架主架

暗架支撐架

燈具

蓋夾式骨架

12mm石膏板

25mm組合式吸音天花
(面覆吸音織布)

齒夾式骨架

齒夾式骨架詳圖

暗架組合式吸音天花剖面圖

暗架組合式吸音天花施工規範

一、骨架：蓋夾式骨架 (W35mmX-H16mm)，
齒夾式 (W30mmX-H15mm)，可拆換織布

二、吸音棉

1.材質：玻璃吸音棉

2.厚度：25mm

3.密度：56 kg/m³

4.防火：依CNS 14705測試經內政部新材料耐燃一級認證。

5.環保：玻璃棉應符合環保標章或綠建材認證。

6.ARC吸音率0.6以上。

三、吸音織布

1.成份：100%Polyester

2.重量：≥250g/m²

3.通過防焰性能試驗

擊釘片

螺桿吊筋

暗架主架

暗架支撐架

蓋夾式骨架詳圖

統一企業集團桃園U-PARK智匯產業園區
建築新建工程
U-PARK PROJECT
統流開發股份有限公司
UNI-PRESIDENT EXPRESS CORP. TAIPEI, TAIWAN, R.O.C.


暗架吸音石膏板天花板

華興聯合建築師事務所
HWA SHIN ARCHITECTS

DWG. NO.
0721B-ARB-D09021

JOB NO.
0721B

ISSUE NO.

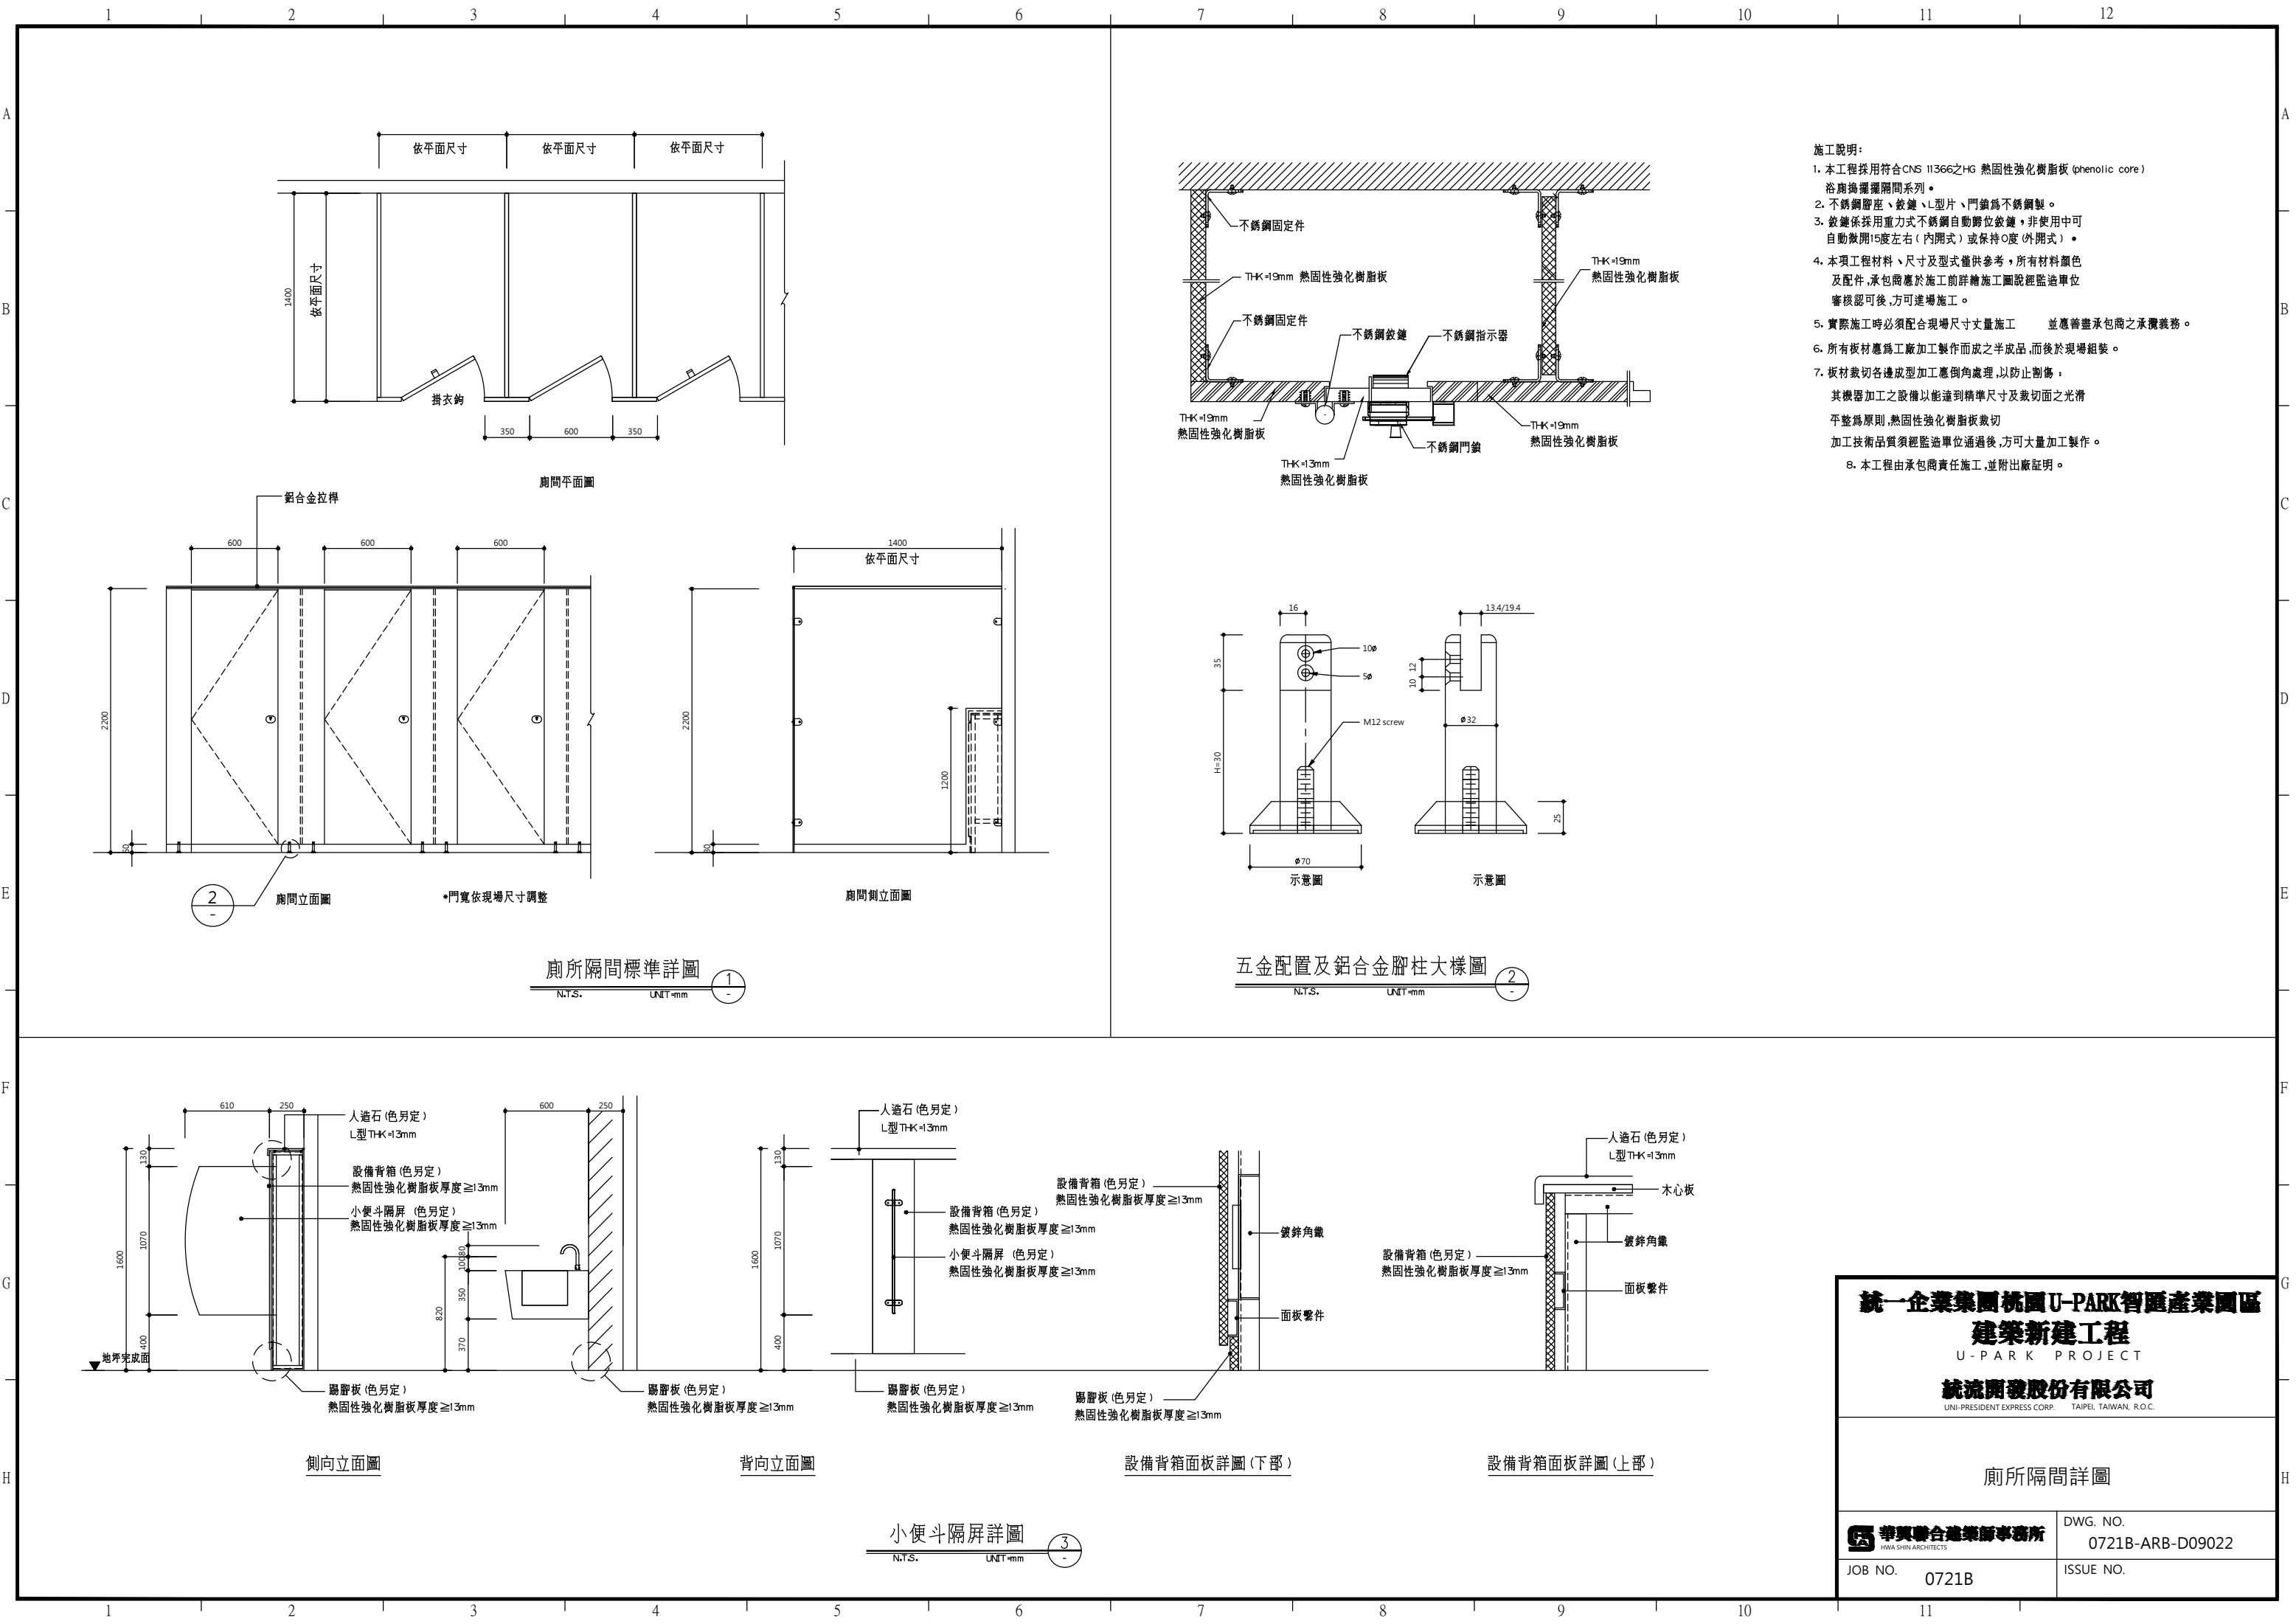


- 施工說明：
1. 本工程採用符合CNS 11366之HG 熱固性強化樹脂板 (phenolic core) 浴廁掛欄擺隔間系列。
 2. 不銹鋼腳座、鉸鏈、L型片、門鎖為不銹鋼製。
 3. 鉸鏈係採用重力式不銹鋼自動歸位鉸鏈，非使用中可自動微開15度左右（內開式）或保持0度（外開式）。
 4. 本項工程材料、尺寸及型式僅供參考，所有材料顏色及配件，承包商應於施工前詳繪施工圖說經監造單位審核可後，方可進場施工。
 5. 實際施工時必須配合現場尺寸丈量施工 並應善盡承包商之承攬義務。
 6. 所有板材應為工廠加工製作而成之半成品，而後於現場組裝。
 7. 板材裁切各邊成型加工應倒角處理，以防止割傷，其機器加工之設備以能達到精準尺寸及裁切面之光滑平整為原則，熱固性強化樹脂板裁切加工技術品質須經監造單位通過後，方可大量加工製作。
 8. 本工程由承包商責任施工，並附出廠證明。


統一企業集團桃園U-PARK智匯產業園區
建築新建工程
U-PARK PROJECT
統流開發股份有限公司
UNI-PRESIDENT EXPRESS CORP. TAIPEI, TAIWAN, R.O.C.

廁所隔間詳圖

 華興聯合建築師事務所 HWA SHIN ARCHITECTS	DWG. NO. 0721B-ARB-D09022
JOB NO. 0721B	ISSUE NO.

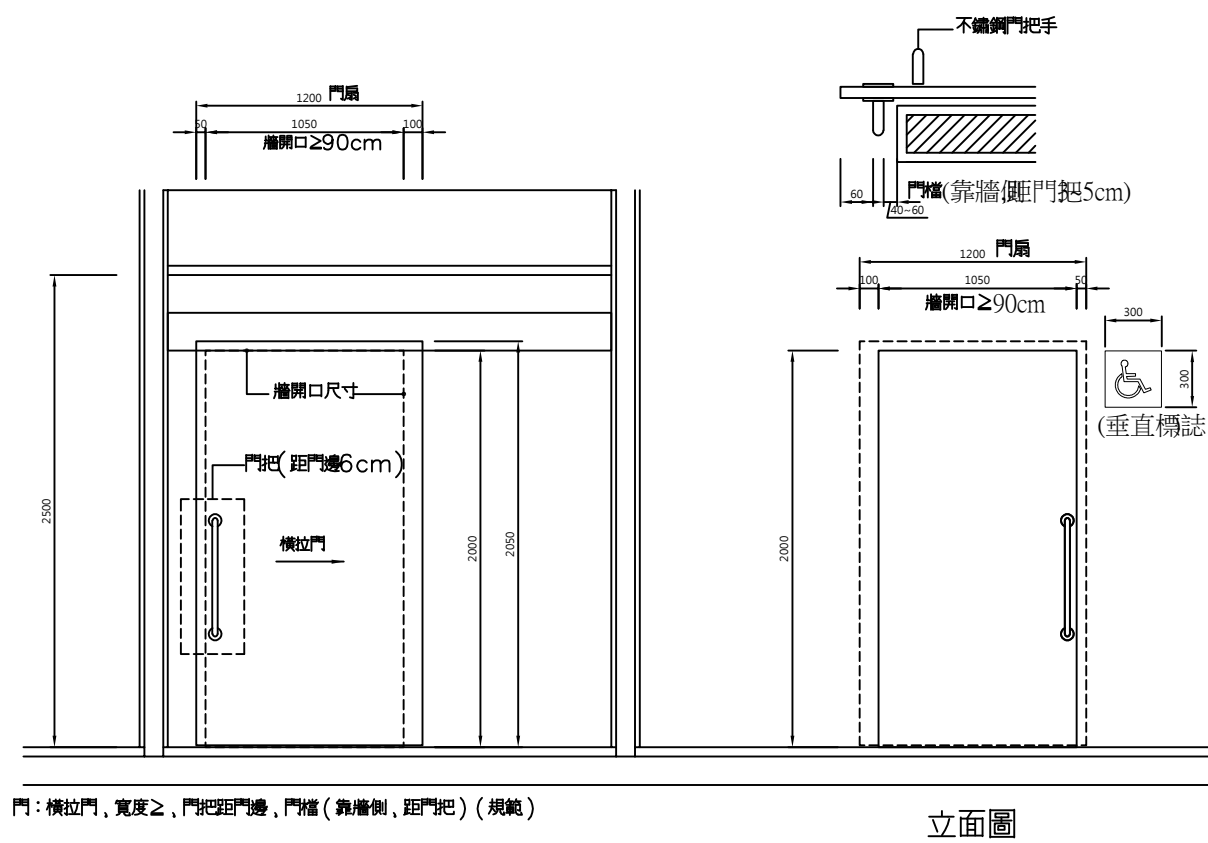


立面圖

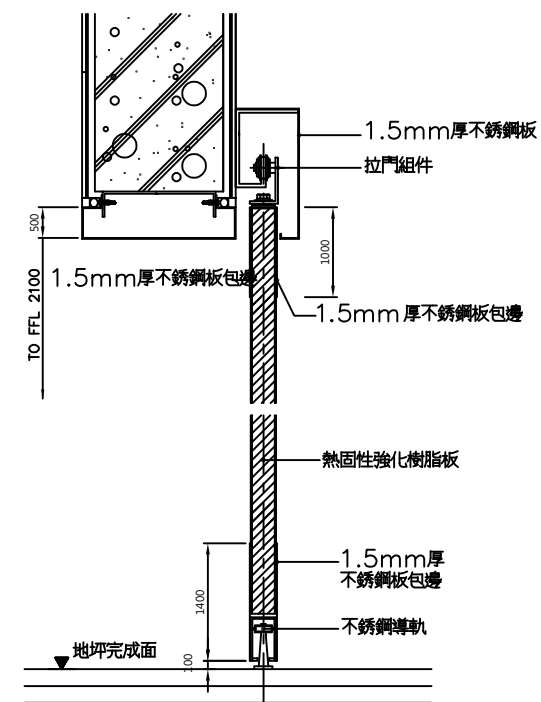

橫拉門詳圖

無障礙廁所橫拉門詳圖
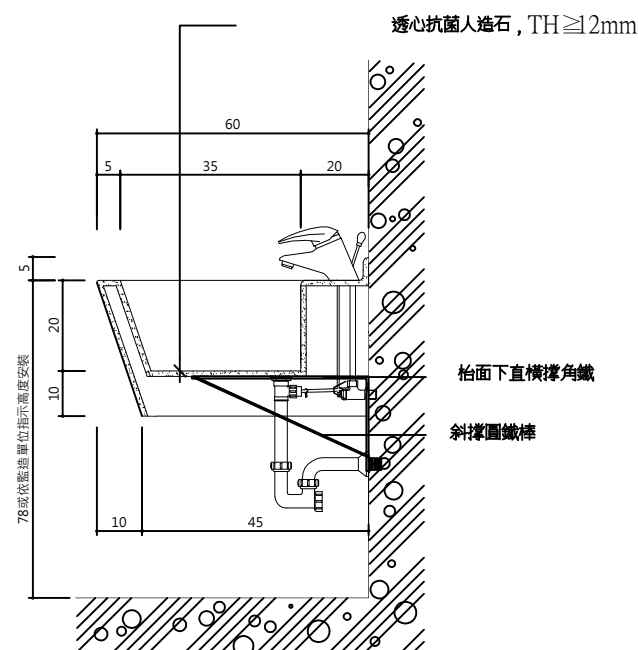
$$S=1:20$$
 $\frac{1}{-}$ 

浴廁洗手枱剖面圖

洗手枱大樣詳圖

S=1:10 UNIT=mm

$$\frac{2}{-}$$

洗手抬面施工標準:

- 1-本檯面採用厚20mm透心抗菌人造石。
- 2-深度60cm，檯面前緣長100度人造石檯面。
- 3-板材接縫時，需以同色膠拌合。
- 4-併接板材溢出之同色膠需完全乾涸後，再進行表面清除工作並於表面進行水磨處理，以確保表面平整。
- 5-表面經水磨之後，以清水擦拭，並以羊毛輪拋光，無需上蠟。
- 6-本工程材料、顏色及配件等，於施工前須經監造審核認可，並轉送業主備查後方可進場施工。
- 7-本工程由責任施工，並附上廠證明。
- 8-臉盆與檯面及檯面與牆面之接觸面，需以矽膠填縫處理。

統一企業集團桃園U-PARK智匯產業園區
建築新建工程

建築新建工程

U-PARK PROJECT

統流開發股份有限公司

UNI-PRESIDENT EXPRESS CORP. TAIPEI, TAIWAN, R.O.C.

無障礙廁所詳圖



 華興聯合建築師事務所
HWA SHIN ARCHITECTS


華興聯合
HWA SHIN ARCHITECTS


DWG. NO.	0721B-ARB-D09023
----------	------------------

JOB NO. 0721B

ISSUE NO.	
-----------	--

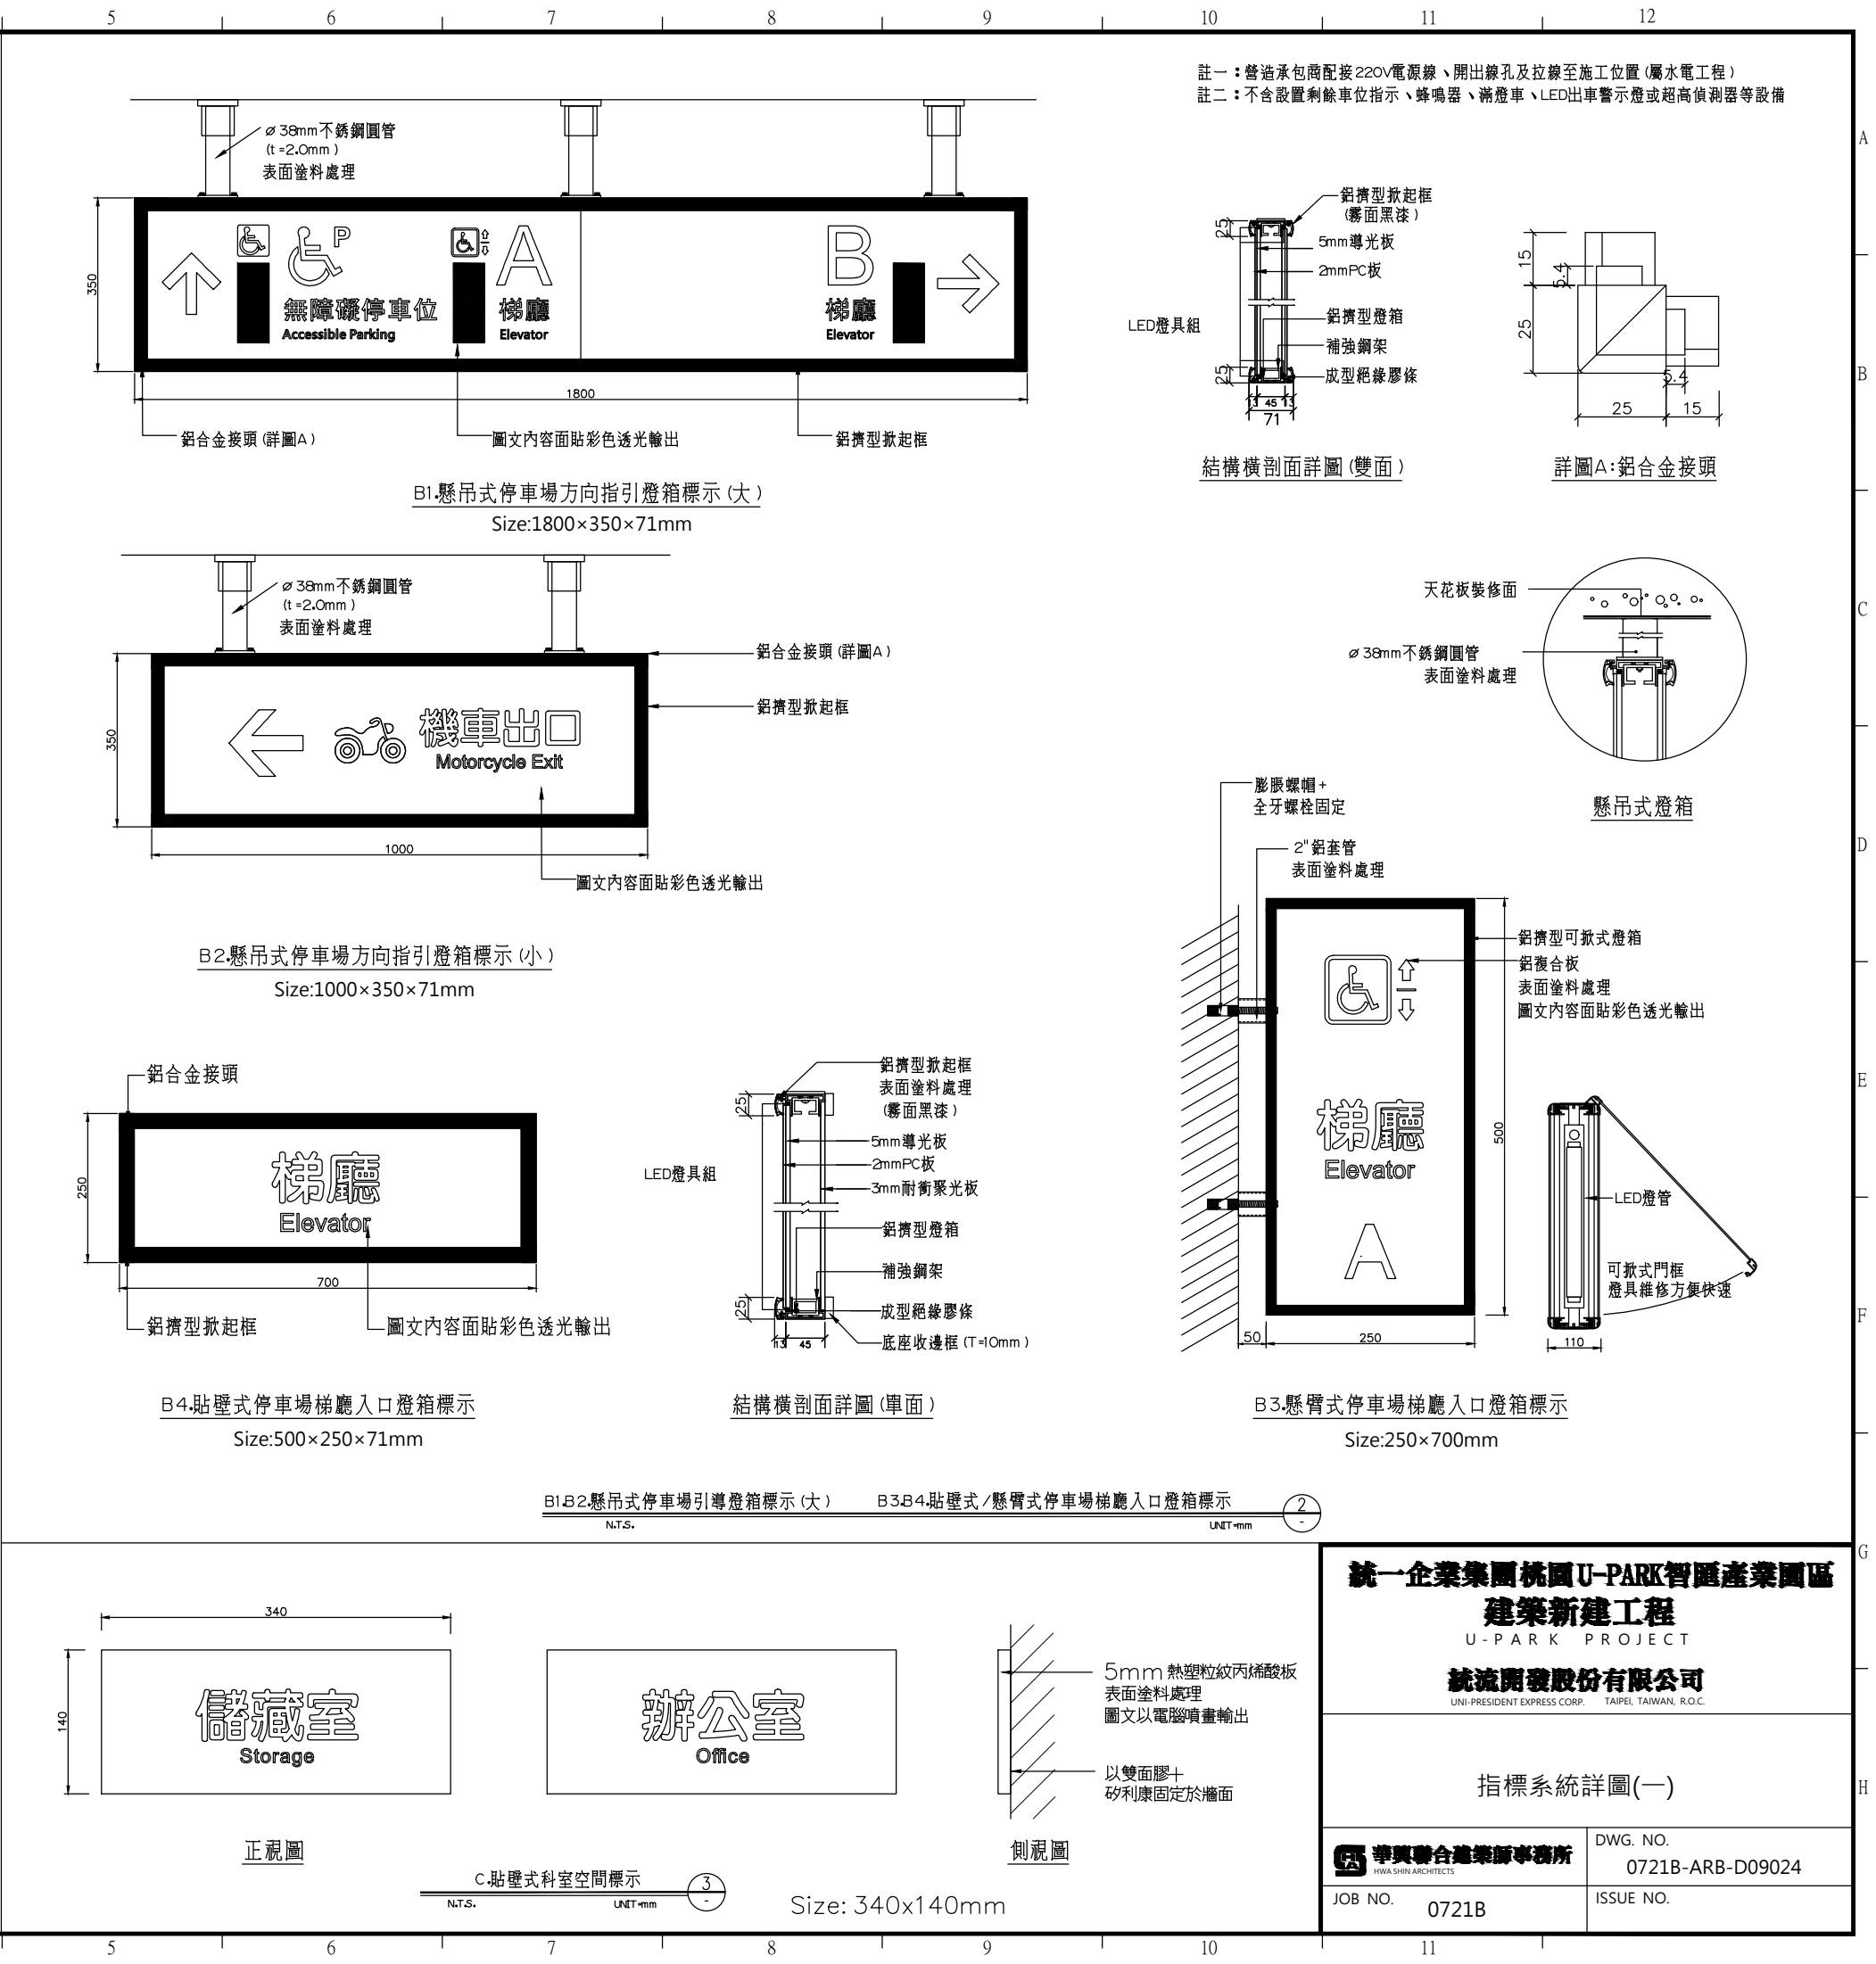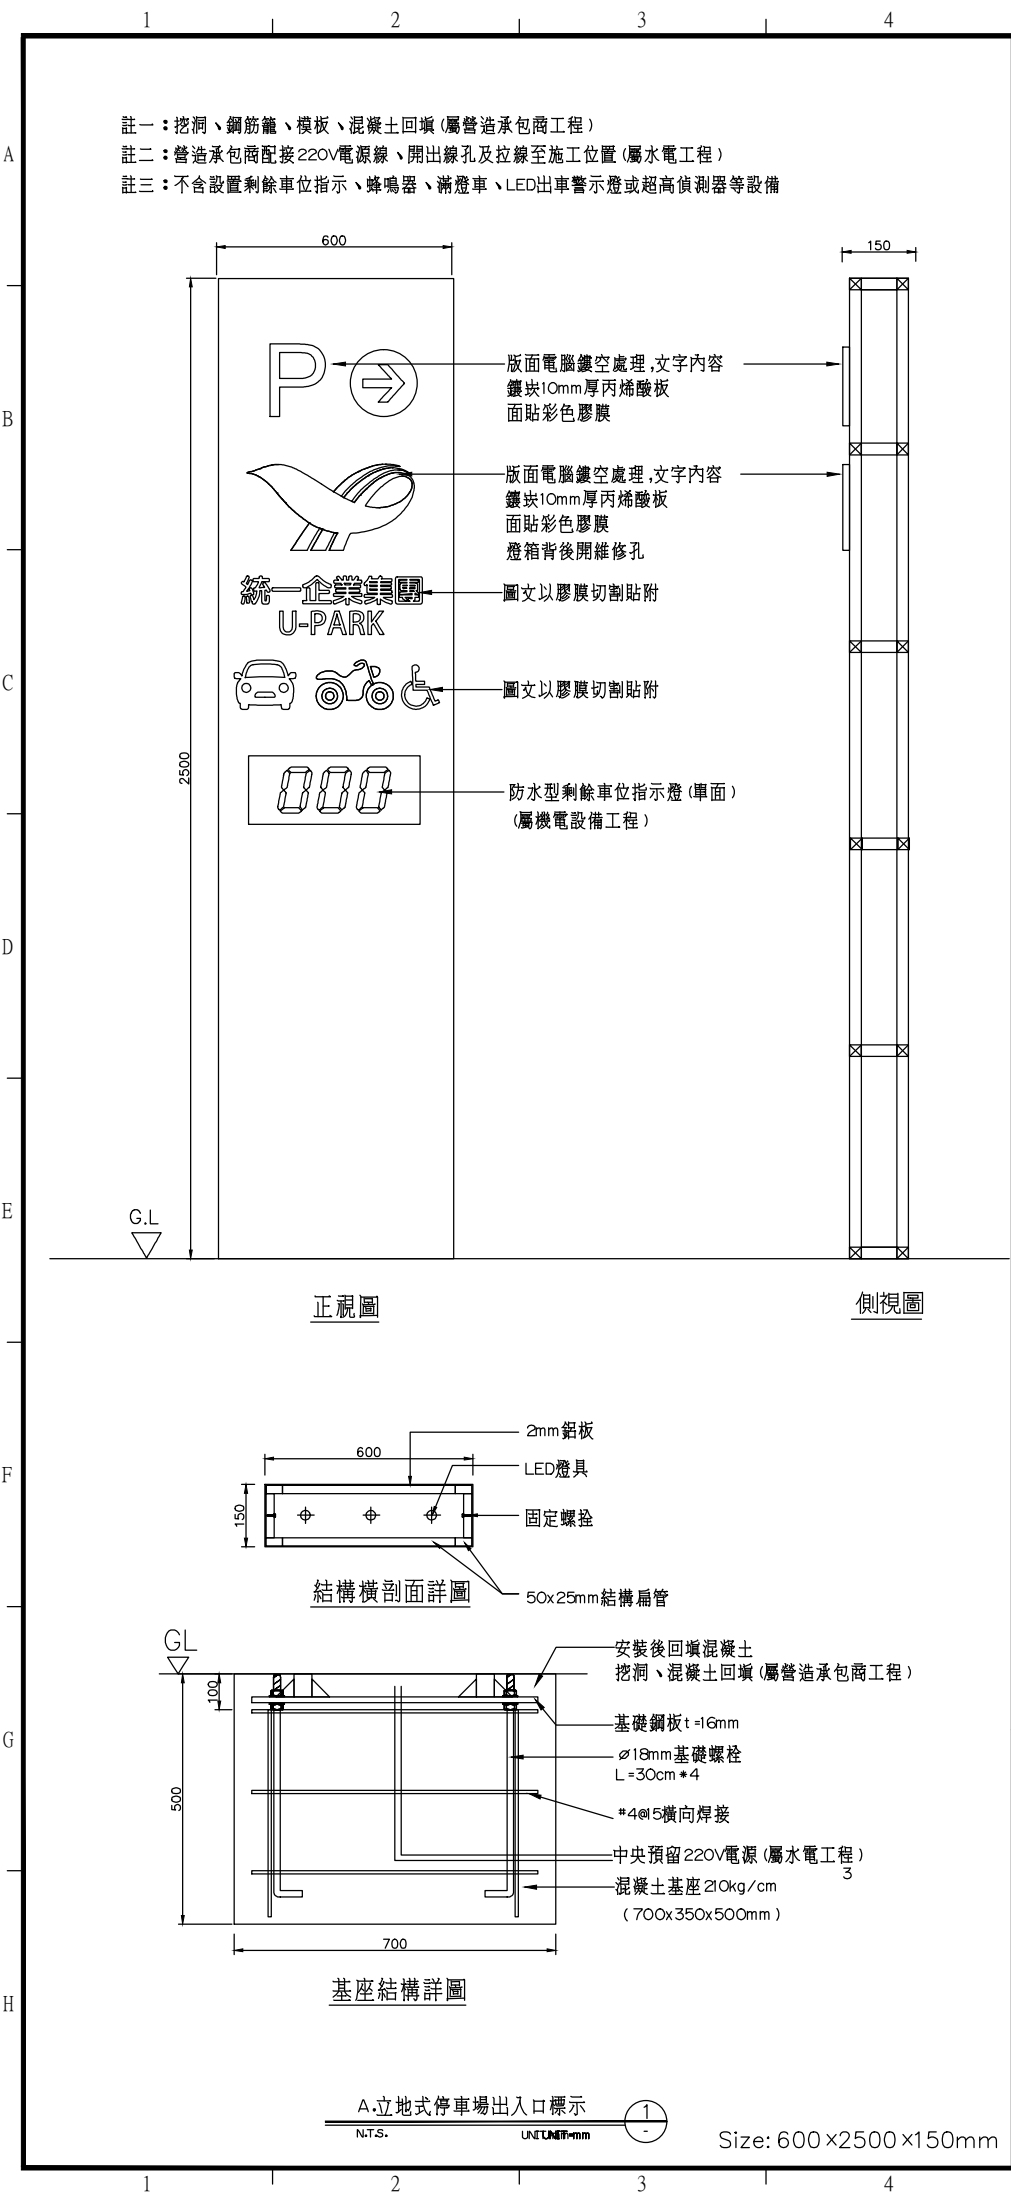

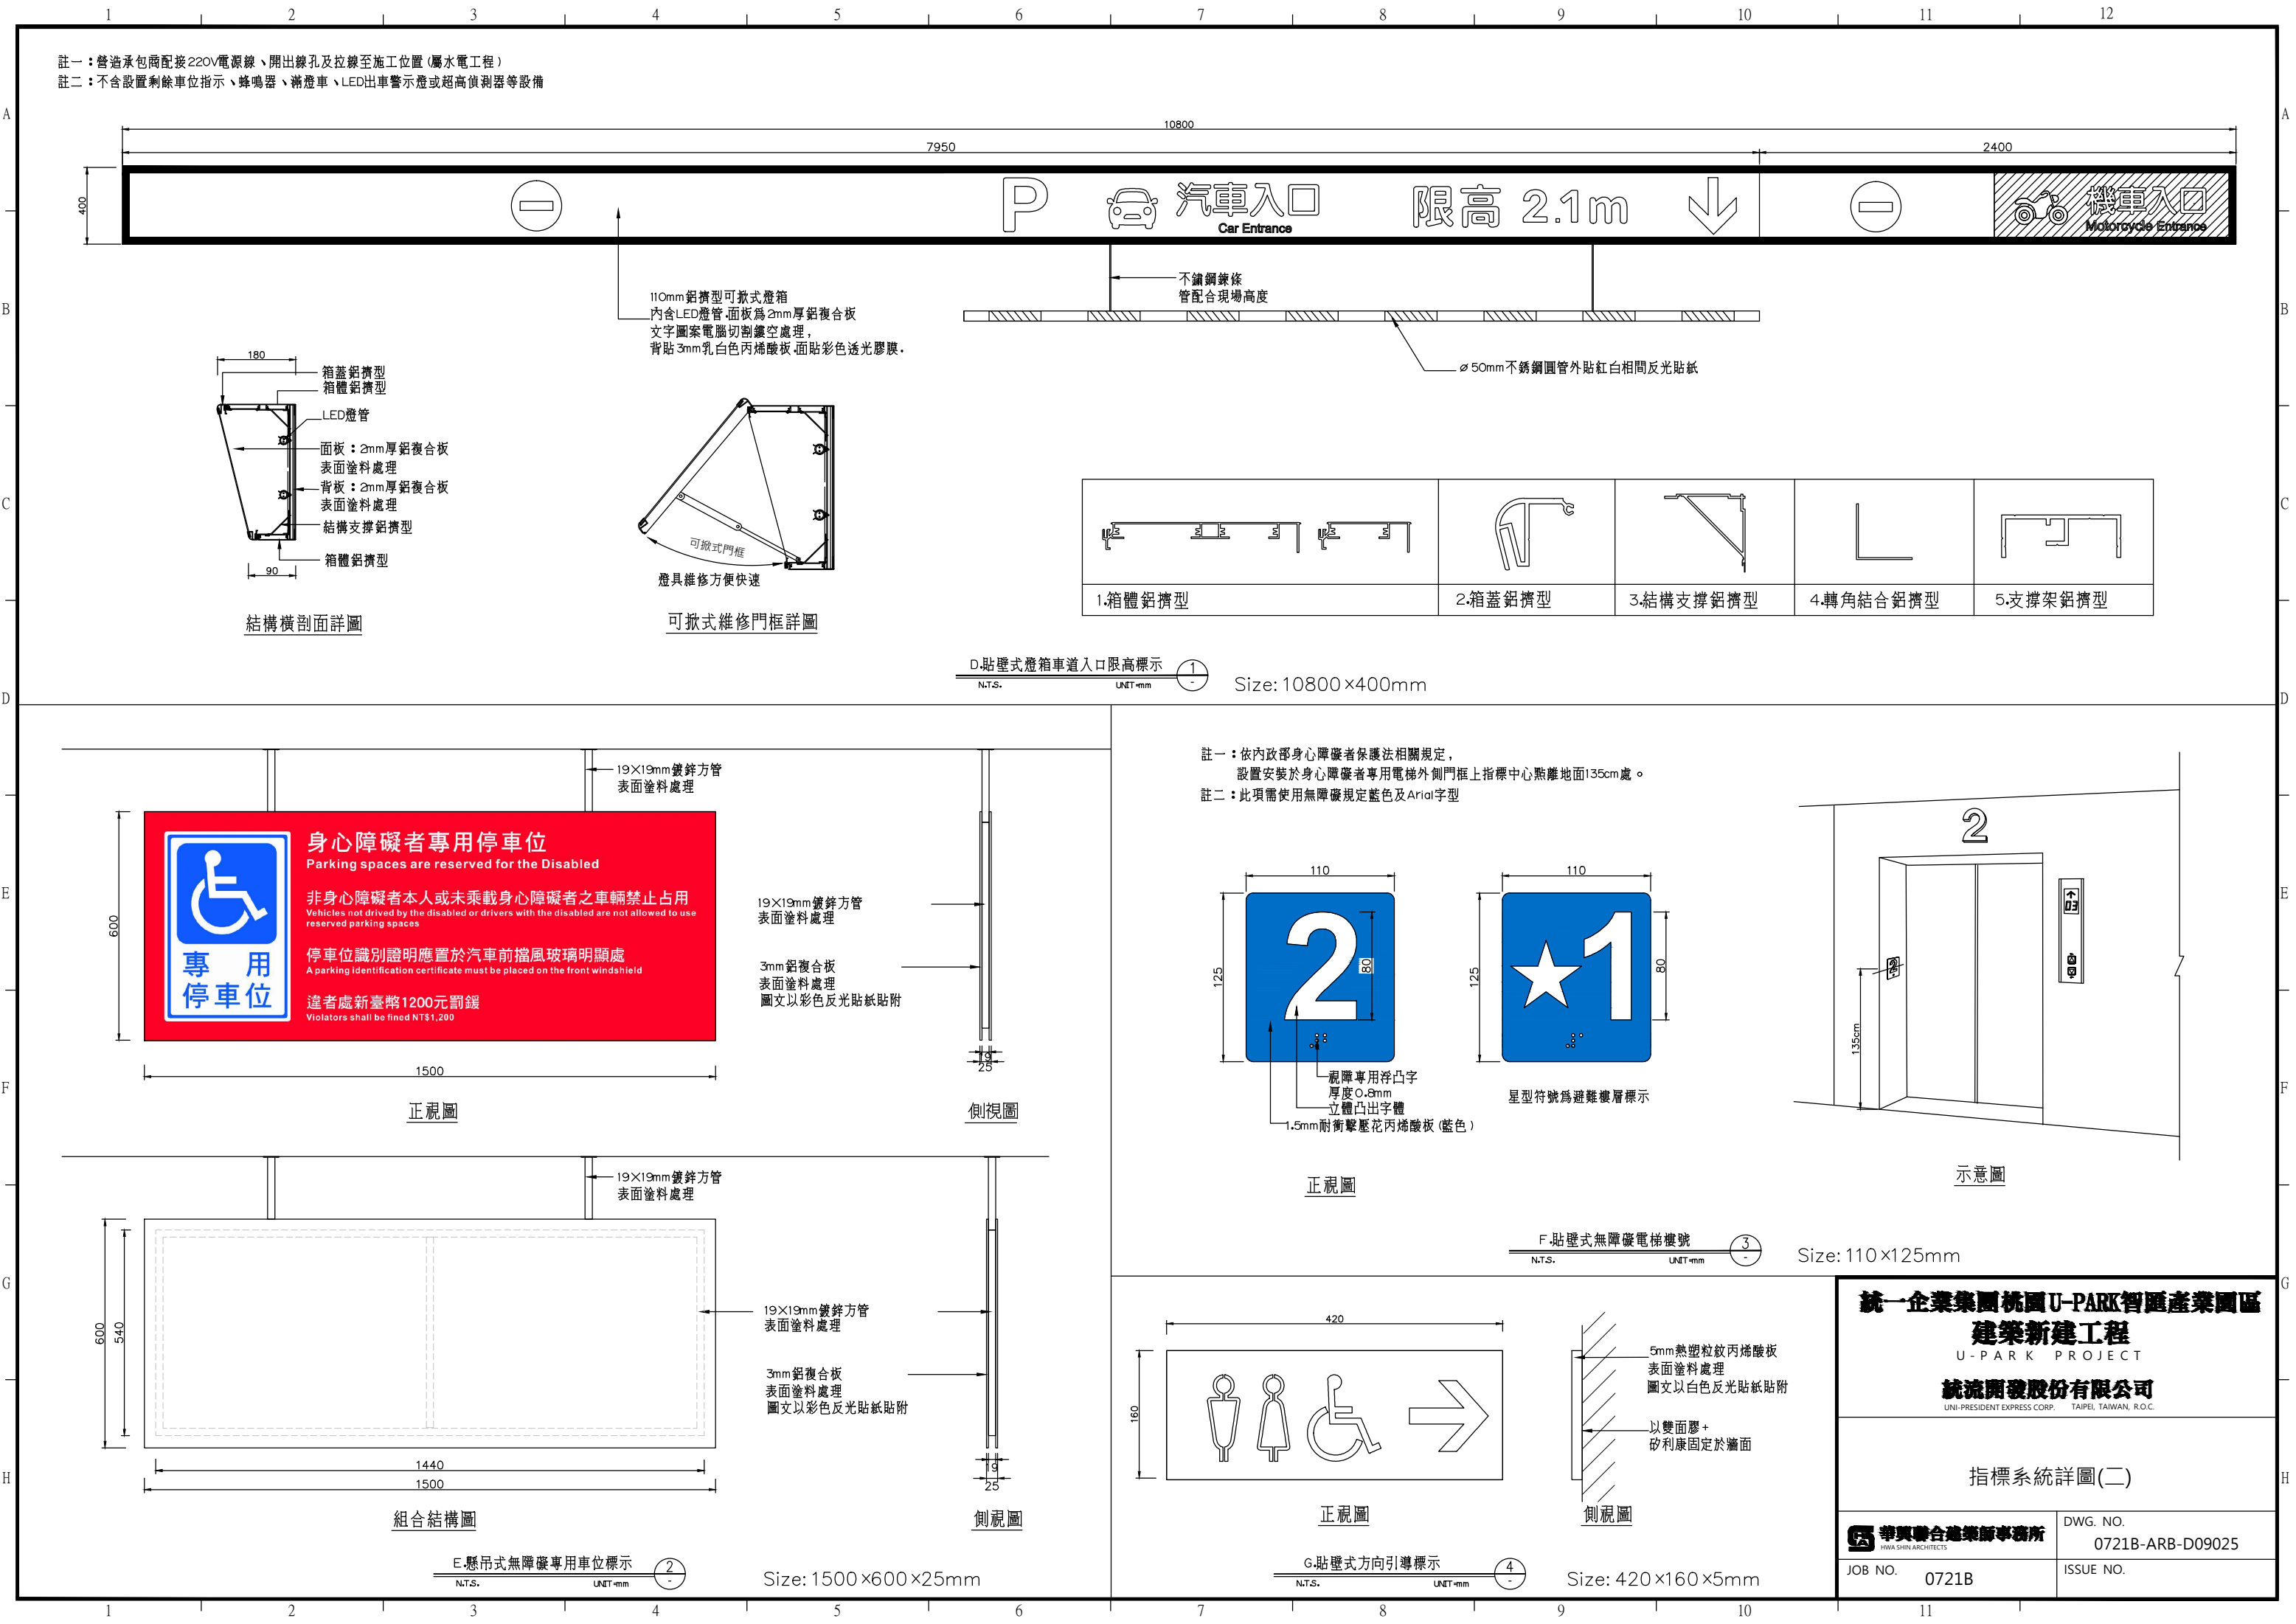

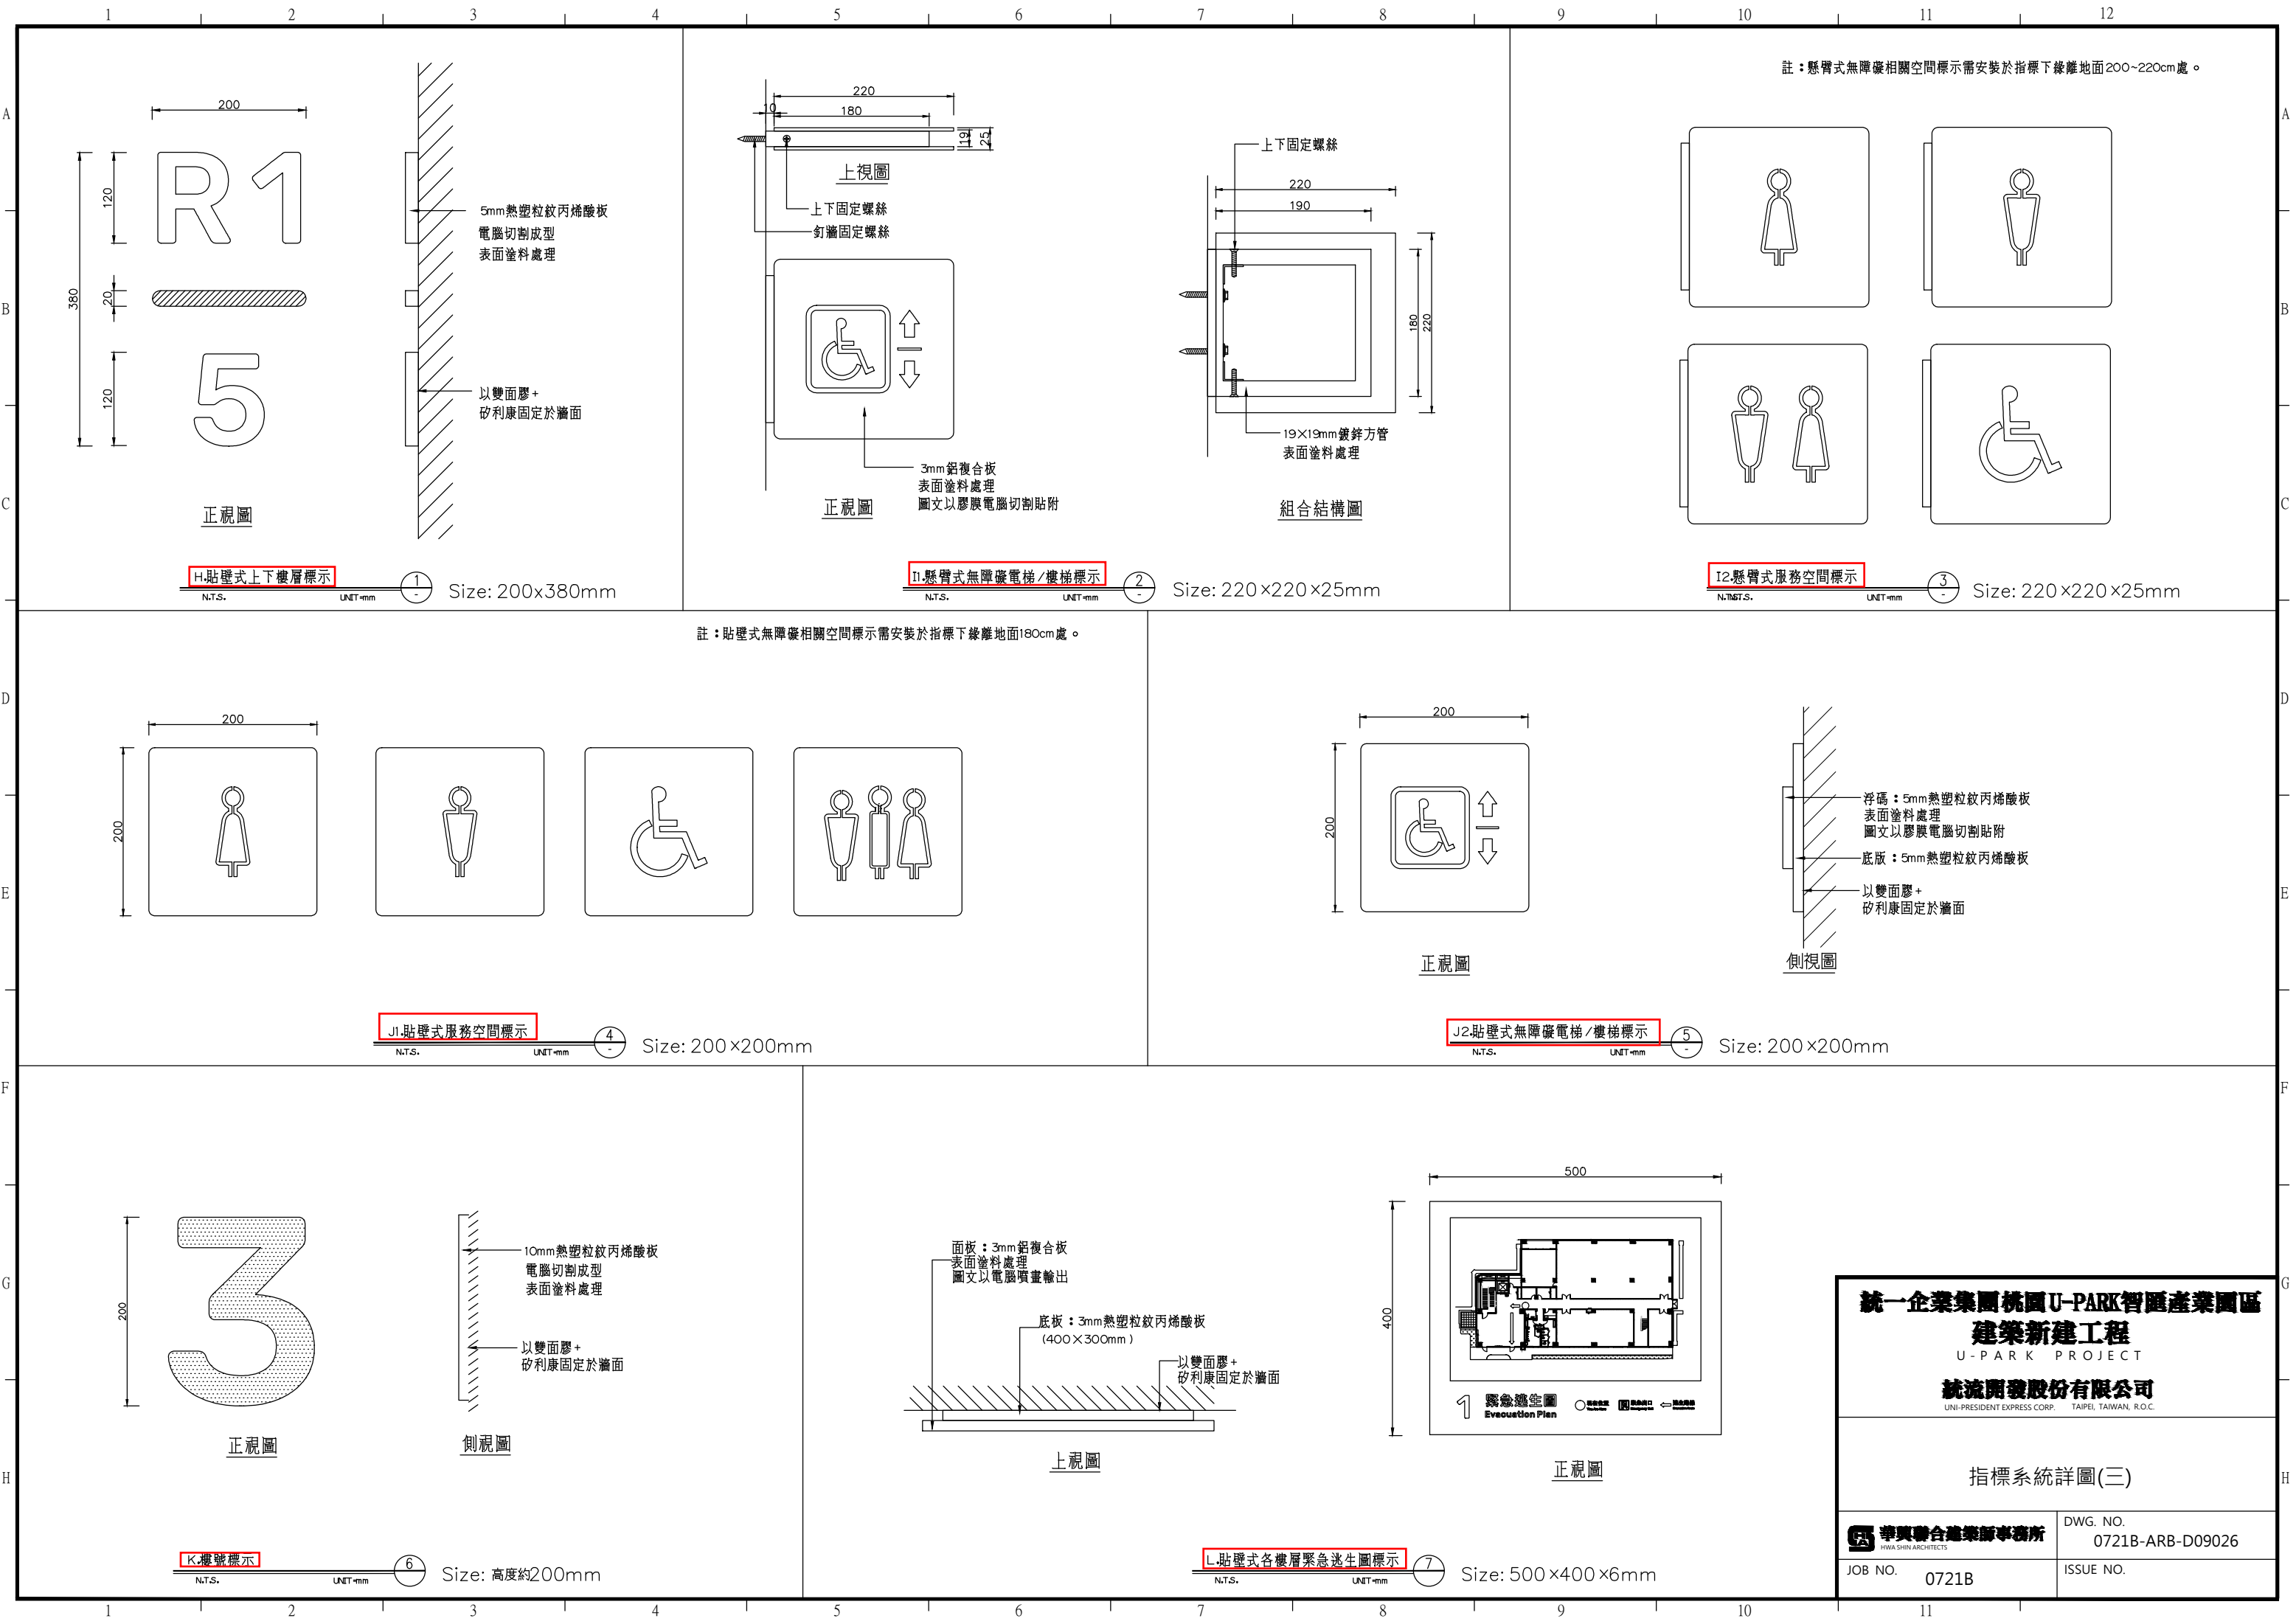

註：懸臂式無障礙相關空間標示需安裝於指標下緣離地面200~220cm處。

註：貼壁式無障礙相關空間標示需安裝於指標下緣離地面180cm處。

統一企業集團桃園U-PARK智匯產業園區
建築新建工程
U-PARK PROJECT
統流開發股份有限公司
UNI-PRESIDENT EXPRESS CORP. TAIPEI, TAIWAN, R.O.C.


指標系統詳圖(三)

華興聯合建築師事務所
HWA SHIN ARCHITECTS

DWG. NO.
0721B-ARB-D09026

JOB NO.
0721B

ISSUE NO.

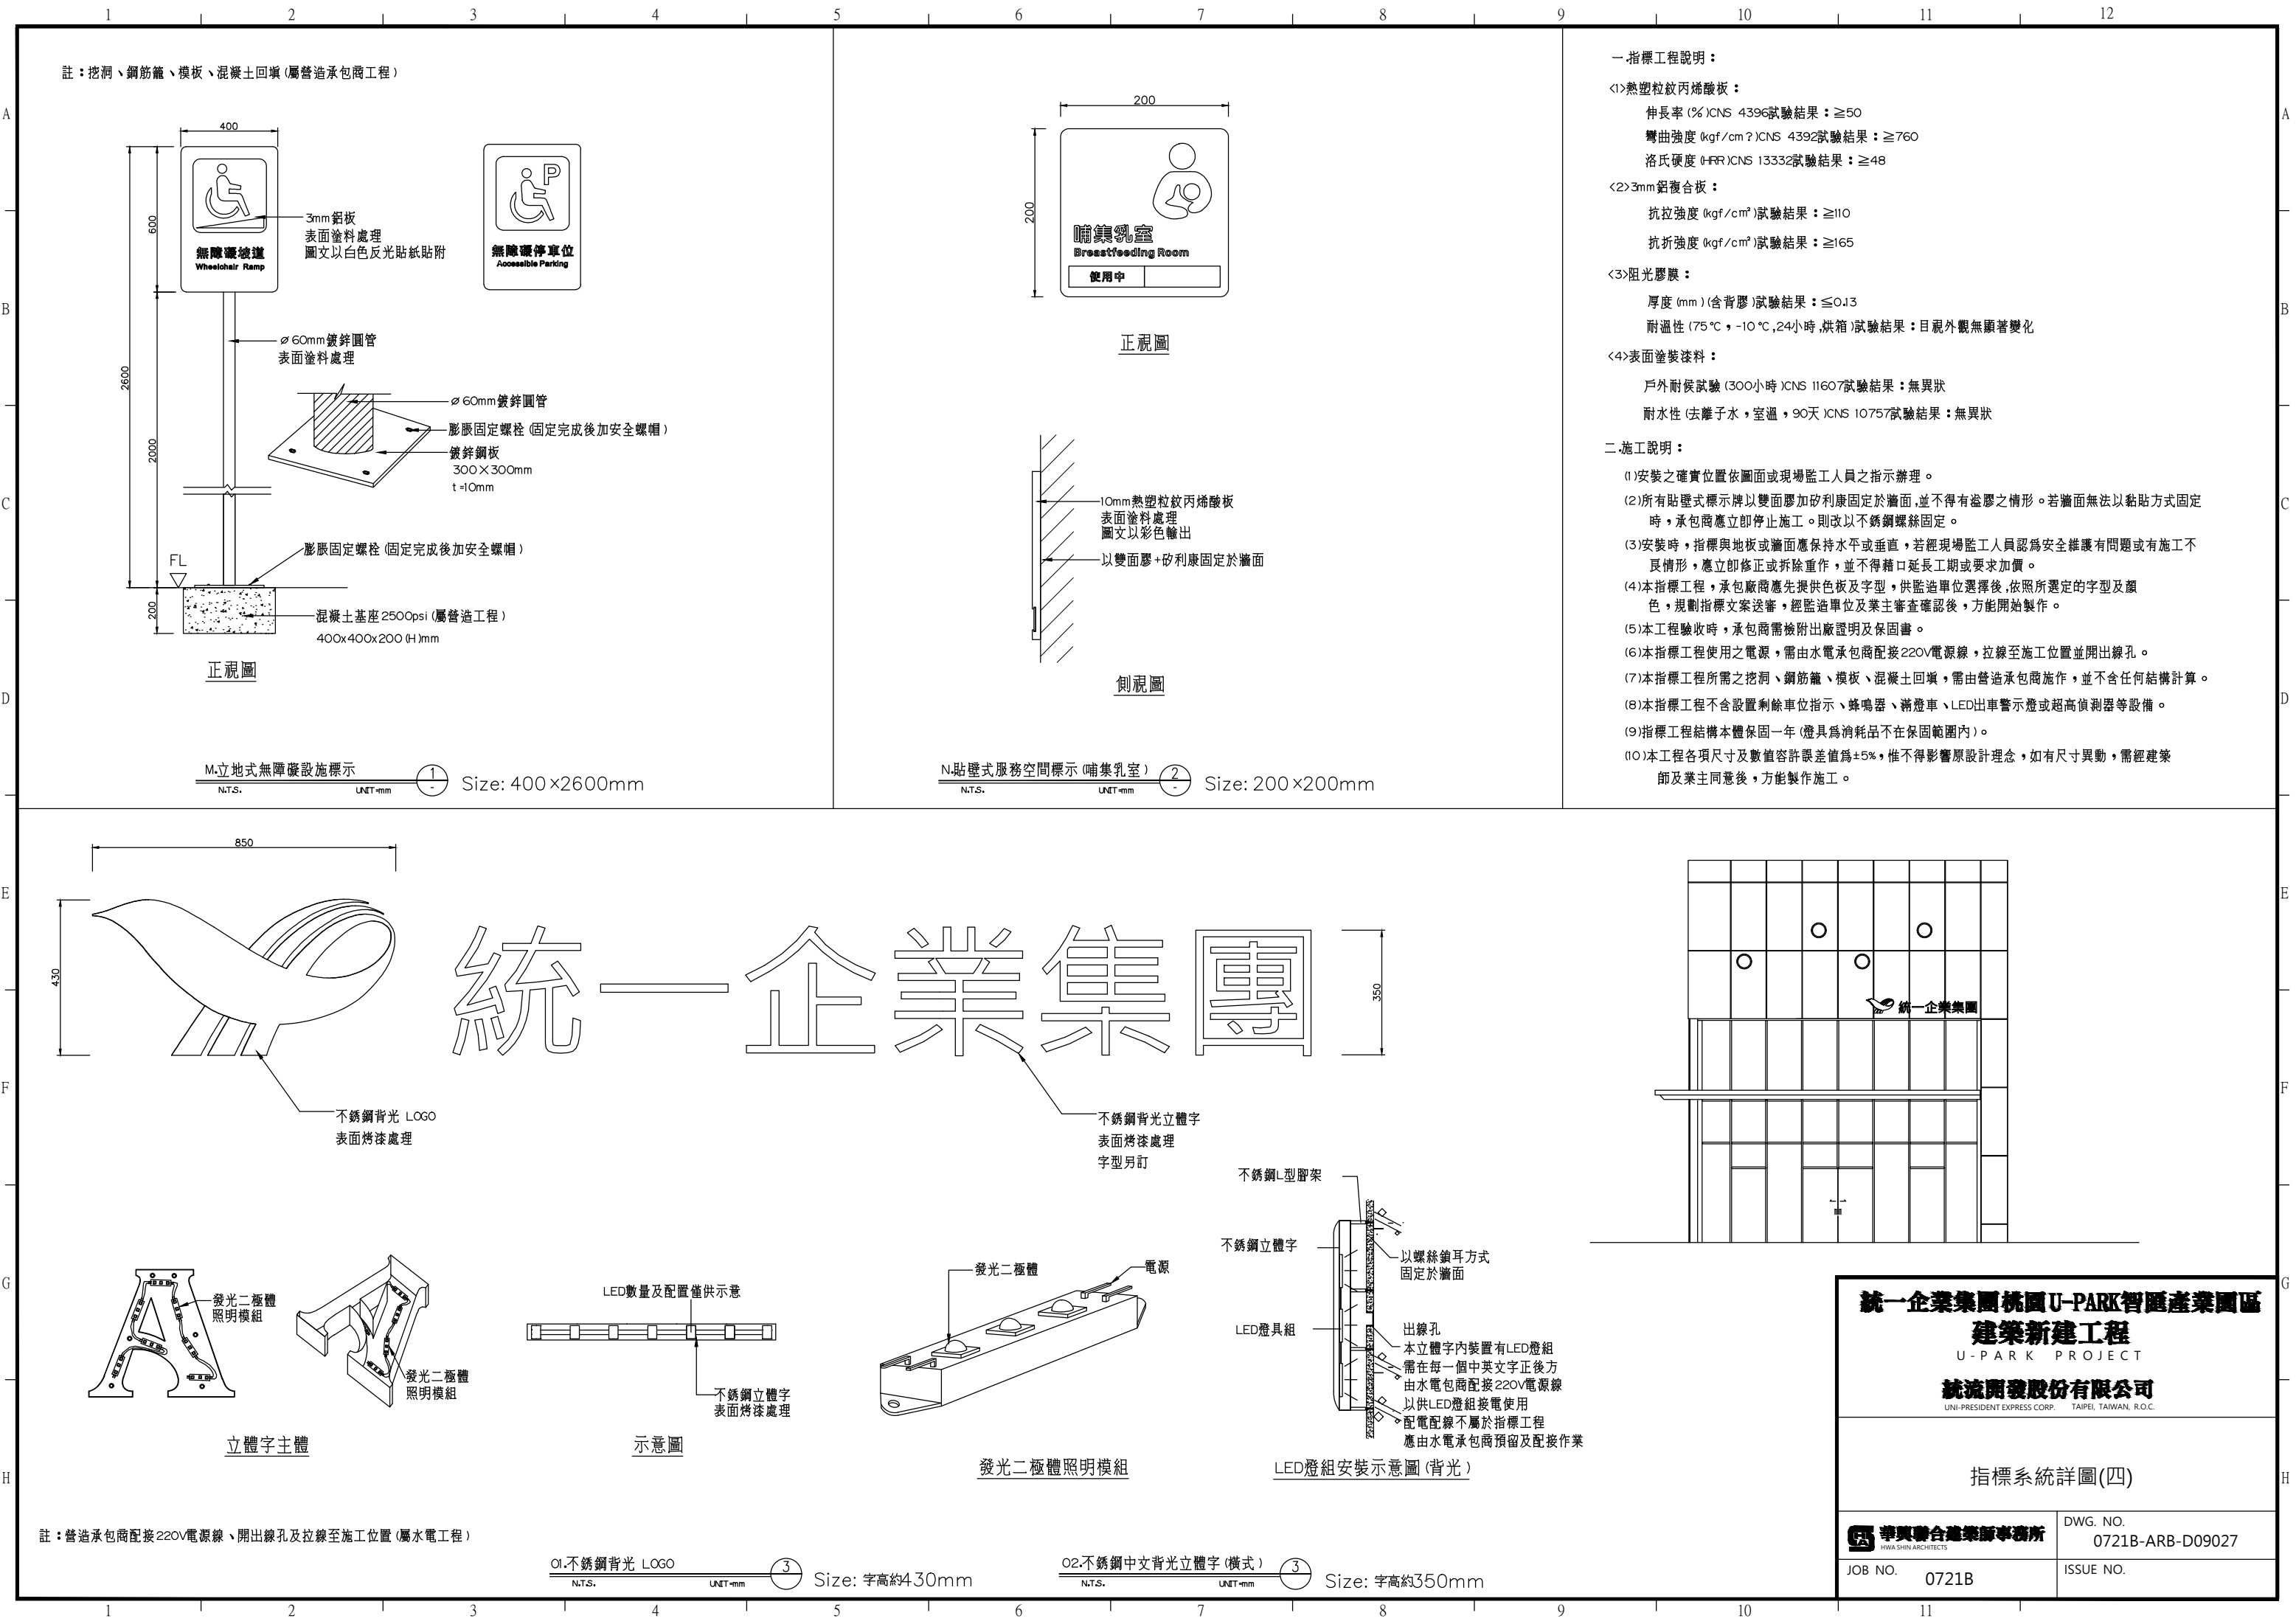

一.指標工程說明：

<1>熱塑粒紋丙烯酸板：

伸長率(%)JCNS 4396試驗結果：≥50

彎曲強度(kgf/cm²)JCNS 4392試驗結果：≥760

洛氏硬度(HRR)JCNS 13332試驗結果：≥48

<2>3mm 鋁複合板：

抗拉強度(kgf/cm²)試驗結果：≥110

抗折強度(kgf/cm²)試驗結果：≥165

<3>阻光膠膜：

厚度(mm)(含背膠)試驗結果：≤0.13

耐溫性(75℃、-10℃,24小時,烘箱)試驗結果：目視外觀無顯著變化

<4>表面塗裝漆料：

戶外耐候試驗(300小時)JCNS 11607試驗結果：無異狀

耐水性(去離子水,室溫,90天)JCNS 10757試驗結果：無異狀

二.施工說明：

(1)安裝之確實位置依圖面或現場監工人員之指示辦理。

(2)所有貼壁式標示牌以雙面膠加矽利康固定於牆面,並不得有溢膠之情形。若牆面無法以黏貼方式固定時,承包商應立即停止施工。則改以不銹鋼螺絲固定。

(3)安裝時,指標與地板或牆面應保持水平或垂直,若經現場監工人員認為安全維護有問題或有施工不良情形,應立即修正或拆除重作,並不得藉口延長工期或要求加價。

(4)本指標工程,承包廠商應先提供色板及字型,供監造單位選擇後,依照所選定的字型及顏色,規劃指標文案送審,經監造單位及業主審查確認後,方能開始製作。

(5)本工程驗收時,承包商需檢附出廠證明及保固書。


(6)本指標工程使用之電源,需由水電承包商配接220V電源線,拉線至施工位置並開出線孔。

(7)本指標工程所需之挖洞、鋼筋籠、模板、混凝土回填,需由營造承包商施作,並不含任何結構計算。

(8)本指標工程不含設置剩餘車位指示、蜂鳴器、滿燈車、LED出車警示燈或超高偵測器等設備。

(9)指標工程結構本體保固一年(燈具為消耗品不在保固範圍內)。

(10)本工程各項尺寸及數值容許誤差值為±5%,惟不得影響原設計理念,如有尺寸異動,需經建築師及業主同意後,方能製作施工。

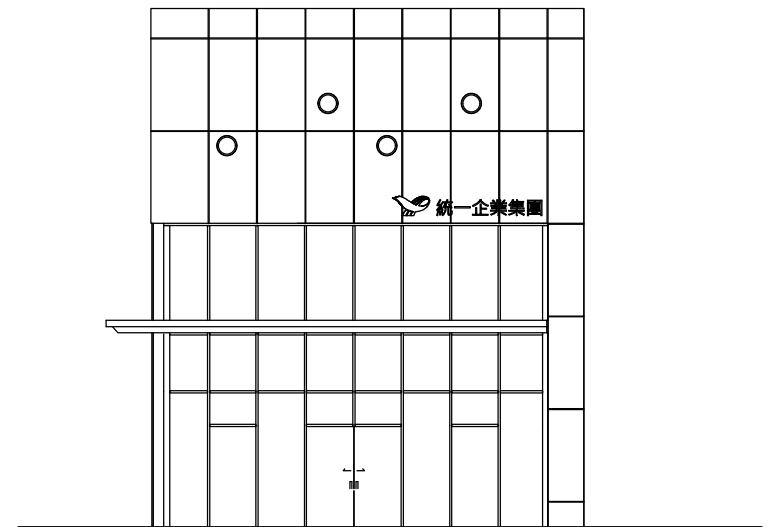

**統一企業集團桃園U-PARK智匯產業園區
建築新建工程**
U-PARK PROJECT
統流開發股份有限公司
UNI-PRESIDENT EXPRESS CORP. TAIPEI, TAIWAN, R.O.C.


指標系統詳圖(四)

華興聯合建築師事務所
HWA SHIN ARCHITECTS

DWG. NO.
0721B-ARB-D09027


JOB NO.
0721B

ISSUE NO.

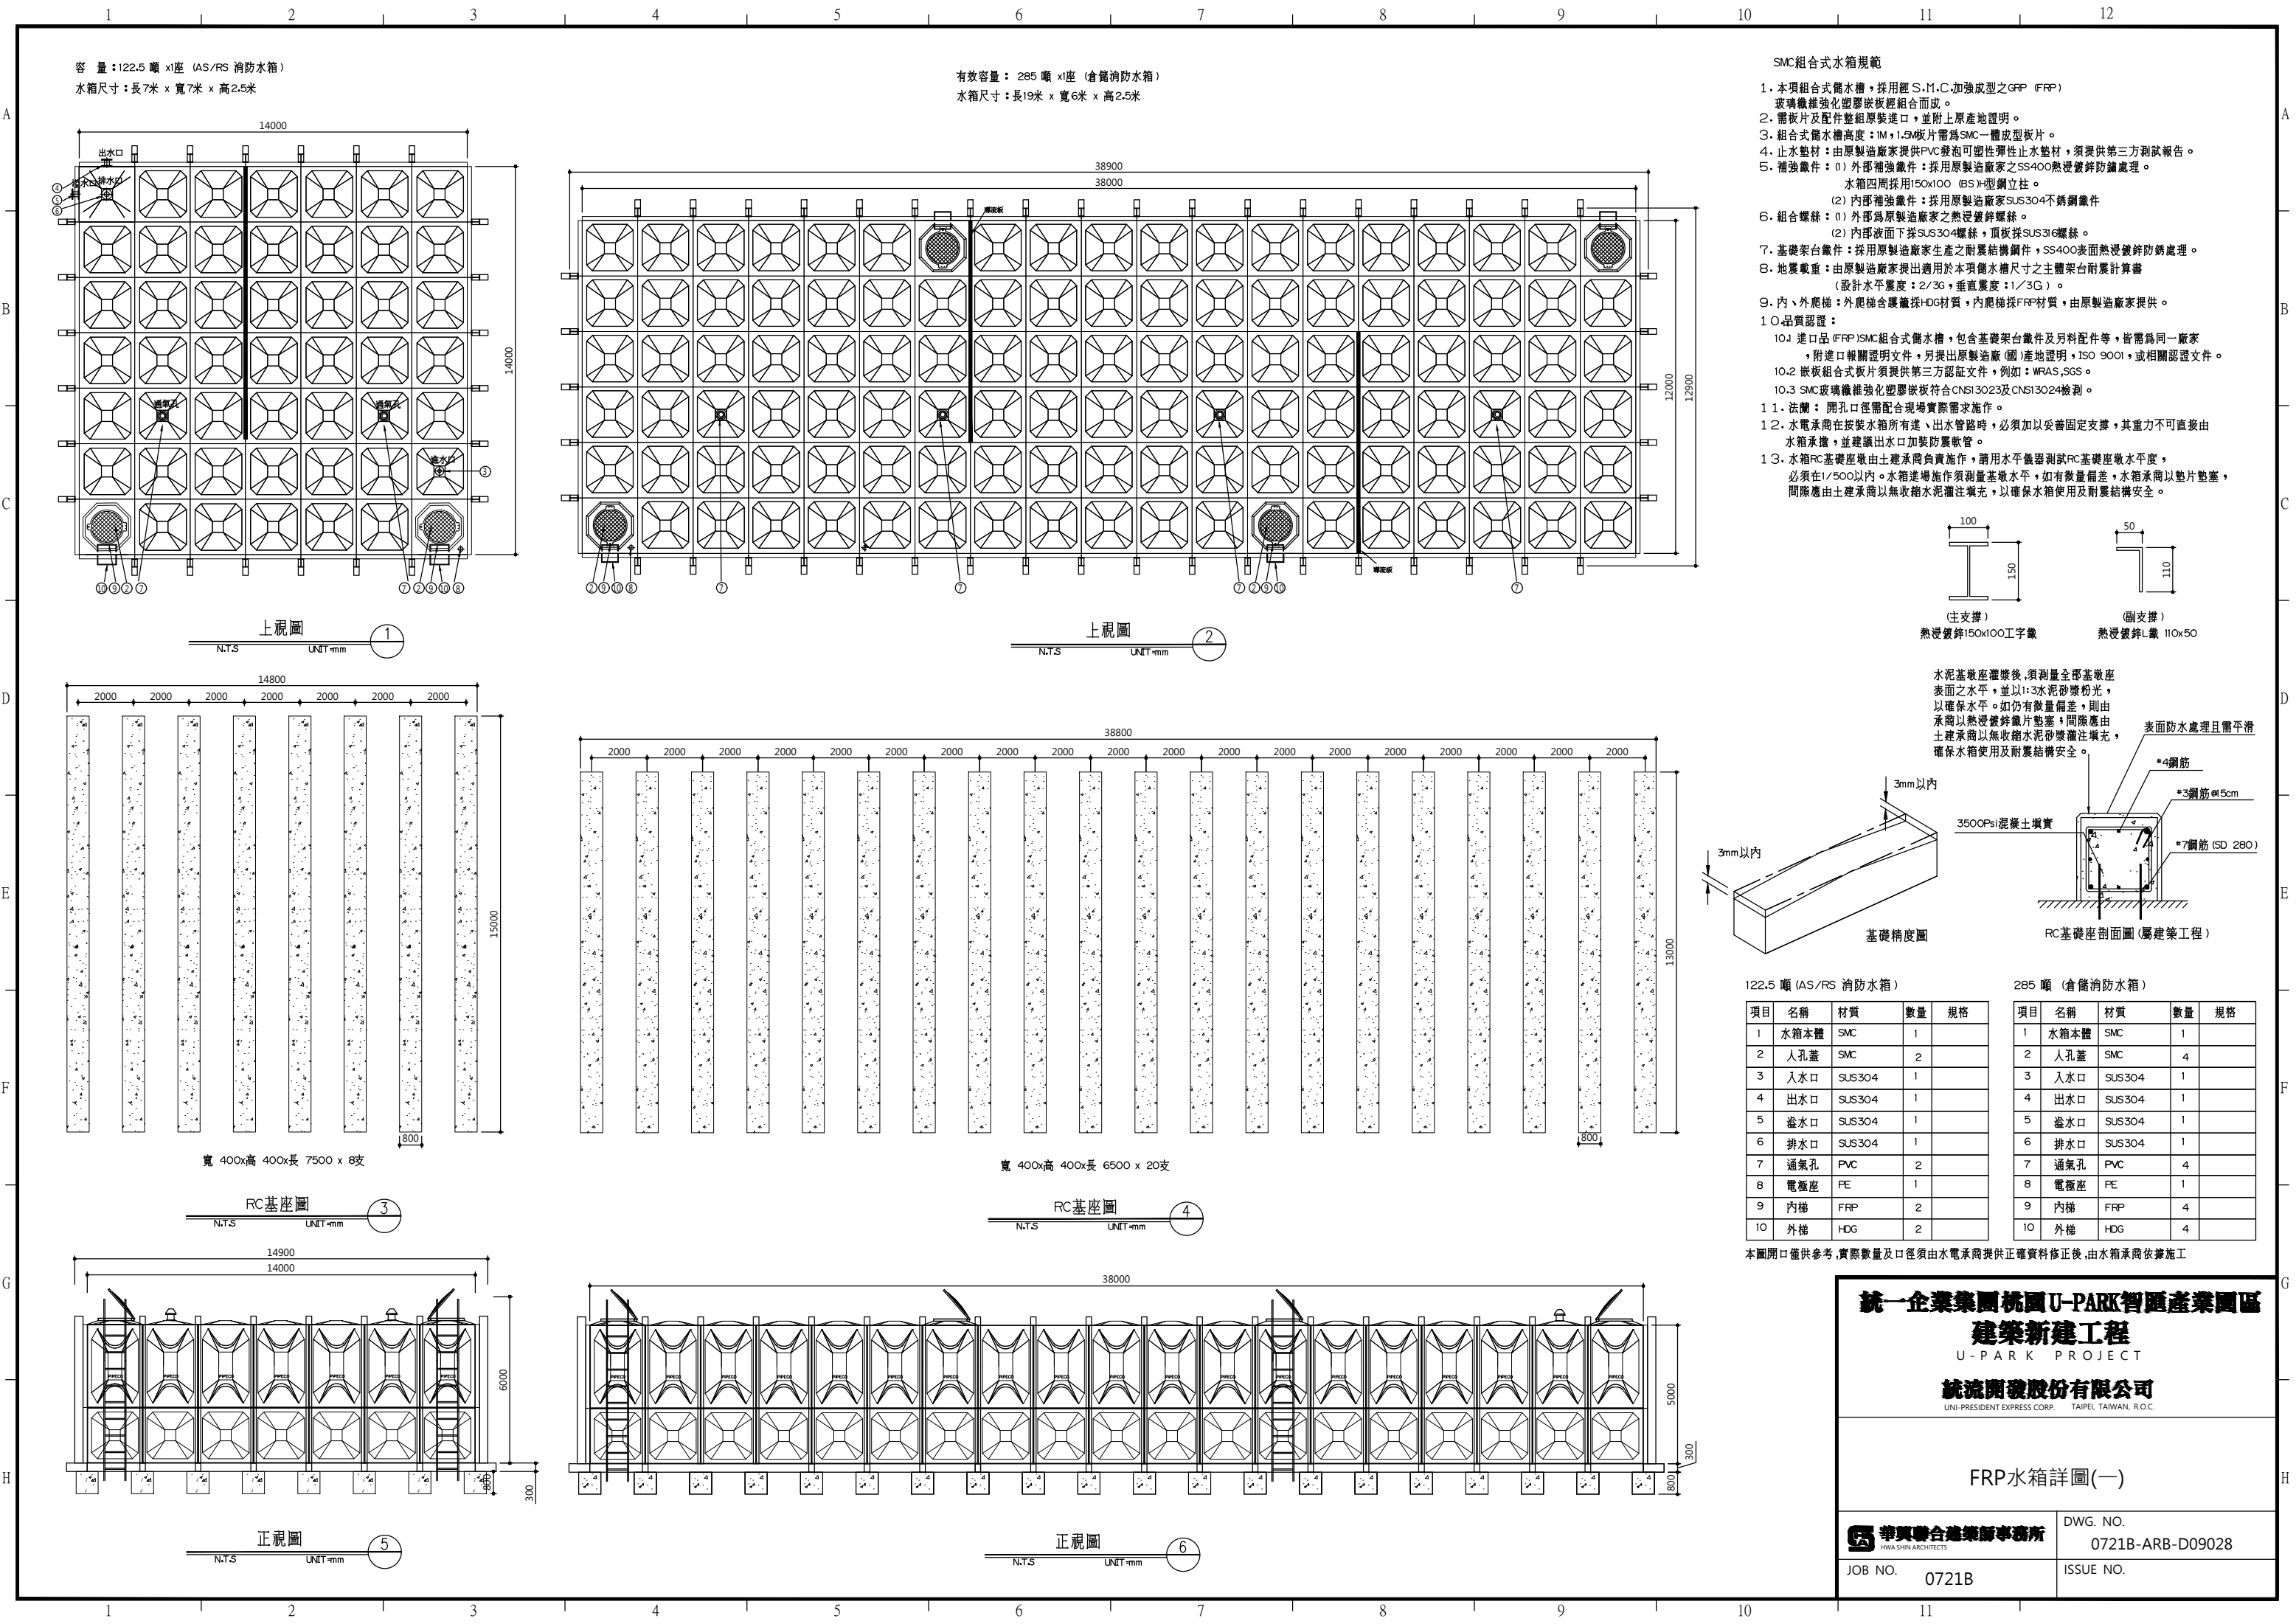


SMC組合式水箱規範

- 1. 本項組合式儲水槽，採用經 S.M.C.加強成型之 FRP (FRP) 玻璃纖維強化塑膠板經組合而成。
- 2. 需板片及配件整組原裝進口，並附上原產地證明。
- 3. 組合式儲水槽高度：1M，1.5M板片需為 SMC一體成型板片。
- 4. 止水墊材：由原製造廠家提供PVC發泡可塑性彈性止水墊材，須提供第三方測試報告。
- 5. 補強鐵件：(1) 外部補強鐵件：採用原製造廠家之SS400熱浸鍍鋅防銹處理。
水箱四周採用150x100 (8S)I-型鋼立柱。
(2) 內部補強鐵件：採用原製造廠家SUS304不銹鋼鐵件
- 6. 組合螺絲：(1) 外部為原製造廠家之熱浸鍍鋅螺絲。
(2) 內部液面下採SUS304螺絲，頂板採SUS316螺絲。
- 7. 基礎架台鐵件：採用原製造廠家生產之耐震結構鋼件，SS400表面熱浸鍍鋅防銹處理。
- 8. 地震載重：由原製造廠家提出適用於本項儲水槽尺寸之主體架台耐震計算書 (設計水平震度：2/3G，垂直震度：1/3G)。
- 9. 內、外爬梯：外爬梯含護籠採HDG材質，內爬梯採FRP材質，由原製造廠家提供。
- 10.品質認證：
 - 10.1 進口品 (FRP) SMC組合式儲水槽，包含基礎架台鐵件及另料配件等，皆需為同一廠家，附進口報關證明文件，另提出原製造廠 (國)產地證明，ISO 9001，或相關認證文件。
 - 10.2 嵌板組合式板片須提供第三方認證文件，例如：WRAS, SGS。
 - 10.3 SMC玻璃纖維強化塑膠板符合CNS13023及CNS13024檢測。
- 11. 法蘭：開口口徑需配合現場實際需求施作。
- 12. 水電承商在安裝水箱所有進、出水管路時，必須加以妥善固定支撐，其重力不可直接由水箱承擔，並建議出水管口加裝防震軟管。
- 13. 水箱RC基礎座墩由土建承商負責施作，請用水準儀器測試RC基礎座墩水平度，必須在1/500以內。水箱進場施作須測量基礎水平，如有數量偏差，水箱承商以墊片墊塞，間隙應由土建承商以無收縮水泥漿灌注填充，以確保水箱使用及耐震結構安全。

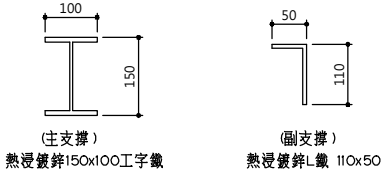

水泥基礎座灌漿後，須測量全部基礎座表面之水平，並以1:3水泥砂漿粉光，以確保水平。如仍有數量偏差，則由承商以熱浸鍍鋅鐵片墊塞，間隙應由土建承商以無收縮水泥砂漿灌注填充，確保水箱使用及耐震結構安全。

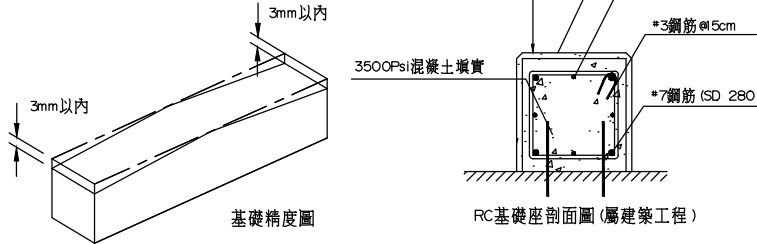

122.5 噸 (AS/RS 消防水箱)

項目	名稱	材質	數量	規格
1	水箱本體	SMC	1	
2	人孔蓋	SMC	2	
3	入水口	SUS304	1	
4	出水口	SUS304	1	
5	溢水口	SUS304	1	
6	排水口	SUS304	1	
7	通氣孔	PVC	2	
8	電極座	FE	1	
9	內梯	FRP	2	
10	外梯	HDG	2	

285 噸 (倉儲消防水箱)

項目	名稱	材質	數量	規格
1	水箱本體	SMC	1	
2	人孔蓋	SMC	4	
3	入水口	SUS304	1	
4	出水口	SUS304	1	
5	溢水口	SUS304	1	
6	排水口	SUS304	1	
7	通氣孔	PVC	4	
8	電極座	FE	1	
9	內梯	FRP	4	
10	外梯	HDG	4	

本圖開口僅供參考，實際數量及口徑須由水電承商提供正確資料修正後，由水箱承商依據施工

統一企業集團桃園U-PARK智匯產業園區
建築新建工程
U-PARK PROJECT
統流開發股份有限公司
UNI-PRESIDENT EXPRESS CORP. TAIPEI, TAIWAN, R.O.C.


FRP水箱詳圖(一)

華興聯合建築師事務所
HWA SHIN ARCHITECTS

DWG. NO.
0721B-ARB-D09028


JOB NO.
0721B

ISSUE NO.

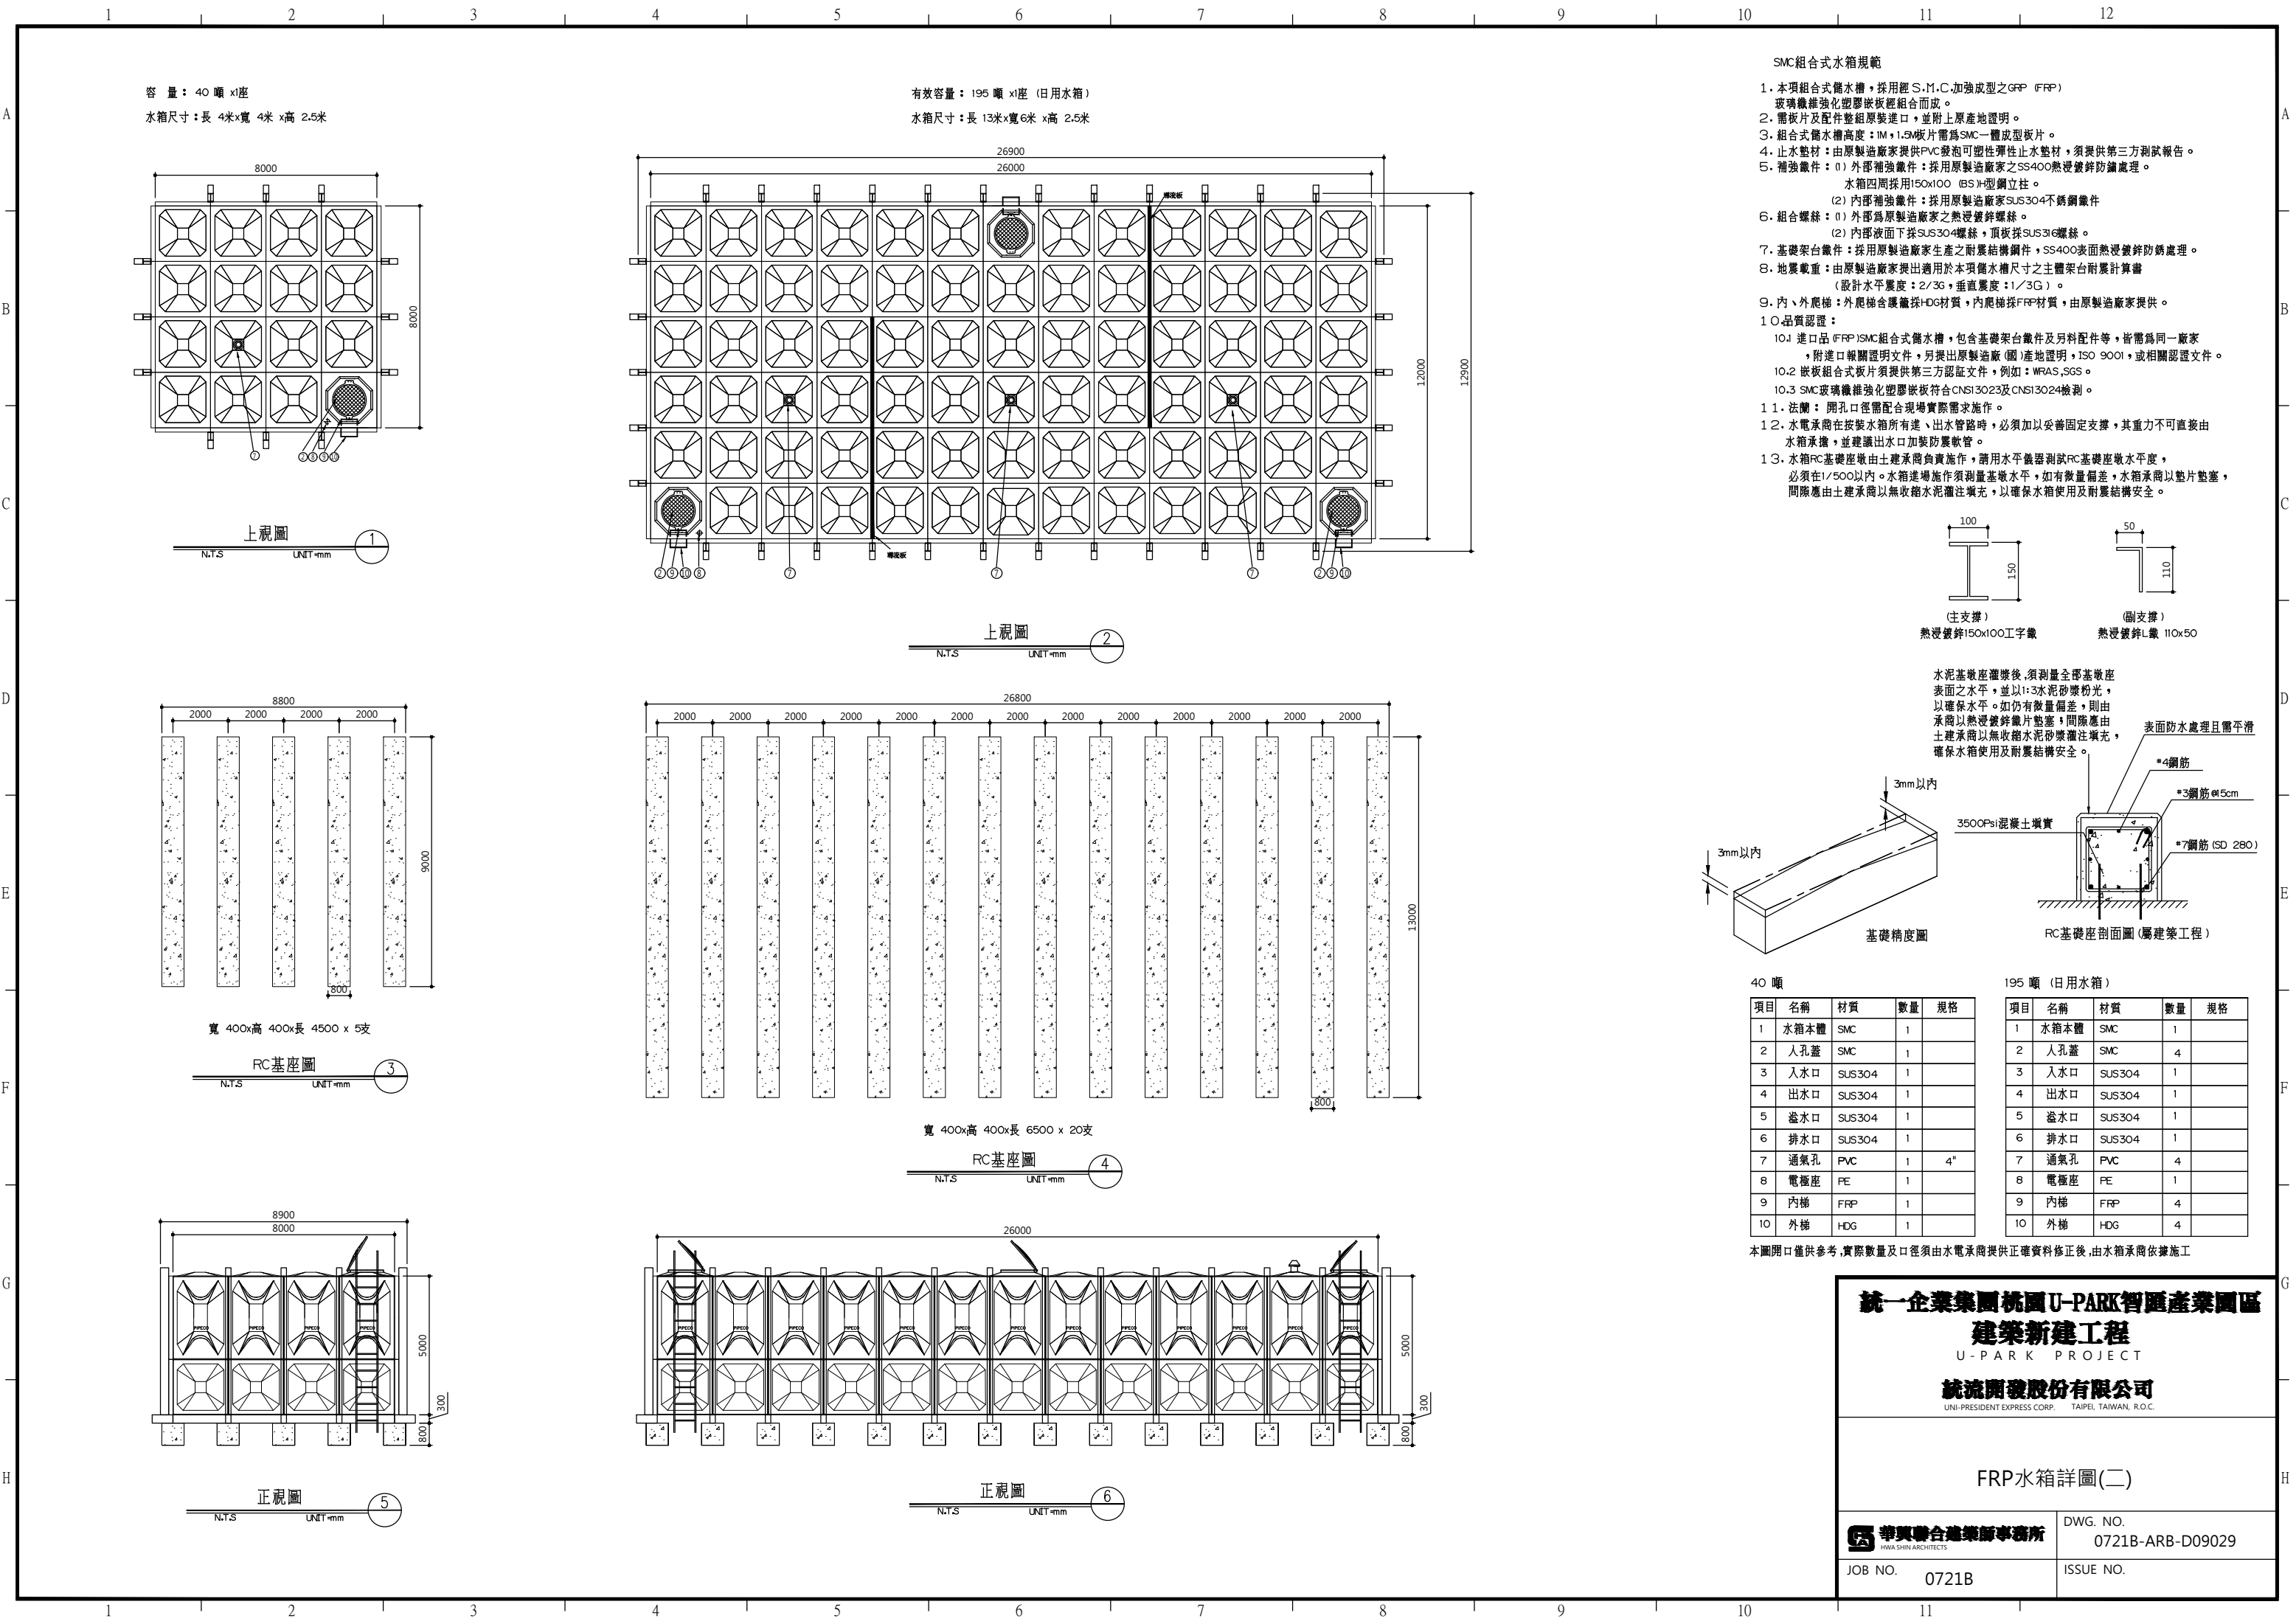


SMC組合式水箱規範

- 1. 本項組合式儲水槽，採用經S.M.C.加強成型之FRP (FRP) 玻璃纖維強化塑膠嵌板組合而成。
- 2. 需板片及配件整組原裝進口，並附上原產地證明。
- 3. 組合式儲水槽高度：1M，1.5M板片需為SMC一體成型板片。
- 4. 止水墊材：由原製造廠家提供PVC發泡可塑性彈性止水墊材，須提供第三方測試報告。
- 5. 補強鐵件：(1) 外部補強鐵件：採用原製造廠家之SS400熱浸鍍鋅防銹處理。
水箱四周採用150x100 (B.S) H型鋼立柱。
(2) 內部補強鐵件：採用原製造廠家SUS304不銹鋼鐵件
- 6. 組合螺絲：(1) 外部為原製造廠家之熱浸鍍鋅螺絲。
(2) 內部液面下採SUS304螺絲，頂板採SUS316螺絲。
- 7. 基礎架台鐵件：採用原製造廠家生產之耐震結構鋼件，SS400表面熱浸鍍鋅防銹處理。
- 8. 地震載重：由原製造廠家提出適用於本項儲水槽尺寸之主體架台耐震計算書 (設計水平震度：2/3G，垂直震度：1/3G)。
- 9. 內、外爬梯：外爬梯合環鐵梯HDG材質，內爬梯採FRP材質，由原製造廠家提供。
- 10. 品質認證：
 - 10.1 進口品 (FRP) SMC組合式儲水槽，包含基礎架台鐵件及另料配件等，皆需為同一廠家，附進口報關證明文件，另提出原製造廠 (國) 產地證明，ISO 9001，或相關認證文件。
 - 10.2 嵌板組合式板片須提供第三方認證文件，例如：WRAS, SGS。
 - 10.3 SMC玻璃纖維強化塑膠嵌板符合CNS13023及CNS13024檢測。
- 11. 法蘭：開口口徑需配合現場實際需求施作。
- 12. 水電承商在按裝水箱所有進、出水管路時，必須加以妥善固定支撐，其重力不可直接由水箱承擔，並建議出水口加裝防震軟管。
- 13. 水箱RC基礎座墩由土建承商負責施作，請用水平儀器測試RC基礎座墩水平度，必須在1/500以內。水箱進場施作須測量基礎水平，如有數量偏差，水箱承商以墊片墊塞，間隙應由土建承商以無收縮水泥灌注填充，以確保水箱使用及耐震結構安全。

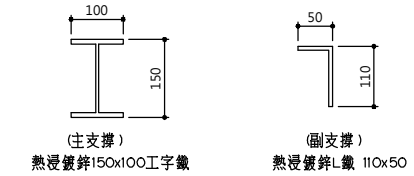

水泥基礎座灌漿後，須測量全部基礎座表面之水平，並以1:3水泥砂漿粉光，以確保水平。如仍有數量偏差，則由承商以熱浸鍍鋅鐵片墊塞，間隙應由土建承商以無收縮水泥砂漿灌注填充，確保水箱使用及耐震結構安全。

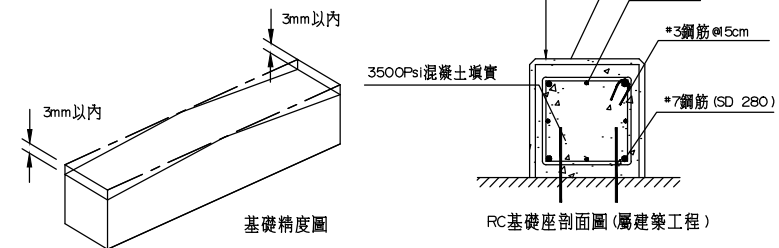

40 噸

項目	名稱	材質	數量	規格
1	水箱本體	SMC	1	
2	人孔蓋	SMC	1	
3	入水口	SUS304	1	
4	出水口	SUS304	1	
5	溢水口	SUS304	1	
6	排水口	SUS304	1	
7	通氣孔	PVC	1	4"
8	電極座	PE	1	
9	內梯	FRP	1	
10	外梯	HDG	1	

195 噸 (日用水箱)

項目	名稱	材質	數量	規格
1	水箱本體	SMC	1	
2	人孔蓋	SMC	4	
3	入水口	SUS304	1	
4	出水口	SUS304	1	
5	溢水口	SUS304	1	
6	排水口	SUS304	1	
7	通氣孔	PVC	4	
8	電極座	PE	1	
9	內梯	FRP	4	
10	外梯	HDG	4	

本圖開口僅供參考，實際數量及口徑須由水電承商提供正確資料修正後，由水箱承商依據施工

統一企業集團

桃園U-PARK智匯產業園區

建築新建工程


U-PARK PROJECT

統流開發股份有限公司

UNI-PRESIDENT EXPRESS CORP. TAIPEI, TAIWAN, R.O.C.

FRP水箱詳圖(二)

	DWG. NO. 0721B-ARB-D09029
JOB NO. 0721B	ISSUE NO.

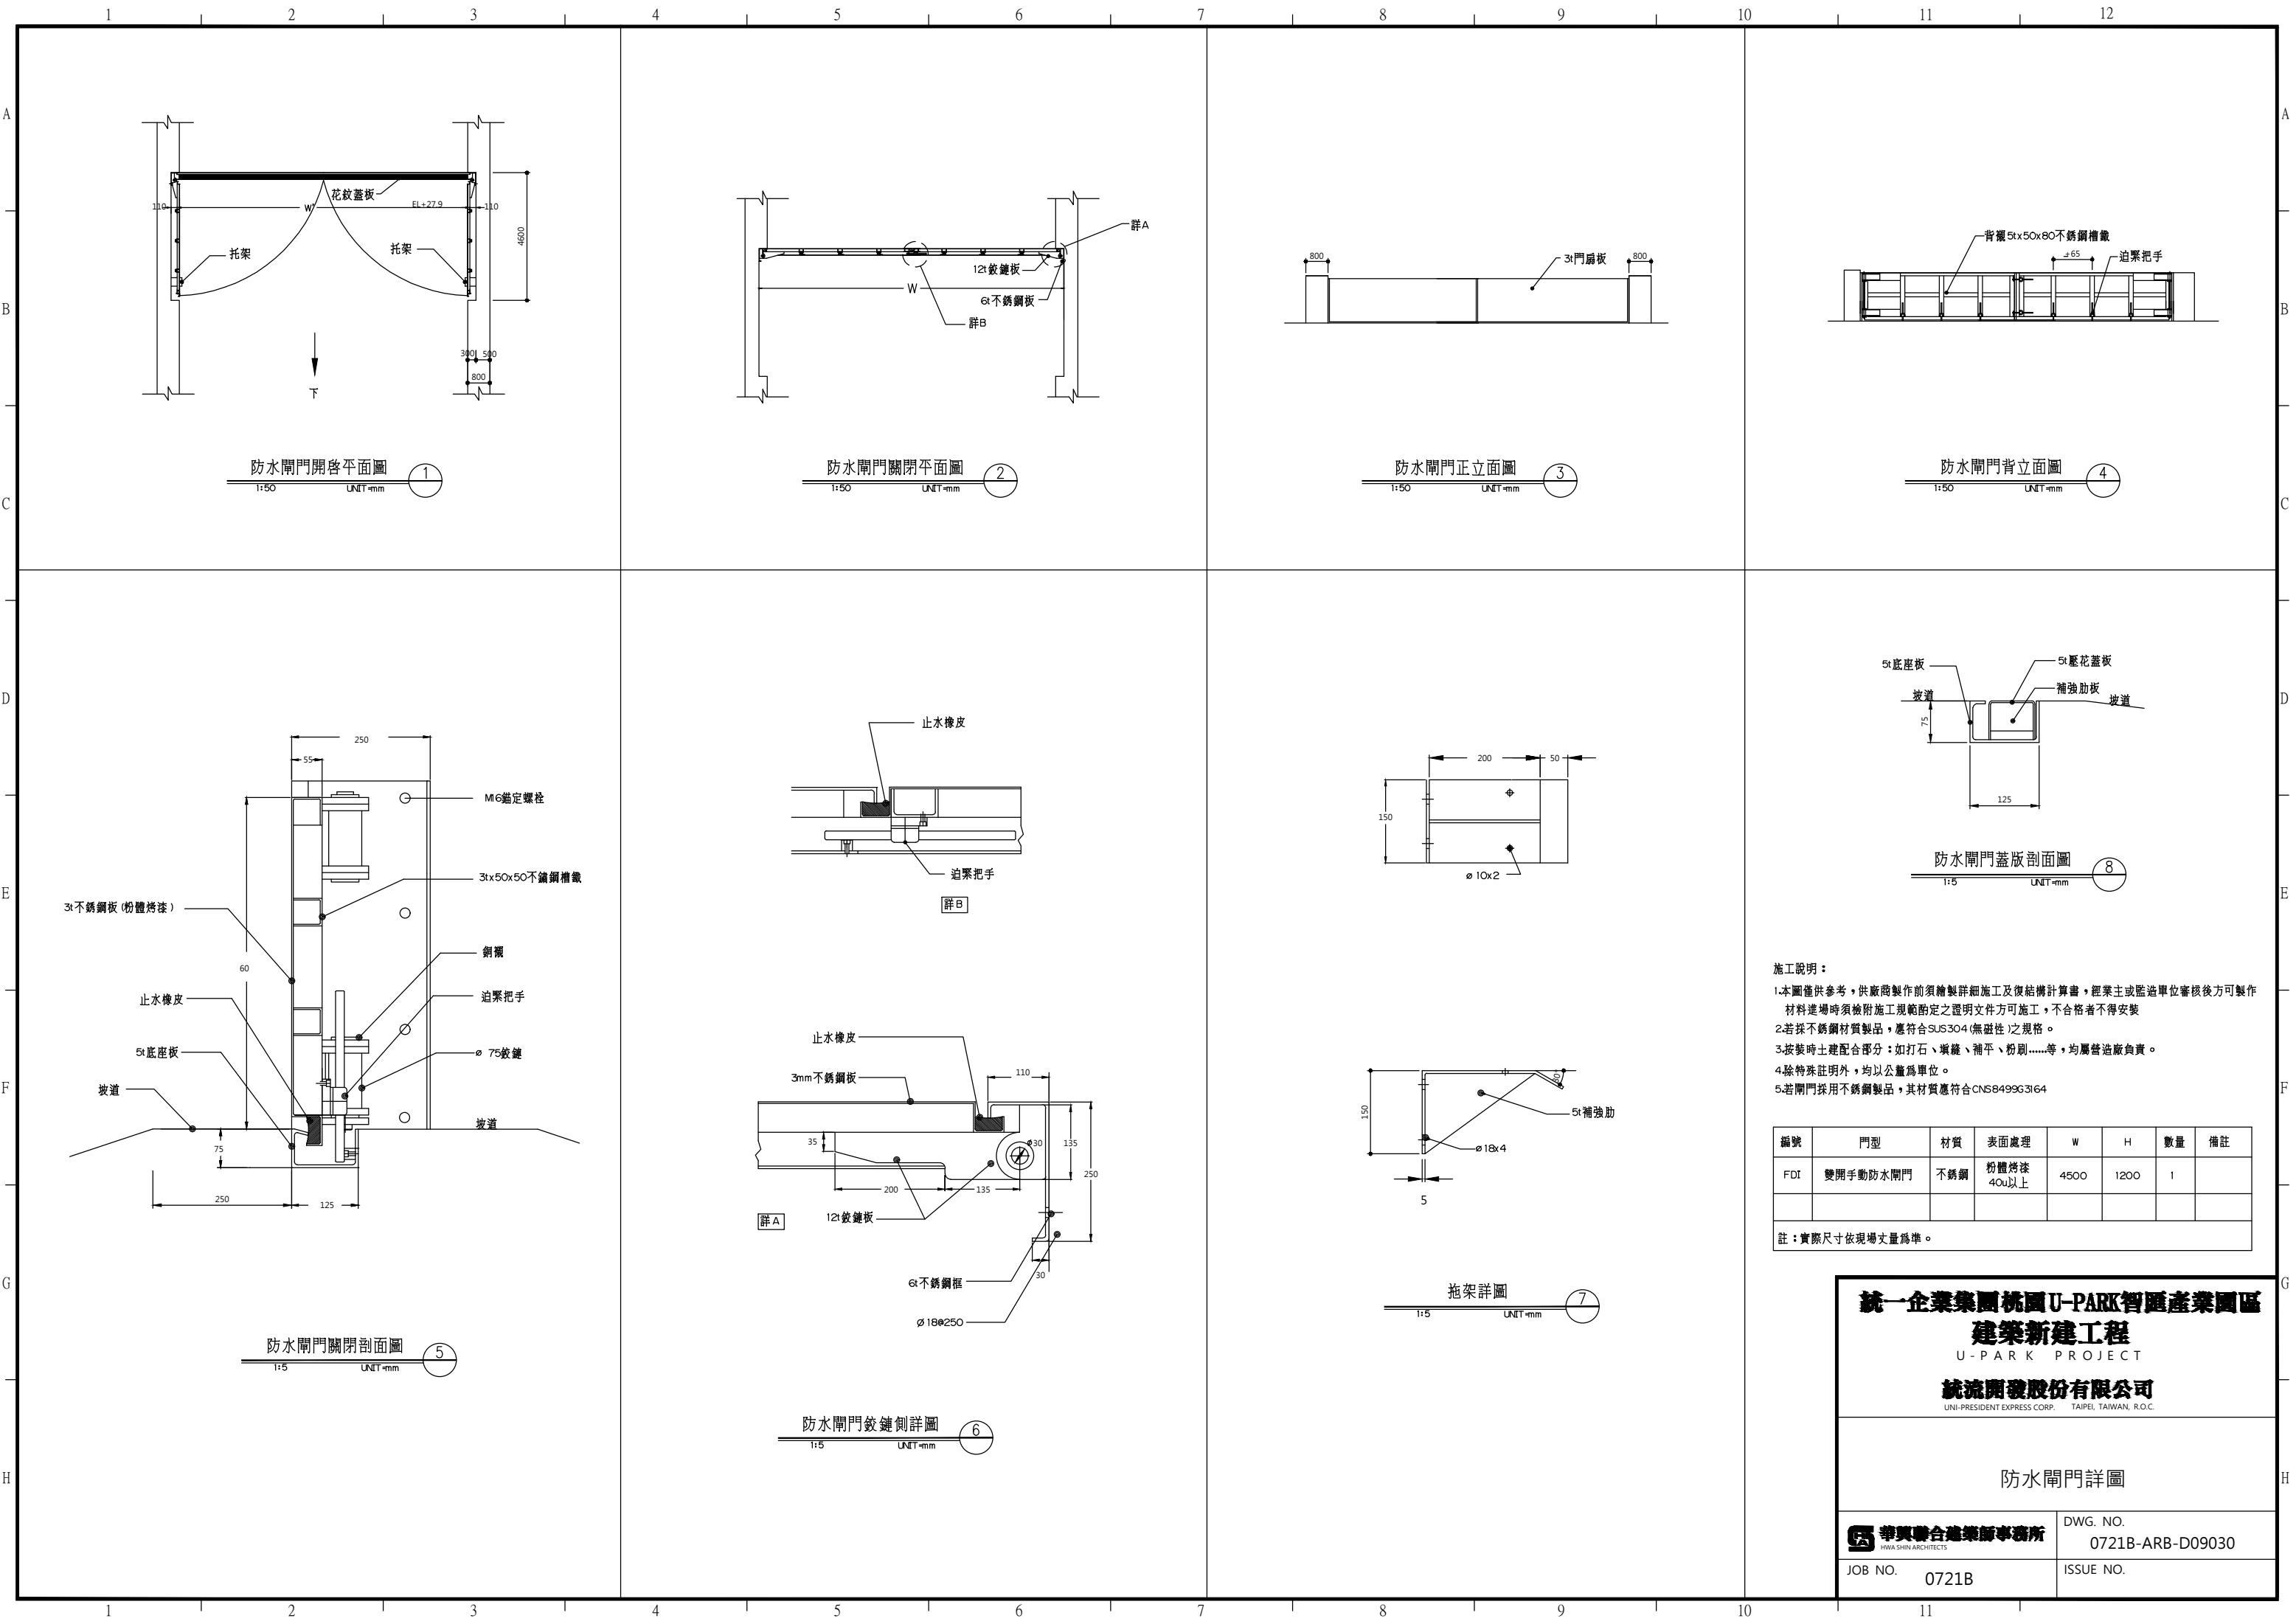

施工說明：

1.本圖僅供參考，供廠商製作前須繪製詳細施工及復結構計算書，經業主或監造單位審核後方可製作
材料進場時須檢附施工規範酌定之證明文件方可施工，不合格者不得安裝

2.若採不銹鋼材質製品，應符合SUS304(無磁性)之規格。

3.按裝時土建配合部分：如打石、填縫、補平、粉刷.....等，均屬營造廠負責。

4.除特殊註明外，均以公釐為單位。

5.若閘門採用不銹鋼製品，其材質應符合CNS8499G3164


編號	門型	材質	表面處理	W	H	數量	備註
FDI	雙開手動防水閘門	不銹鋼	粉體烤漆 40u以上	4500	1200	1	

註：實際尺寸依現場丈量為準。


統一企業集團桃園U-PARK智匯產業園區
建築新建工程
U-PARK PROJECT
統流開發股份有限公司
UNI-PRESIDENT EXPRESS CORP. TAIPEI, TAIWAN, R.O.C.

防水閘門詳圖


 華興聯合建築師事務所 HWA SHIN ARCHITECTS	DWG. NO. 0721B-ARB-D09030
JOB NO. 0721B	ISSUE NO.

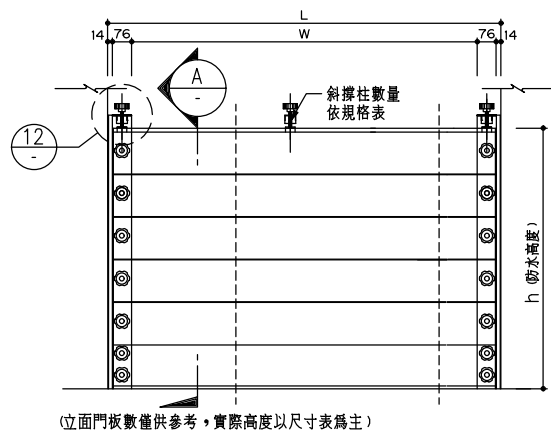

防水閘門立面示意圖--單片式

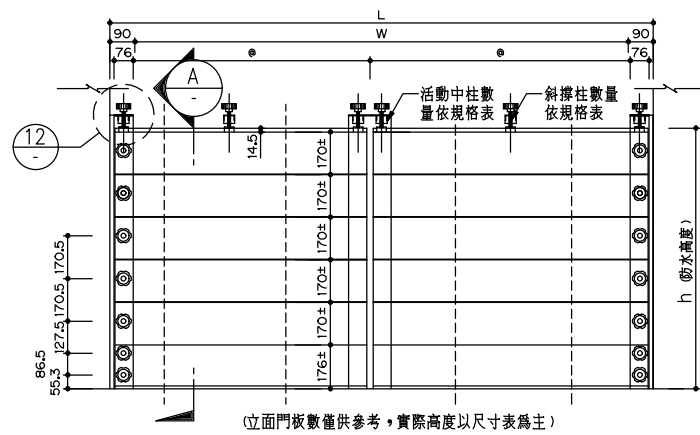


防水閘門立面示意圖--多片式

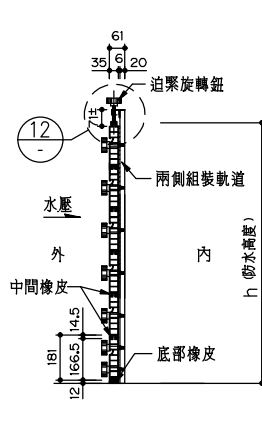

A-A剖面示意圖

N.T.S. UNIT:mm


3

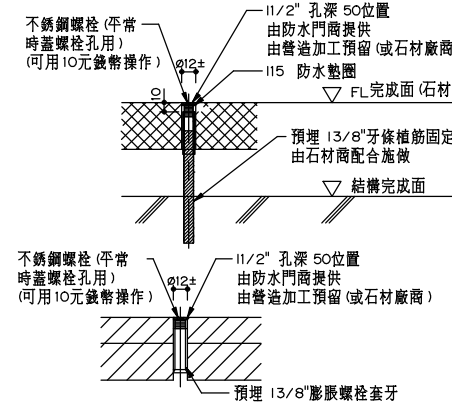

詳圖H(地面固定法大樣)
RC 地坪面鑽孔安裝示意圖

N.T.S. UNIT:mm


4

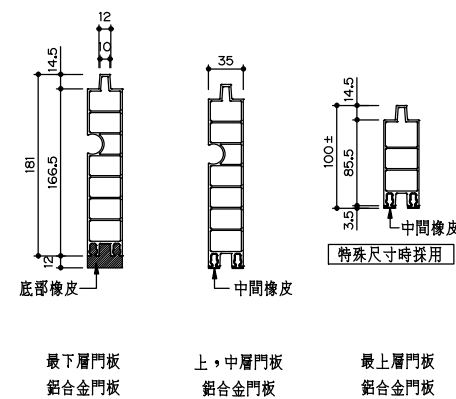


門板詳圖

N.T.S. UNIT=mm


5

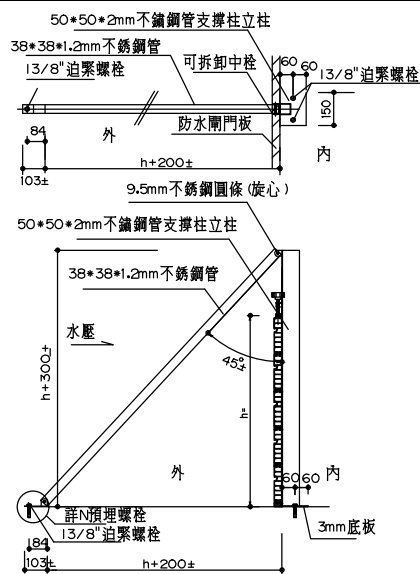

詳圖支撐柱(外拉式)
裝大樣--使用中

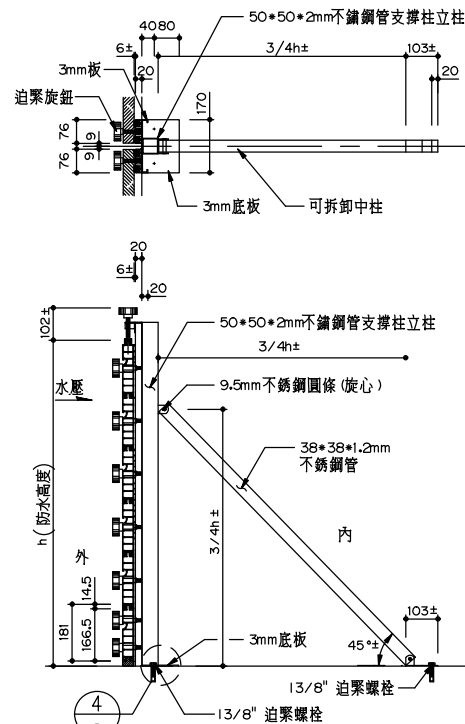


(E-E)中柱安裝大樣--使用中

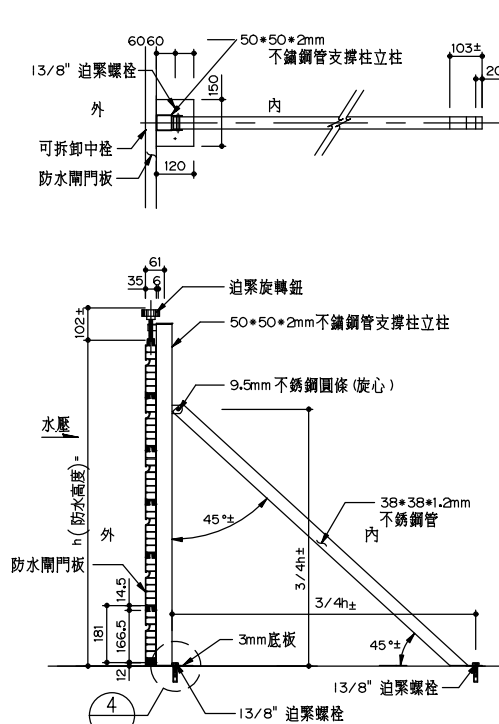


(F-F)支撐柱安裝大樣--使用中


註：防水閘門安裝位置需配合建物建材作設計考慮

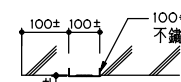


邊框大樣之詳圖 A
未使用中示意圖

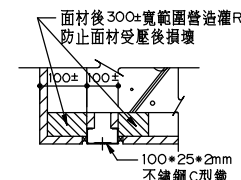


邊框大樣
未使用中示意圖

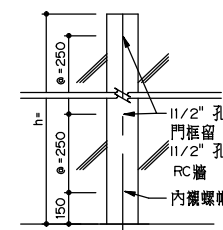


RC 邊框大樣之詳圖 A
牆面嵌板安裝立面圖

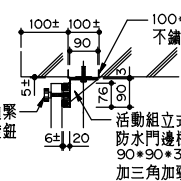


邊框大樣之詳圖 A
RC 牆面安裝示意圖

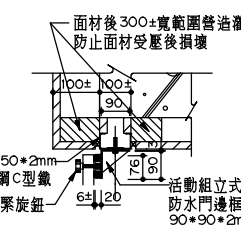

邊框大樣
石材面坎板安裝

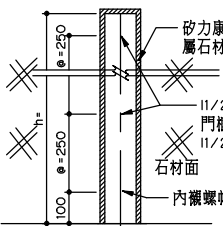

邊框大樣 (單位
石材面嵌板安裝立面圖)

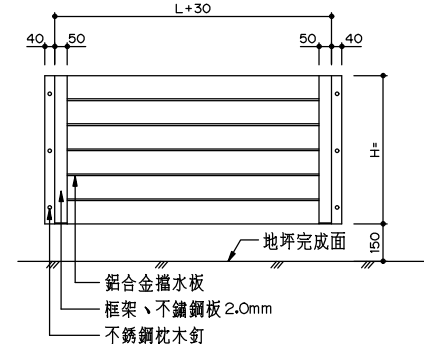


註:置板架設置位置由業主及監造決定後告知

置板架立面圖

N.T.S. UNIT-mm


10

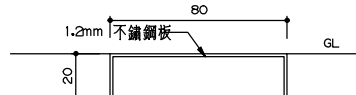

底框詳圖

UNIT=mm

11

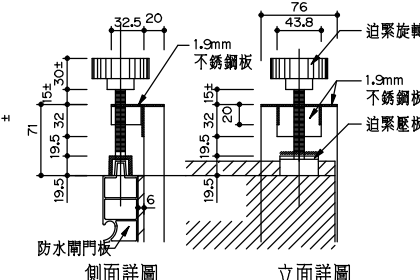


詳圖I


UNIT=mm

12


註：防水閘門安裝位置需配合建物建材作設計考慮

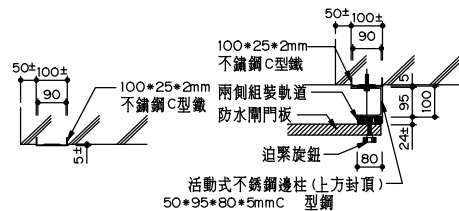


邊框大樣
未使用中示意圖

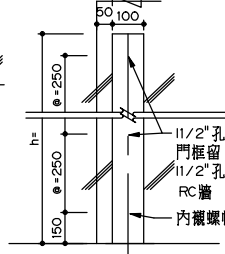

RC 邊框大樣
牆面嵌板安裝立面圖

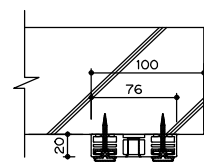


邊框大樣之C詳圖

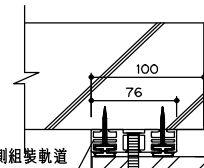

邊框大樣之C詳圖
使用中示意圖

本工程採用熱固性樹脂板

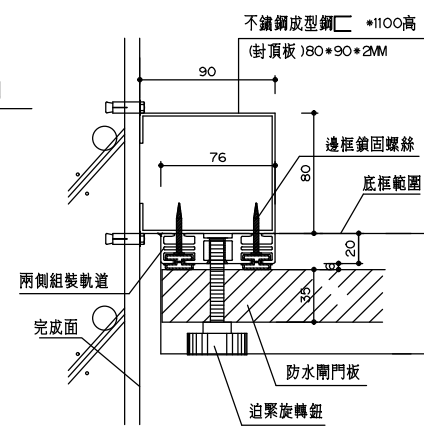

1. 本工程製作前須檢繪詳細施工圖，經工程司審核後方可施工，不合格者不得安裝。
2. 本閘門工程為責任施工，所有應備之零件，不論圖示與否，製造廠商均應具備並依工地工程師之指示裝設。
3. 施工前製造廠商須先繪製現場施工圖經工地工程師核可後方可施工。
4. 除特殊註明者外，均以公釐為單位。
5. 本工程所需配合之土建部份，打石、槽牆、補平、粉刷部份由營造廠負責施工。
6. 本閘門採用不鏽鋼製造，其材質應符合 SUS 304 之規格標準。
7. 本防水閘門工程施工前，應先檢附公立單位之產品防水測試報告（測試報告尺寸不得小於寬度 6M(高度 1.4M)，測試產品之水密性及耐水壓變形，應無滲水及可察覺之變形，超過產品防水測試報告規格之特殊品，可另進行實品防水門之防水試驗，於安裝完成後進行測試，以高壓之水壓作高壓區水試驗，其方法為關閉閘門後，以消防栓之水柱射在閘門水封界上，於另側檢測其貫水試驗結果，檢視無嚴重明顯漏水情況為合格，經審核後，方可施工。
8. 驗收後製造廠商應提供出廠證明及一年保固書。

統一企業集團桃園U-PARK智匯產業園區 建築新建工程 U-PARK PROJECT 統流開發股份有限公司 UNI-PRESIDENT EXPRESS CORP. TAIPEI, TAIWAN, R.O.C.	
防水閘板詳圖	
 華興聯合建築師事務所 HWA SHIN ARCHITECTS	DWG. NO. 0721B-ARB-D09031
JOB NO. 0721B	ISSUE NO.

